


DOOR WINDOW SCHEDULE

MARKED	MASONRY OPENING			DESCRIPTION	QTY.
	WIDTH	SILL	LINTEL		
D1G	6'-3"	-	6'-9"	SINGLE LEAF FLUSH DOOR SHUTTER & OPENABLE GLAZED SHUTTER WITH PRESSED STEEL FRAME AS / DNIT	1
D	3'-3"	-	6'-9"	SINGLE LEAF FLUSH DOOR SHUTTER WITH PRESSED STEEL FRAME AS / DNIT	2
D1	3'-0"	-	6'-9"	SINGLE LEAF FLUSH DOOR SHUTTER WITH PRESSED STEEL FRAME AS / DNIT	2
D2	2'-6"	-	6'-9"	SINGLE LEAF FLUSH DOOR SLIDING SHUTTER WITH PRESSED STEEL FRAME AS / DNIT	1
SD	3'-3"	-	6'-9"	SINGLE LEAF FLUSH DOOR SHUTTER WITH PRESSED STEEL FRAME AS / DNIT	1
W	3'-6"	2'-3"	6'-9"	DOUBLE LEAF OPENABLE GLAZED SHUTTER WITH PRESSED STEEL FRAME AS / DNIT	4
W1	1'-6"	5'-3"	6'-9"	FIXED GLASS WINDOW WITH PRESSED STEEL FRAME AS / DNIT	2
V	3'-3"	7'-6"	10'-6"	FIXED GLASS VENTILATOR WITH PRESSED STEEL FRAME AS / DNIT (ABOVE D)	2
V1	1'-6"	7'-6"	10'-6"	FIXED GLASS VENTILATOR WITH PRESSED STEEL FRAME AS / DNIT (ABOVE W1)	2
V2	6'-3"	7'-6"	10'-6"	FIXED GLASS VENTILATOR & EXHAUST FAN OPENING WITH PRESSED STEEL FRAME AS / DNIT (ABOVE D1G)	1
O	3'-0"	7'-6"	8'-6"	MASONRY OPENING	1

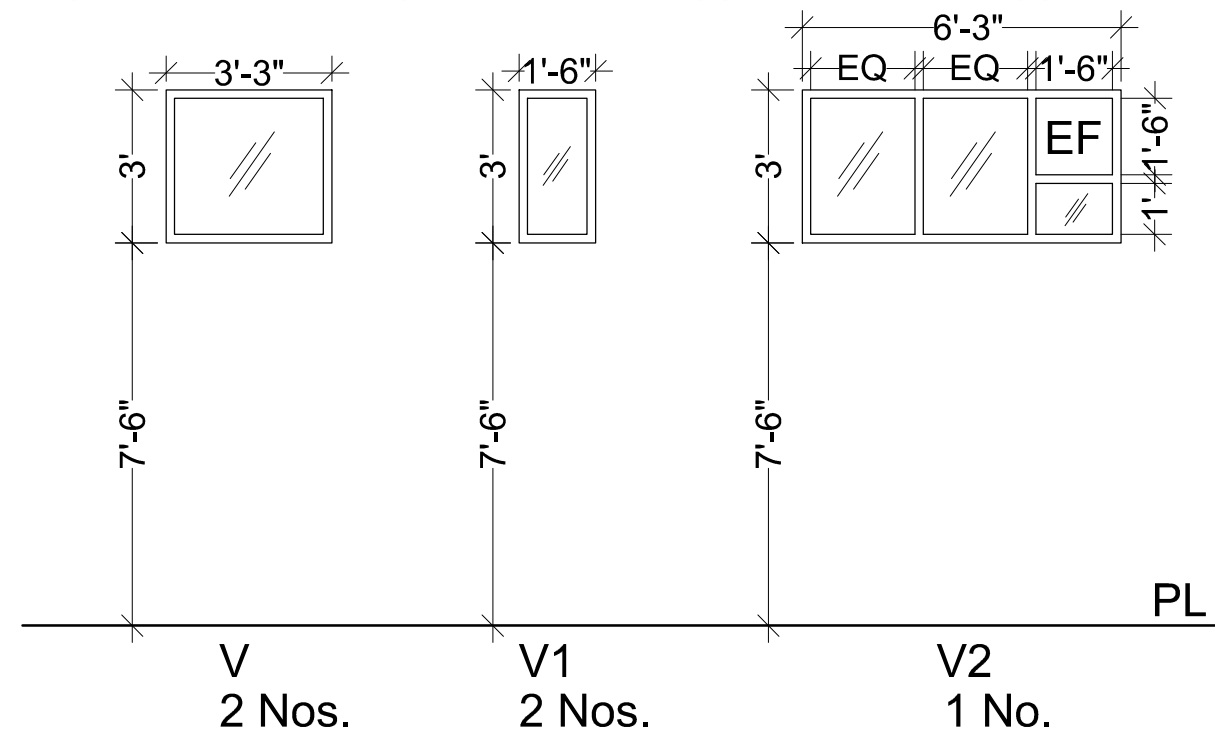

NOTE :-
1. ALL DIMENSION ARE IN FEET INCHES

PROJECT ANGANWARI CENTER AT VARIOUS PLACE			
TITLE DOOR & WINDOW DETAIL			
DRG. NO. AWC-05	SCALE NTS	DATE 05-02-2018	DRAWN BY VIKAS PANNU
EXECUTIVE ENGINEER PANCHAYATI RAJ, SIRSA			