



S. NO.	DATE	DESCRIPTION
--------	------	-------------

--	--	--

THIS DRAWING IS THE PROPERTY OF THE DEPTT. OF ARCHITECTURE, GOVT. OF HARYANA AND MAY NOT BE ALTERED, COPIED, USED IN WHOLE OR IN PART WITHOUT THE PERMISSION OF THIS DEPTT. IN WRITING.

AR. B. B. MEHTA
CHIEF ARCHITECT


AR. HIRSHAN BIRSH
SENIOR ARCHITECT

AR. AMAN JAIN
ARCHITECT
OFFICE OF THE CHIEF
ARCHITECT HARYANA
CHANDIGARH

STANDARD BARAT GHAR
/ COMMUNITY CENTRE
FOR 500 PERSONS

CHECKED BY	SCALE
JOB NO.	DATE
2471 / 500 P	03
DRG. NO.	SEP 2022

FRONT ELEVATION
COLOUR SCHEME

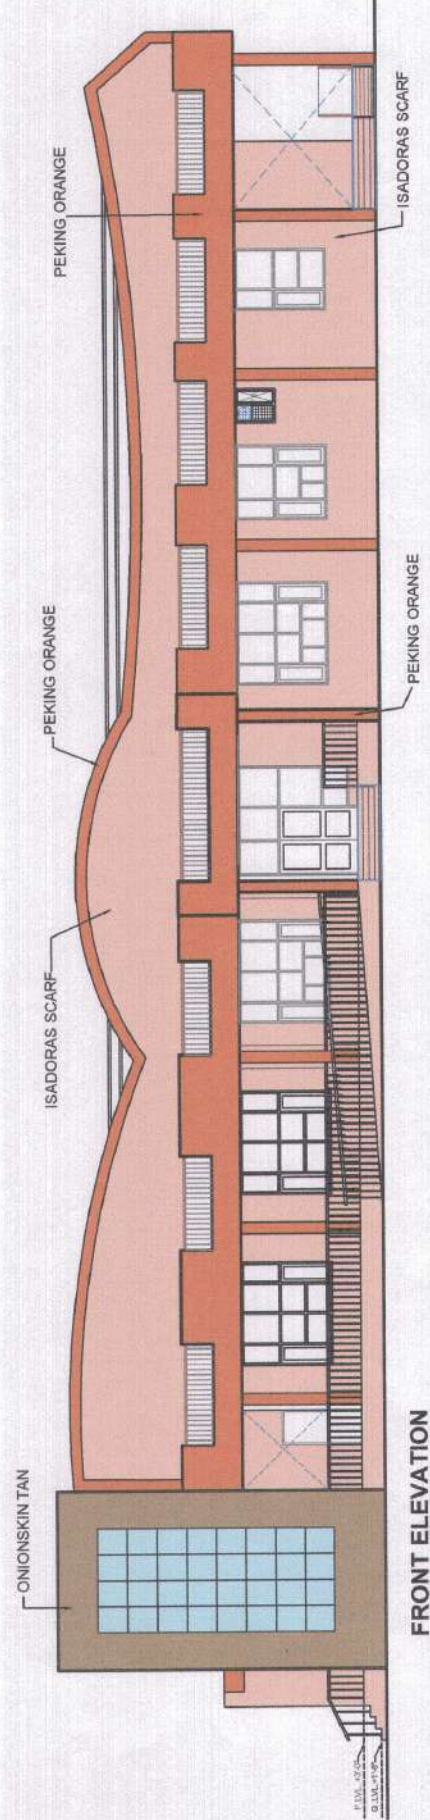

FRONT ELEVATION

EXTERNAL FINISH:-

SHADE	DULUX PAINT
	PEKING ORANGE DULUX 80YR 24/439 (PAGE NO.72)
	ISADORAS SCARF DULUX 80YR 65/196 (PAGE NO. 71)
	ONIONSKIN TAN DULUX 00YY 37/221 (PAGE NO.252)

COLOURS HAS BEEN TAKEN FROM DULUX SHADE CARD FOR REFERENCE ONLY

ALL THE ABOVE SHADES HAVE BEEN TAKEN FROM THE FANDAK DULUX OF PAINTSIASIAN
PAINTS CATALOGUE FOR REFERENCE OF COLOUR/ SHADE ONLY. TYPE OF PAINTS &
SPECIFICATIONS MAY BE ADOPTED AS PER PROVISIONS MADE IN DNITHARYANA PWD B& R
SCHEDULE OF RATES.

INTERNAL FINISH:-

• ALL INTERNAL WALLS OF ROOMS SHALL BE FINISHED WITH OIL BOUND DISTEMPER OF ARIZONA WHITE DULUX 42YY 87/084 (PAGE NO. 260). • ALL CEILINGS SHALL BE FINISHED WITH WHITE COLOUR.
JOINERY:- • ALL DOORS & WINDOWS FRAME, WINDOWS SHUTTER AND GRILL SHALL BE PAINTED WITH SYNTHETIC ENAMEL PAINT OF CHOCOLATE BROWN SHADE. • WIRE MESH SHALL BE PAINTED IN SYNTHETIC ENAMEL PAINT OF ADMIRAL BLUE SHADE. • ALL DOORS SHUTTER SHALL BE PAINTED WITH SYNTHETIC ENAMEL PAINT OF PAROCHMENT DULUX 40YY 70/138 (PAGE NO.260).

COLOURS HAS BEEN TAKEN FROM DULUX SHADE CARD FOR REFERENCE ONLY