



REVISION	DATE	DESCRIPTION	BY

THIS DRAWING IS THE PROPERTY OF THE DEPTT OF ARCHITECTURE, GOVT. OF HARYANA AND MAY NOT BE ALTERED, COPIED OR USED IN WHOLE OR IN PART WITHOUT THE PERMISSION OF THIS DEPTT. IN WRITING.

GENERAL NOTES

IN CASE OF ANY DISCREPANCY IN ARCHITECTURAL DRAWINGS, THE DRAWING SHALL BE CONSULTED BEFORE TAKING ANY ACTION AT SITE.

MR. B. B. MEHTA
CHIEF ARCHITECT

MR. LITENDRA SINGH
SENIOR ARCHITECT

MR. ANSHU JAIN
ARCHITECT


MR. SUDIP CHANDRAN
ARCHITECT

OFFICE OF THE CHIEF
ARCHITECT HARYANA
CHANDIGARH.

STANDARD BLOCK OFFICE
BUILDING

DRAWN BY: 1311
SCALE: 1:100
DATE: SEP 2022

FRONT ELEVATION
COLOUR SCHEME

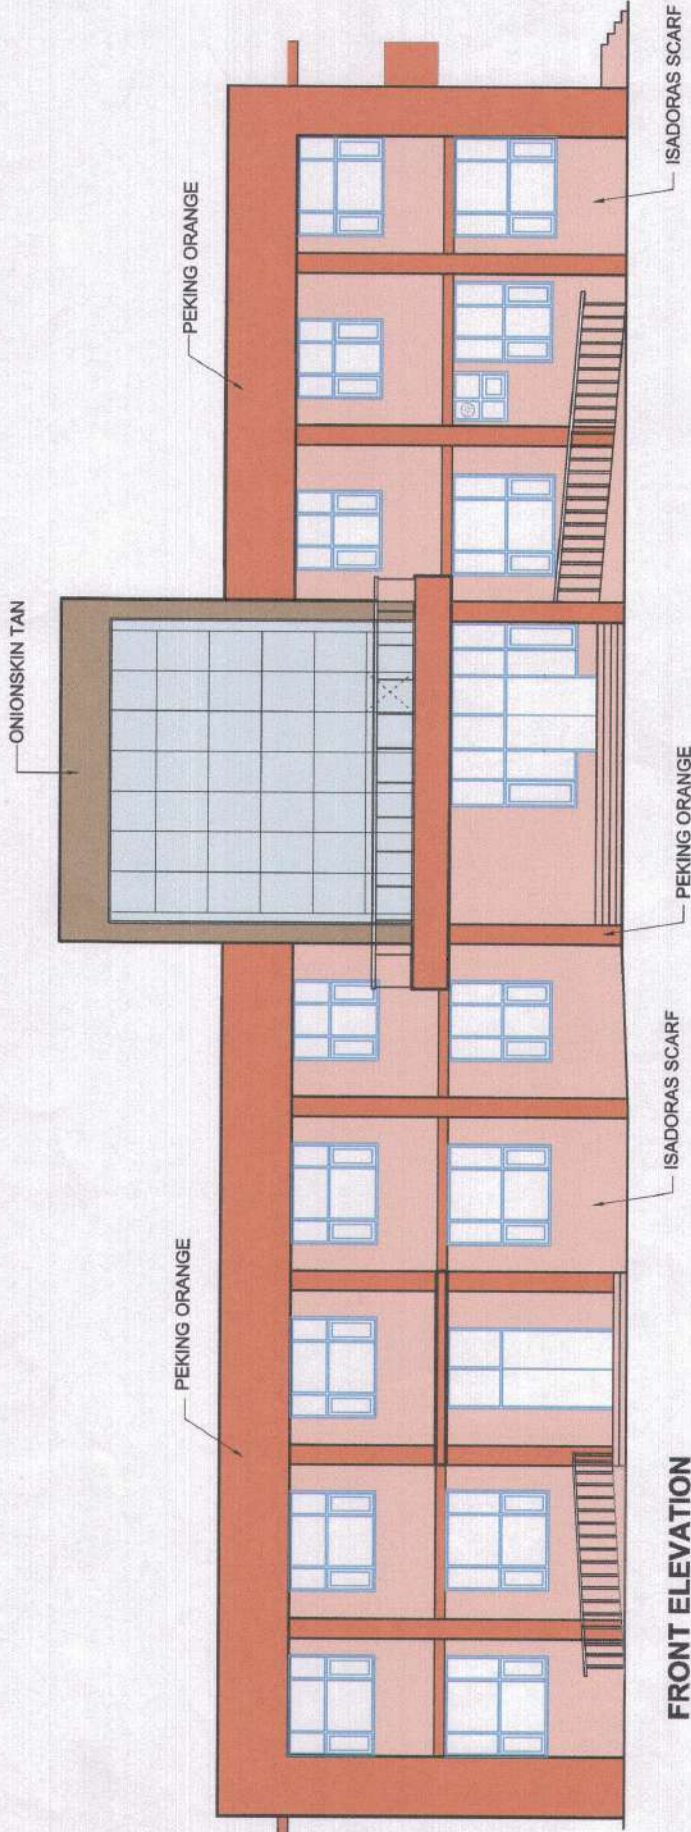

FRONT ELEVATION

INTERNAL FINISH:-

- ALL INTERNAL WALLS OF ROOMS SHALL BE FINISHED WITH OIL BOUND DISTEMPER OF ARIZONA WHITE DULUX 42YY 87/084 (PAGE NO. 260).
- ALL CEILINGS SHALL BE FINISHED WITH WHITE COLOUR.
- JOINERY:-**
- ALL DOORS & WINDOWS FRAME, WINDOWS SHUTTER AND GRILL SHALL BE PAINTED WITH SYNTHETIC ENAMEL PAINT OF CHOCOLATE BROWN SHADE.
- WIRE MESH SHALL BE PAINTED IN SYNTHETIC ENAMEL PAINT OF ADMIRAL BLUE SHADE.
- ALL DOORS SHUTTER SHALL BE PAINTED WITH SYNTHETIC ENAMEL PAINT OF PARCHMENT DULUX 40YY 70/138 (PAGE NO.260).

COLOURS HAS BEEN TAKEN FROM DULUX SHADE CARD FOR REFERENCE ONLY

EXTERNAL FINISH:-

SHADE	DULUX PAINT
	PEKING ORANGE DULUX 60YR 24/439 (PAGE NO.72)
	ISADORAS SCARF DULUX 60YR 65/196 (PAGE NO. 71)
	ONIONSKIN TAN DULUX 00YY 37/221 (PAGE NO.252)

COLOURS HAS BEEN TAKEN FROM DULUX SHADE CARD FOR REFERENCE ONLY

ALL THE ABOVE SHADES HAVE BEEN TAKEN FROM THE FANDAK DULUX OF PAINTS/ASIAN PAINTS CATALOGUE FOR REFERENCE OF COLOUR/ SHADE ONLY. TYPE OF PAINTS & SPECIFICATIONS MAY BE ADOPTED AS PER PROVISIONS MADE IN DNIT/HARYANA PWD B & R SCHEDULE OF RATES.