



S. NO. DATE DESCRIPTION

THIS DRAWING IS THE PROPERTY OF THE DEPT. OF ARCHITECTURE, GOVT. OF HARYANA AND MAY NOT BE ALTERED, COPIED, USED IN WHOLE OR IN PART WITHOUT THE PERMISSION OF THIS DEPT. IN WRITING.

AR.B.B. MEHTA
CHIEF ARCHITECT

APR 11/2022
SECTION ARCHITECT

APR 11/2022
OFFICE OF THE CHIEF
ARCHITECT HARYANA
CHANDIGARH,
STANDARD BARAT GHAR
/ COMMUNITY CENTRE
FOR 250 PEOPLES

SCALE IN

JOB NO.

2471 / 250 P


DRG. NO.

03

DATE

SEP 2022

FRONT ELEVATION
COLOUR SCHEME

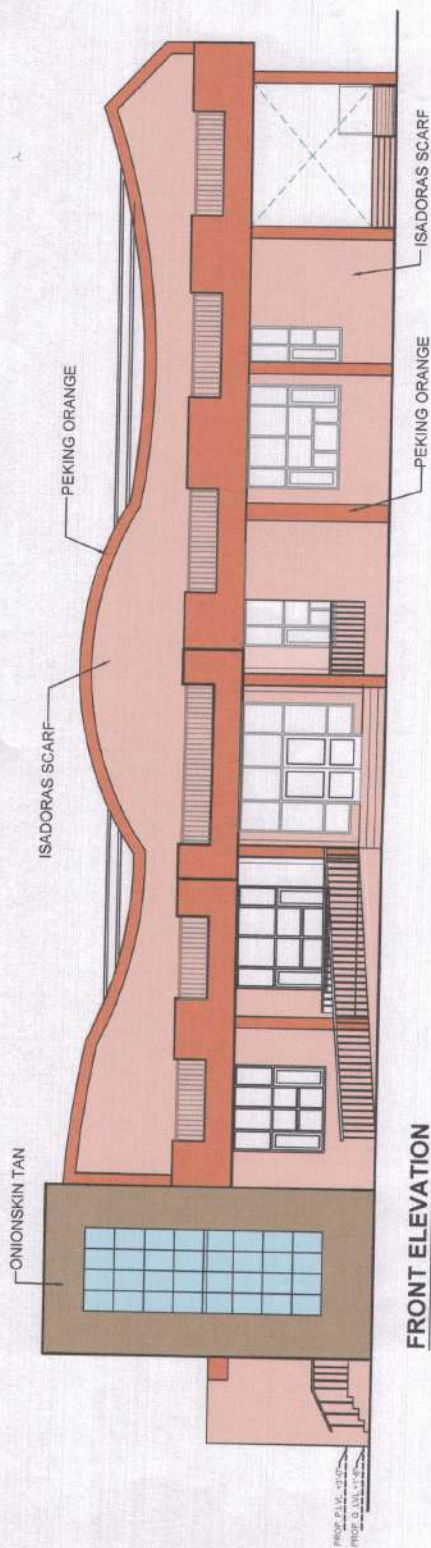

EXTERNAL FINISH:-

SHADE	DULUX PAINT
	PEKING ORANGE DULUX 60YR 24/439 (PAGE NO.72)
	ISADORAS SCARF DULUX 60YR 65/196 (PAGE NO. 71)
	ONIONSKIN TAN DULUX 00YY 37/221 (PAGE NO.252)

COLOURS HAS BEEN TAKEN FROM DULUX SHADE CARD FOR REFERENCE ONLY

ALL THE ABOVE SHADES HAVE BEEN TAKEN FROM THE FANDAK DULUX OF PAINTS/ASIAN PAINTS CATALOGUE FOR REFERENCE OF COLOUR/SHADE ONLY. TYPE OF PAINTS & SPECIFICATIONS MAY BE ADOPTED AS PER PROVISIONS MADE IN DNTHARTANA PWD B&R SCHEDULE OF RATES.

INTERNAL FINISH:-

*ALL INTERNAL WALLS OF ROOMS SHALL BE FINISHED WITH OIL BOUND DISTEMPER OF ARIZONA WHITE DULUX 42YY 87/084 (PAGE NO. 260).
*ALL CEILINGS SHALL BE FINISHED WITH WHITE COLOUR.

JOINERY:-

*ALL DOORS & WINDOWS FRAME, WINDOWS SHUTTER AND GRILL SHALL BE PAINTED WITH SYNTHETIC ENAMEL PAINT OF CHOCOLATE BROWN SHADE.
*WIRE MESH SHALL BE PAINTED IN SYNTHETIC ENAMEL PAINT OF ADMIRAL BLUE SHADE.
*ALL DOORS SHUTTER SHALL BE PAINTED WITH SYNTHETIC ENAMEL PAINT OF PARCHEMENT DULUX 40YY 70/138 (PAGE NO.260).

COLOURS HAS BEEN TAKEN FROM DULUX SHADE CARD FOR REFERENCE ONLY