

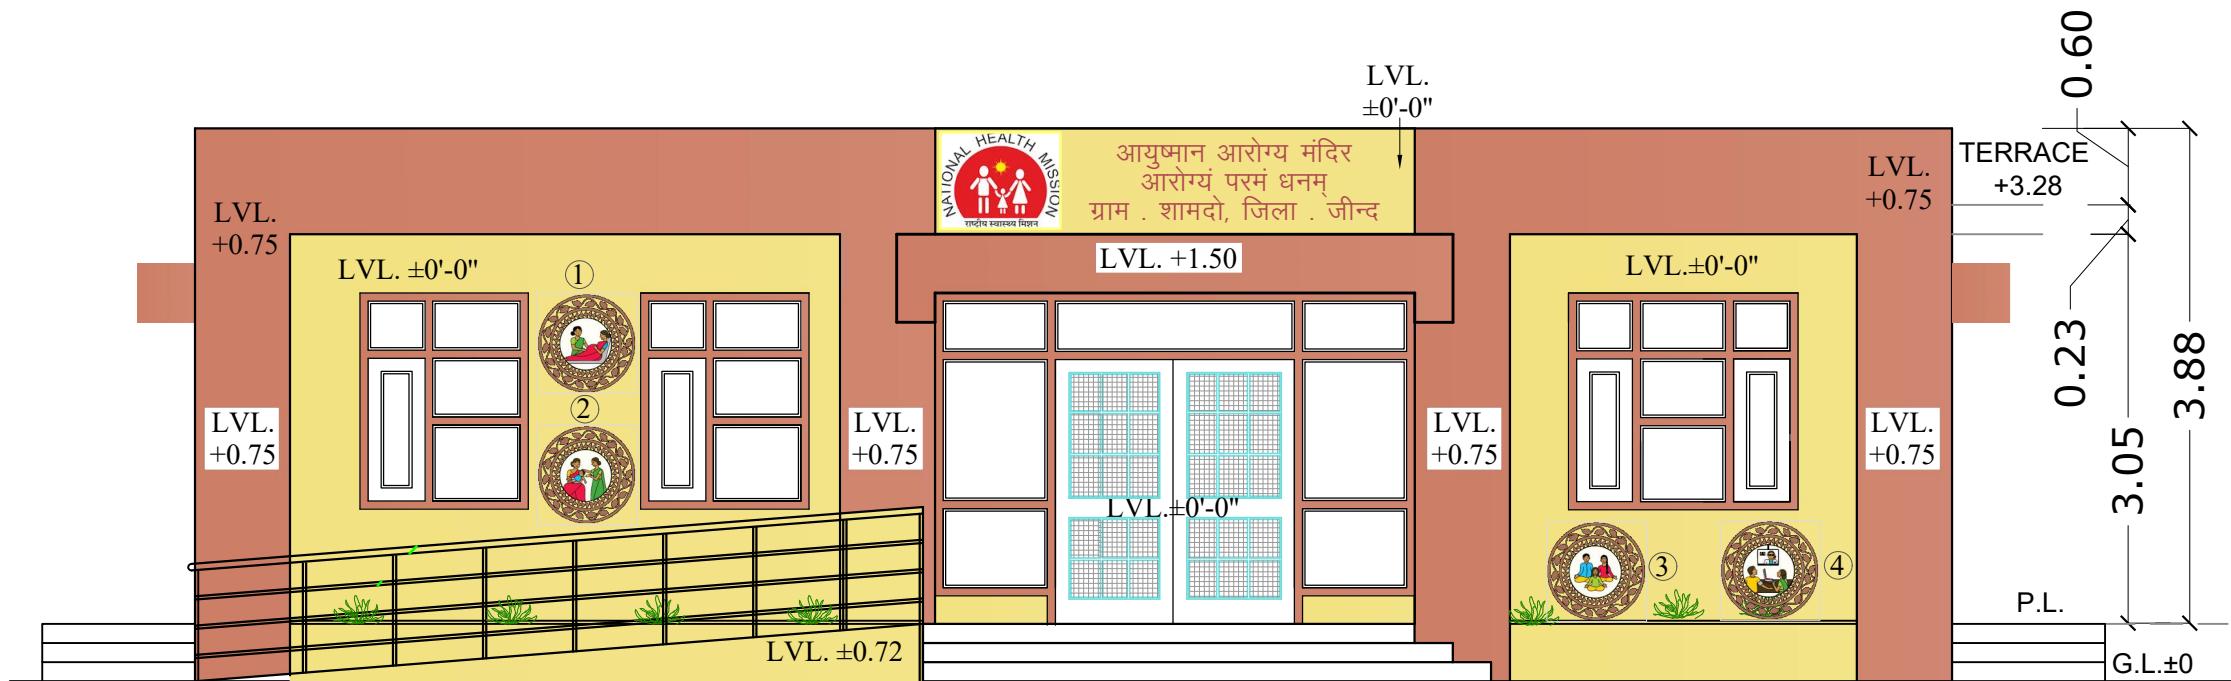
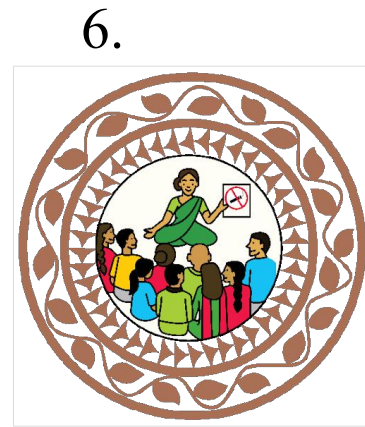
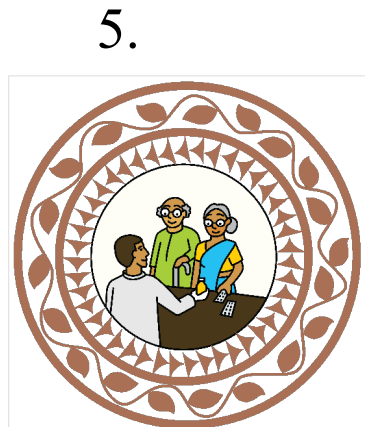


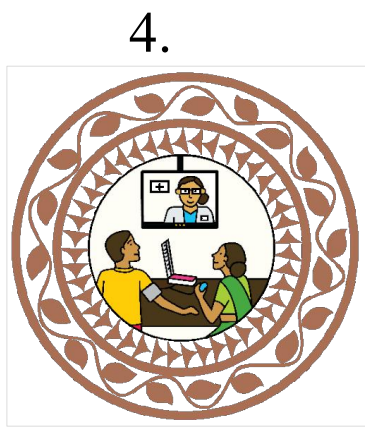

FRONT ELEVATION

COLOURS TO BE USED IN 6 NOS. ILLUSTRATIONS

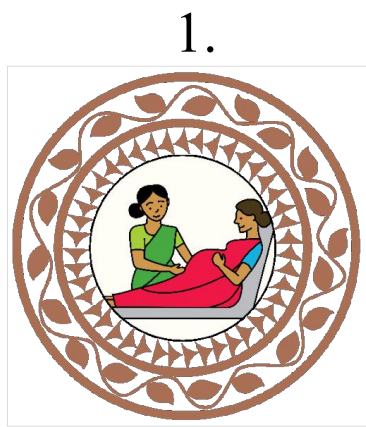

NOTE:- COLOURS AS PER REFERENCE MANUAL.
(FACADE BRANDING FOR HEALTH WELLNESS CENTRE)
AYUSHMAN BHARAT SCHEME 30 MAY 2018 VERSION 3

COLOURS TO BE USED ON FACADE



NOTES:-

INTERNAL FINISH:-
ALL WALLS OF ROOMS SHALL BE FINISHED WITH OIL BOUND DISTEMPER OF MOON YEAR SHADE (ASIAN PAINTS SHADE NO. 7924) AND CEILING SHALL BE FINISHED WITH OIL BOUND DISTEMPER OF PURE IVORY SHADE (ASIAN PAINT SHADE NO.L-124). THE WALLS OF CIRCULATION AREAS UPTO 4'-6" HEIGHT SHALL BE FINISHED WITH CERAMIC TILE DADO OF 12" X 18" SIZE AND WALLS OF CIRCULATION AREA ABOVE 4'-6" HEIGHT SHALL BE FINISHED WITH OIL BOUND DISTEMPER OF MOON YEAR SHADE (ASIAN PAINTS SHADE NO. 7924) .

JOINERY :-
ALL PRESSED STEEL FRAMES, GRILLS AND STYLES OF WINDOW SHUTTERS SHALL BE PAINTED WITH SYNTHETIC ENAMEL PAINT OF ETHNIC BROWN SHADE (ASIAN PAINT SHADE NO. 8589).

ALL DOOR SHUTTERS SHALL BE PAINTED WITH SYNTHETIC ENAMEL PAINT OF WILD HONEY SHADE (ASIAN PAINT SHADE NO. 7922).

WIRE-MESH SHALL BE PAINTED WITH SYNTHETIC ENAMEL PAINT OF CLASSIC BLUE SHADE (ASIAN PAINT SHADE NO. 9190).


EXTERNAL FINISH:-
ALL EXTERNAL WALLS HAVING CEMENT PLASTER SHALL BE FINISHED WITH EXTERIOR PAINT OF YELLOW METAL SHADE (ASIAN PAINT SHADE NO. 7920).

ALL PROJECTIONS/SUNSHADES SHALL BE FINISHED WITH EXTERIOR PAINT OF ETHNIC BROWN SHADE (ASIAN PAINT SHADE NO. 8589).

THE COLOUR SCHEME OF HWC HAVING AN AREA OF 187.60 SQ.MTR WAS PREPARED BY REFERRING "FACADE BRANDING FOR HEALTH WELLNESS CENTRE AYUSHMAN BHARAT SCHEME 30 MAY 2018 VERSION 3", AND THE SAME WAS APPROVED BY THE DIRECTOR GENERAL HEALTH SERVICES HARYANA VIDE MEMO NO. CONST./FC-XV/2025/676 DATED 04.04.2025.

LATER THE DIRECTOR GENERAL HEALTH SERVICES HARYANA VIDE E-MAIL DATED 27.01.2025, HAS COMMUNICATED THAT AYUSHMAN BHARAT-HEALTH AND WELLNESS CENTRE HAVE TO BE RENAMED AS 'AYUSHMAN AROGYA MANDIR' WITH THE TAGLINE 'AROGYAM PARMAM DHANAM' TO REALIZE A DREAM OF AYUSHMAN BHARAT i.e. HEALTHY INDIA AND REQUESTED TO REVISE THE DRAWINGS OF EXTERIOR COLOUR SCHEME OF FACADE BRANDING. AS SUCH, THE SAME HAVE BEEN REVISED.

THE SAME COLOUR SCHEME AND TAGLINES AS SUGGESTED BY DGHS HARYANA HAS BEEN INCORPORATED INTO THIS COLOUR SCHEME AS WELL.

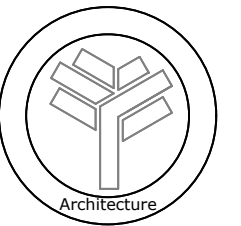

NOTES:-

- THIS DRAWING IS THE PROPERTY OF THE DEPARTMENT OF ARCHITECTURE, GOVT. OF HARYANA. THIS DRAWING MAY NOT BE ALTERED, COPIED, USED IN WHOLE OR IN PART WITHOUT THE PERMISSION OF THIS DEPARTMENT IN WRITING.
- THE DISCREPANCY, IF ANY MUST BE BROUGHT TO THE NOTICE OF THE DEPARTMENT OF ARCHITECTURE HARYANA BEFORE ANY ACTION AT SITE.
- THE SPECIFICATION AND SHADES FOR THE EXTERIOR PAINTS HAVE BEEN ADOPTED FROM REFERENCE MANUAL, i.e. (FACADE BRANDING FOR HEALTH WELLNESS CENTRE- AYUSHMAN BHARAT SCHEME 30 MAY 2018 VERSION 3) PROVIDED BY DIRECTOR GENERAL HEALTH SERVICES, HARYANA OFFICE.
- THE COLOURS SHOWN IN DRAWING MAY VARY DUE TO PRINT MEDIA.
- FIRST QUALITY PAINTS SHALL BE USED. COMPANY NAME AS MENTIONED ARE ONLY FOR REFERENCE PURPOSE, ANY MAKE OF PAINT MAY BE USED AS PER PWD SPECIFICATIONS/ DNIT.

AR. SANJEEV KUMAR
(CHIEF ARCHITECT)

AR. DEVENDER SINGH
(SENIOR ARCHITECT)

AR. LALIT KUMAR (ARCHITECT) (SAPNA RANI JUNEJA)
(ASSTT.ARCHITECT)

OFFICE OF THE
CHIEF ARCHITECT
HARYANA, CHANDIGARH

STANDARD DRAWING OF HEALTH
WELLNESS CENTRE DESIGN -I WITHOUT
LABOUR ROOM AND RESIDENCES.

NISHA RANI (A.D.) TARSEM KUMAR (A.D.)
DEALT BY:- CHECKED BY:-

JOB NO 3152 SCALE NTS

DRG.NO DATE MAY 2026

DETAIL OF EXTERIOR COLOUR SCHEME
OF FACADE BRANDING-01 FOR HWC
HAVING COVERED AREA OF 187.60
SQ.MTR.