



REVISION
DATE



DESCRIPTION

BY

THIS DRAWING IS THE PROPERTY OF THE GOVERNMENT OF ARCHITECTURE, HARYANA AND NOT BE ALTERED OR REPRODUCED IN ANY MANNER WITHOUT THE PERMISSION OF THE DEPTT. IN WRITING.

GENERAL NOTES

IN CASE OF ANY DISCREPANCY IN ARCHITECTURAL DRAWINGS, THE DRAWING SHALL BE CONSULTED BEFORE TAKING ANY ACTION AT SITE.

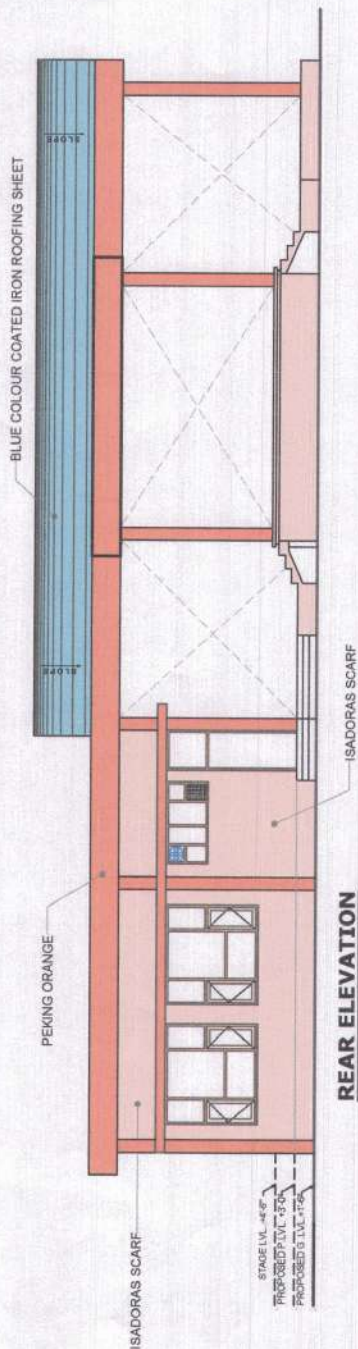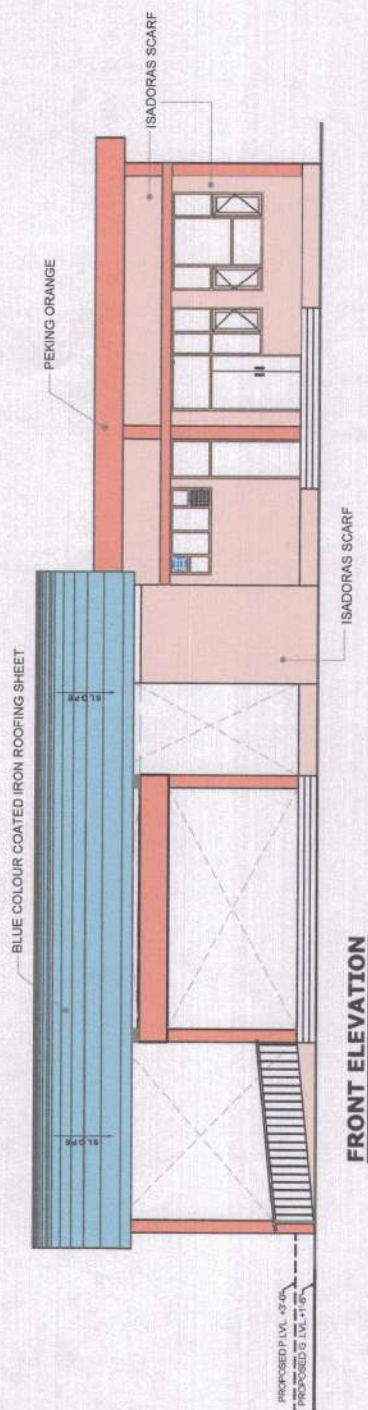

INTERNAL FINISH:-

- ALL INTERNAL WALLS OF ROOMS SHALL BE FINISHED WITH OIL BOUND DISTEMPER OF ARIZONA WHITE DULUX 42YY 87/084 (PAGE NO. 260).
- ALL CEILINGS SHALL BE FINISHED WITH WHITE COLOUR.

JOINERY:-

- ALL DOORS & WINDOWS FRAME, WINDOWS SHUTTER AND GRILL SHALL BE PAINTED WITH SYNTHETIC ENAMEL PAINT OF CHOCOLATE BROWN SHADE.
- WIRE MESH SHALL BE PAINTED IN SYNTHETIC ENAMEL PAINT OF ADMIRAL BLUE SHADE.
- ALL DOORS SHUTTER SHALL BE PAINTED WITH SYNTHETIC ENAMEL PAINT OF PARCHMENT DULUX 40YY 70/138 (PAGE NO.260).

COLOURS HAS BEEN TAKEN FROM DULUX SHADE CARD FOR REFERENCE ONLY

EXTERNAL FINISH:-

SHADE	DULUX PAINT
	PEKING ORANGE DULUX 60YR 24/439 (PAGE NO.72)
	ISADORAS SCARF DULUX 90YR 65/196 (PAGE NO. 71)

COLOURS HAS BEEN TAKEN FROM DULUX SHADE CARD FOR REFERENCE ONLY

ALL THE ABOVE SHADES HAVE BEEN TAKEN FROM THE FANDAK DULUX OF PAINTS/ASIAN PAINTS CATALOGUE FOR REFERENCE OF COLOUR/ SHADE ONLY. TYPE OF PAINTS & SPECIFICATIONS MAY BE ADOPTED AS PER PROVISIONS MADE IN DNIT/HARYANA PWD B & R SCHEDULE OF RATES.

AR. B.B. MEHTA
CHIEF ARCHITECT

AR. HITENDER SINGH
SENIOR ARCHITECT

AR. AMAN JAIN
ARCHITECT

AR. SUBHASH CHANDER
ASSIST. ARCHITECT
OFFICE OF THE CHIEF
ARCHITECT, HARYANA
CHANDIGARH

STD. PARK CUM
VYATAMSHALA

DEALT BY:
JOB NO.
2477

CHECKED BY:

SCALE:

DATE:
JULY 2022

COLOUR SCHEME