


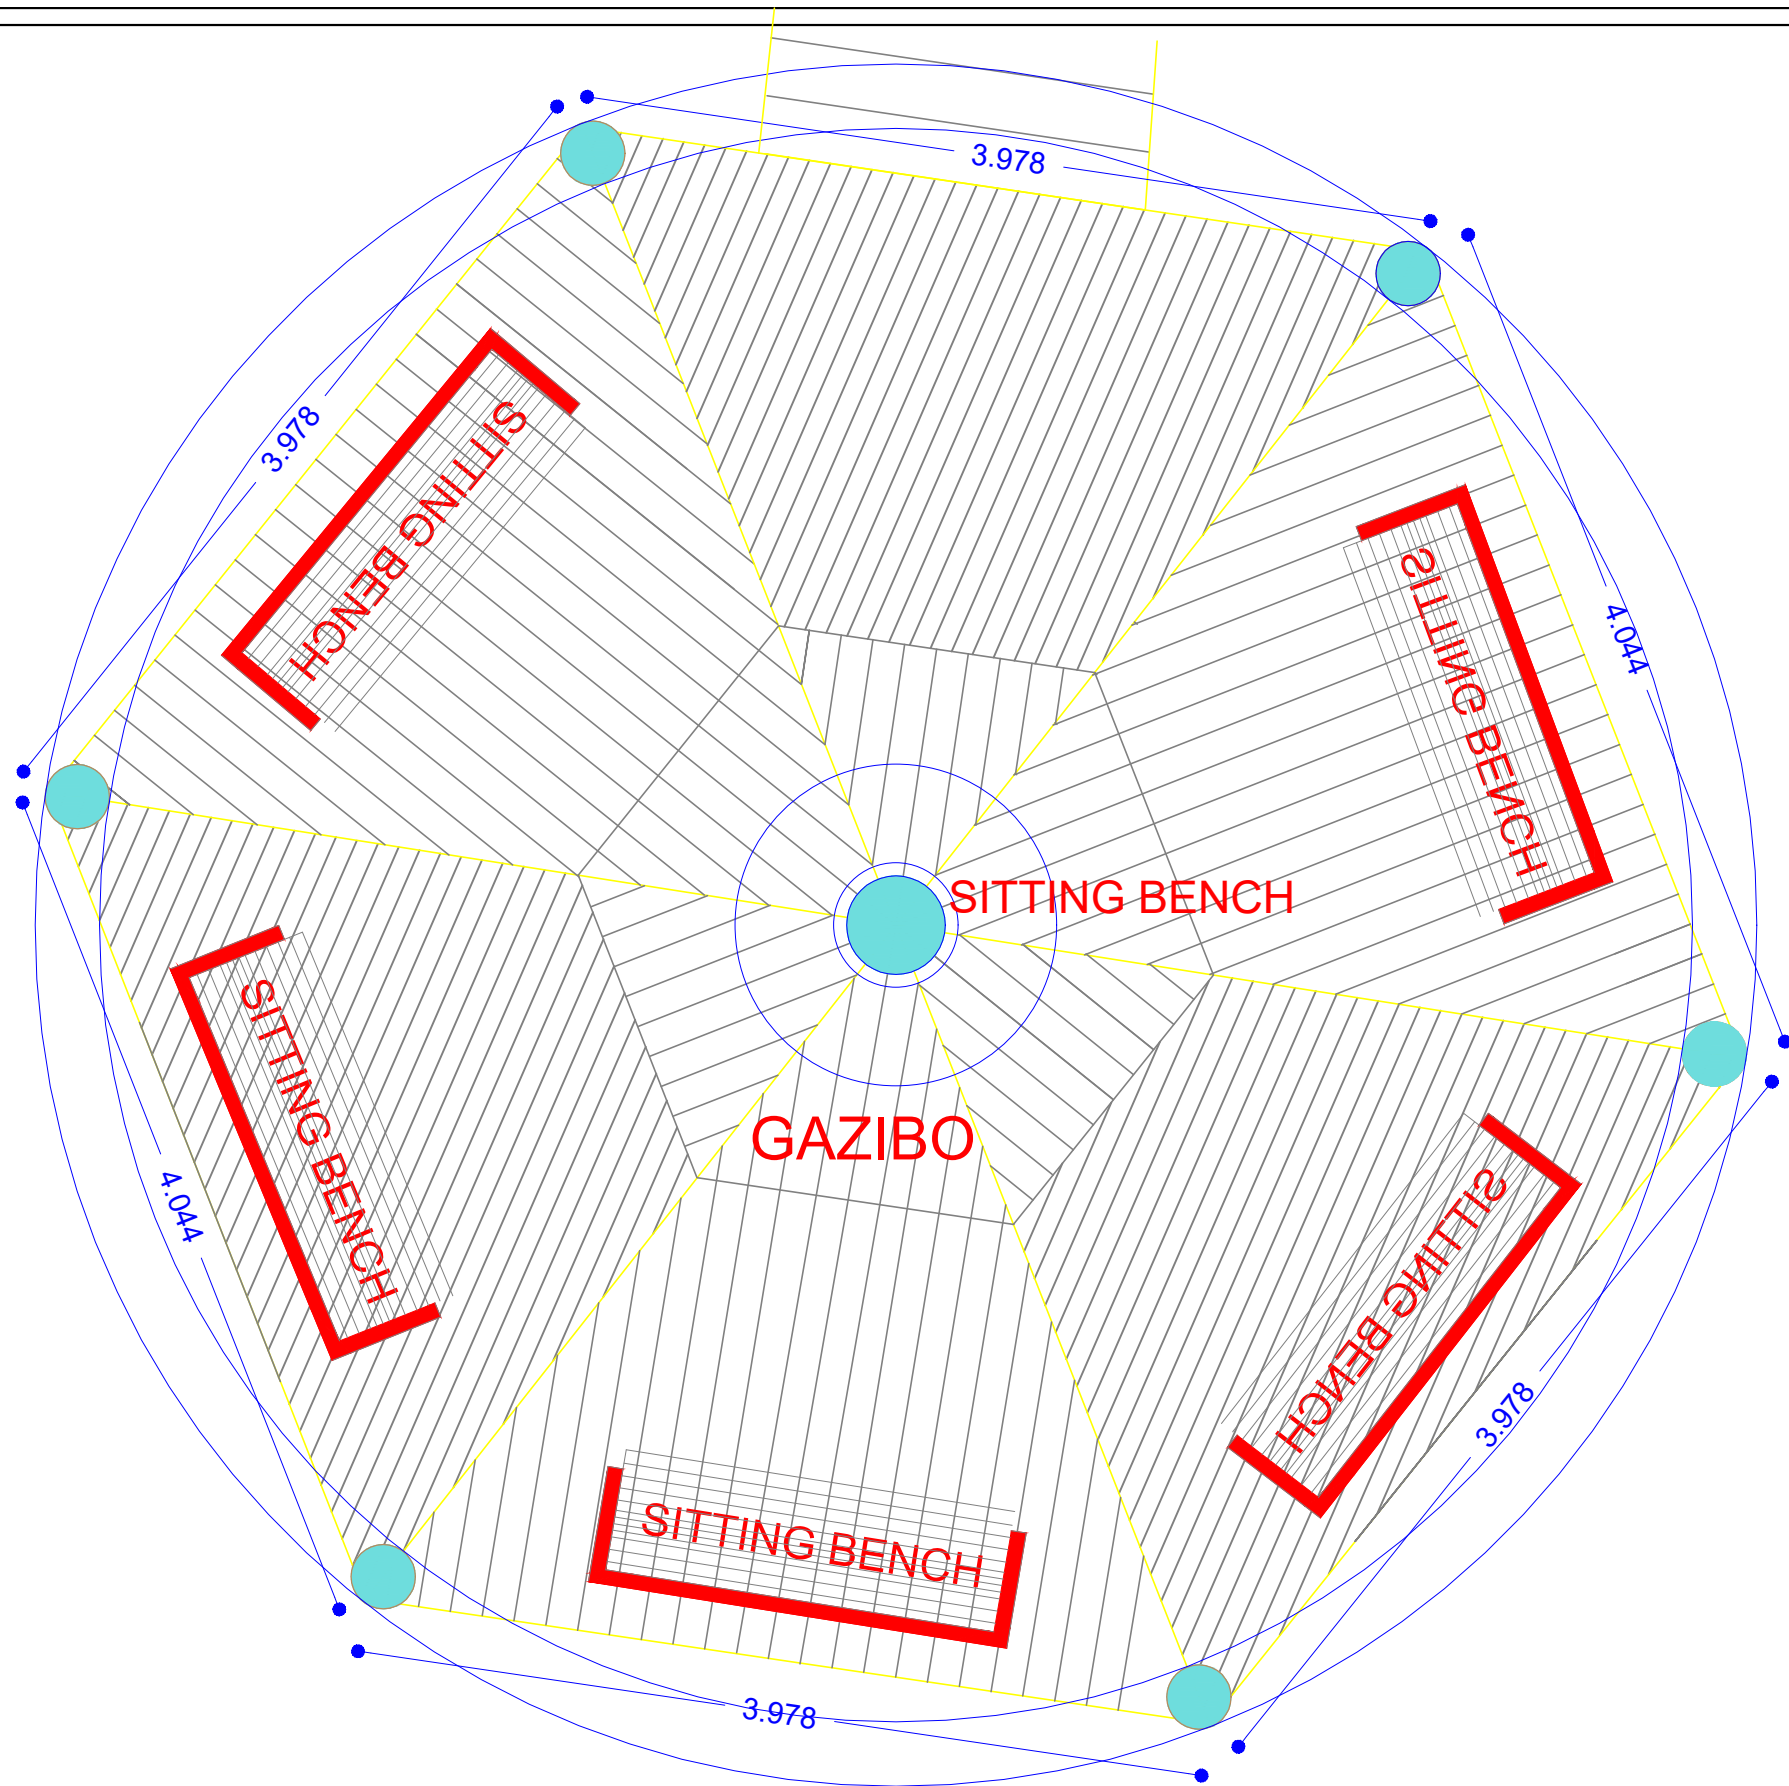

GAZIBO PLAN

PROJECT:-
CONSTRUCTION OF PARK HAMIDA
AT MC YAMUNANAGAR (HARYANA)

PURPOSE OF ISSUE:

ISSUED FOR
CONSTRUCTION

NORTH:

BUILDING NAME:

SHEET TITLE:

GAZIBO PLAN

STRUCTURE CON.


ARCHITECT:

 **CREATIVE DESIGN GROUP**
ARCHITECT . INTERIOR DESIGNER . PLANNING
A/c: KAVITA (B.Arch) 8901325494
A/c: RAVINDER 9416888498
Shop no. 110 ,Divine City Park-2,Behind Botton Gym,Near New bus stand, Kurukshetra

PROJECT No.		SHEET SIZE	A3
-------------	--	------------	----


ISSUE DATE		SCALE	NTS
------------	--	-------	-----

SHEET No.	GZ-AR-01	REV. No	0
-----------	----------	---------	---

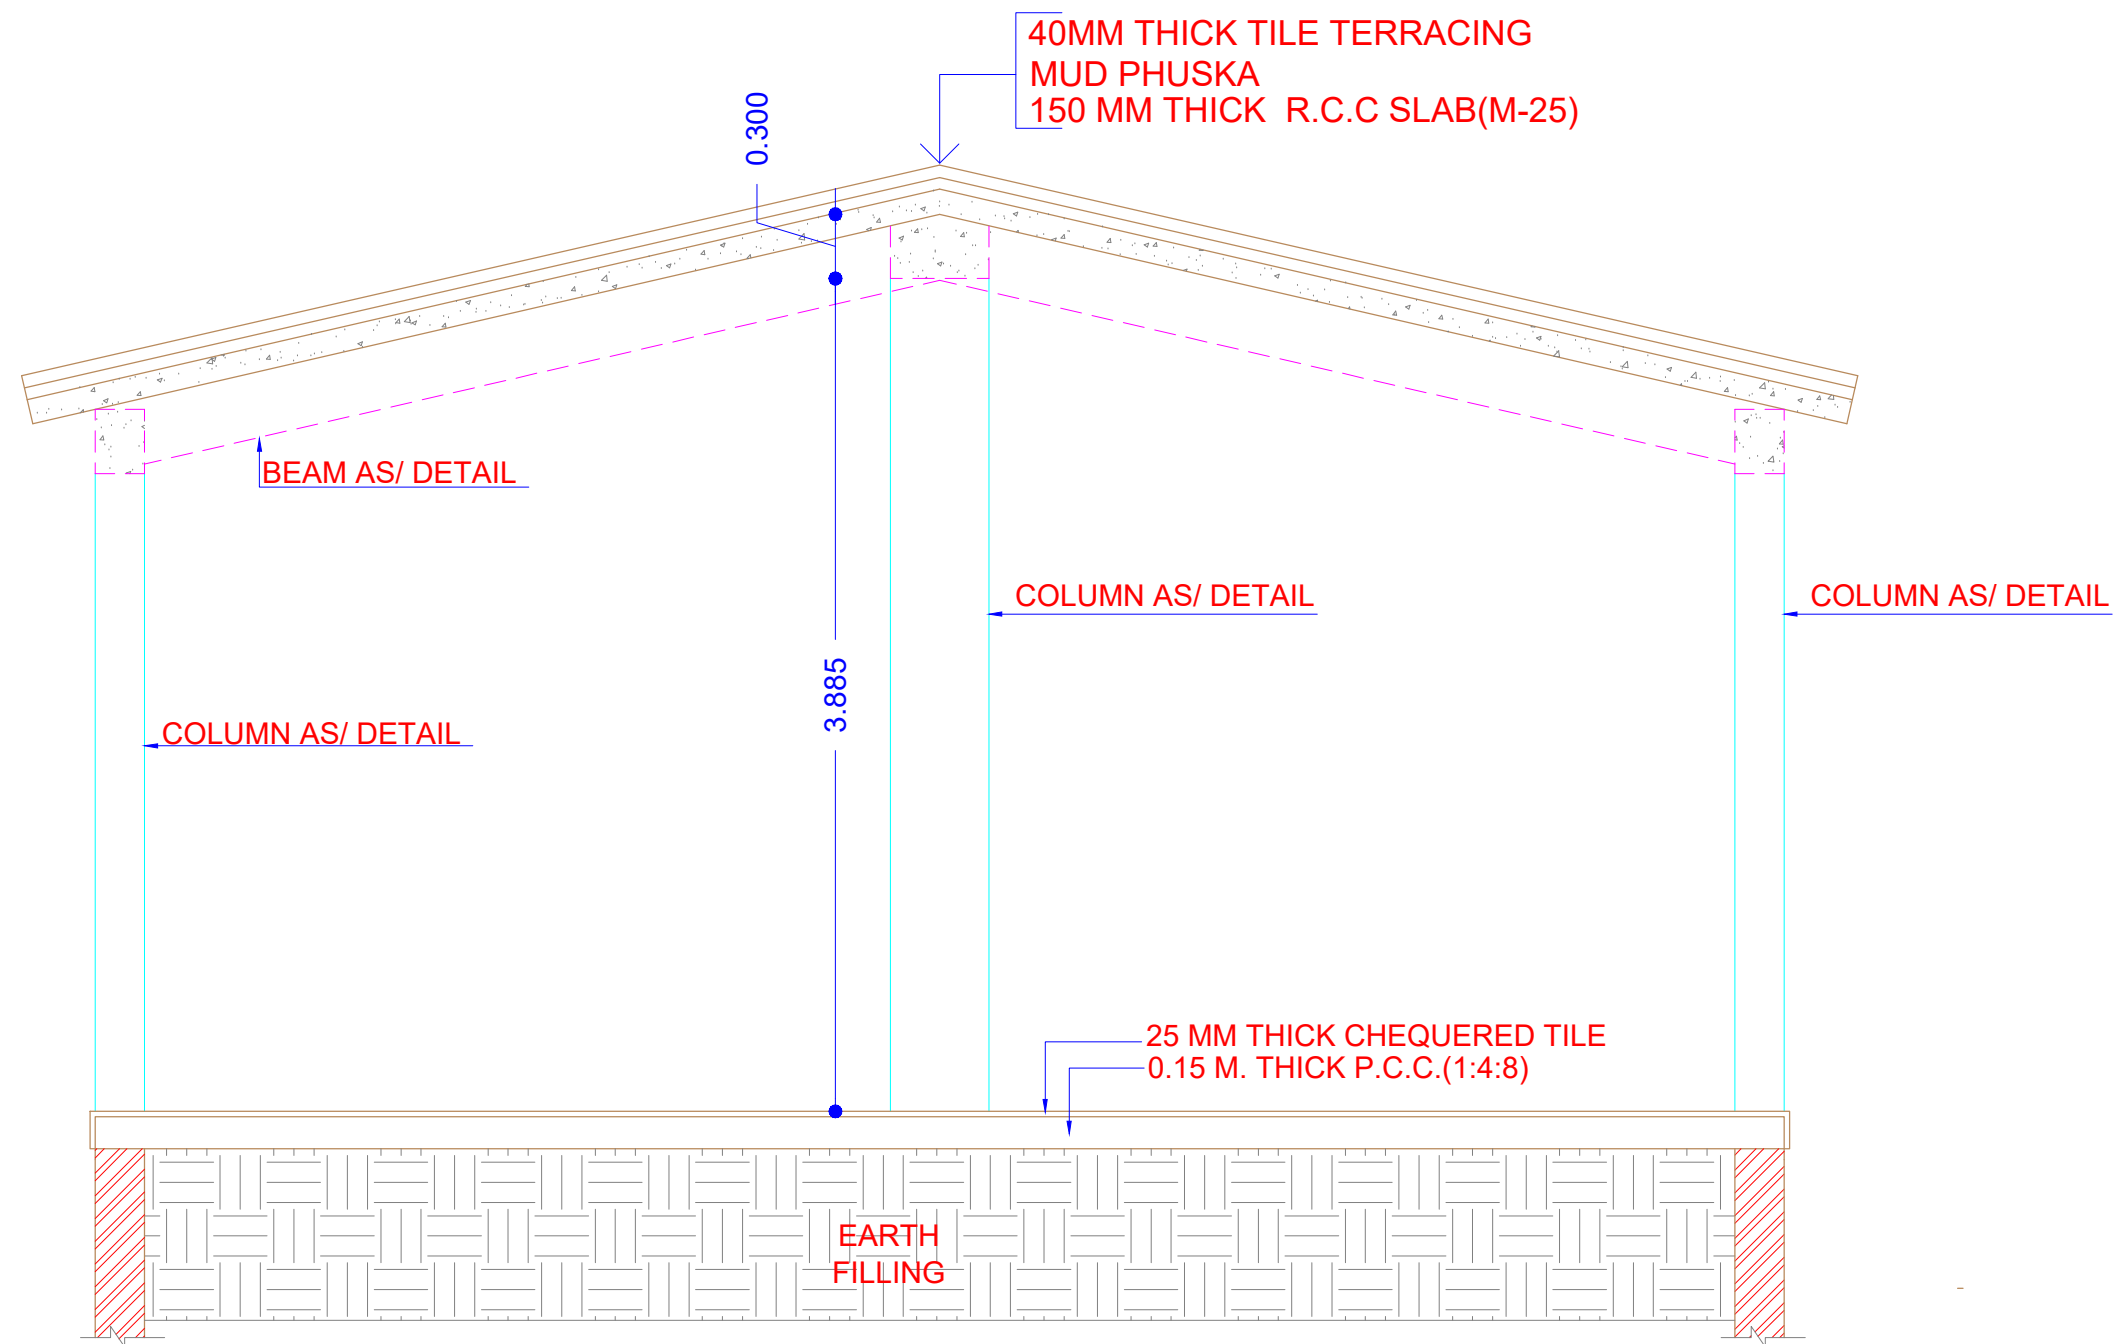


SECTION A-B

PROJECT:- CONSTRUCTION OF PARK HAMIDA AT MC YAMUNANAGAR (HARYANA)			
PURPOSE OF ISSUE: ISSUED FOR CONSTRUCTION			
NORTH:			
BUILDING NAME:			
SHEET TITLE: GAZIBO SECTION			
STRUCTURE CON.			
ARCHITECT: CREATIVE DESIGN GROUP ARCHITECT . INTERIOR DESIGNER . PLANNING Ar. KAVITA (B.Arch) 8901326494 Ar. RAVINDER 9416888498 Shop no. 110 ,Divine City Park-2,Behind Botton Gym,Near New bus stand, Kurukshetra			
PROJECT No.		SHEET SIZE	A3
ISSUE DATE		SCALE	NTS
SHEET No.	GZ-AR-02		REV. No.0

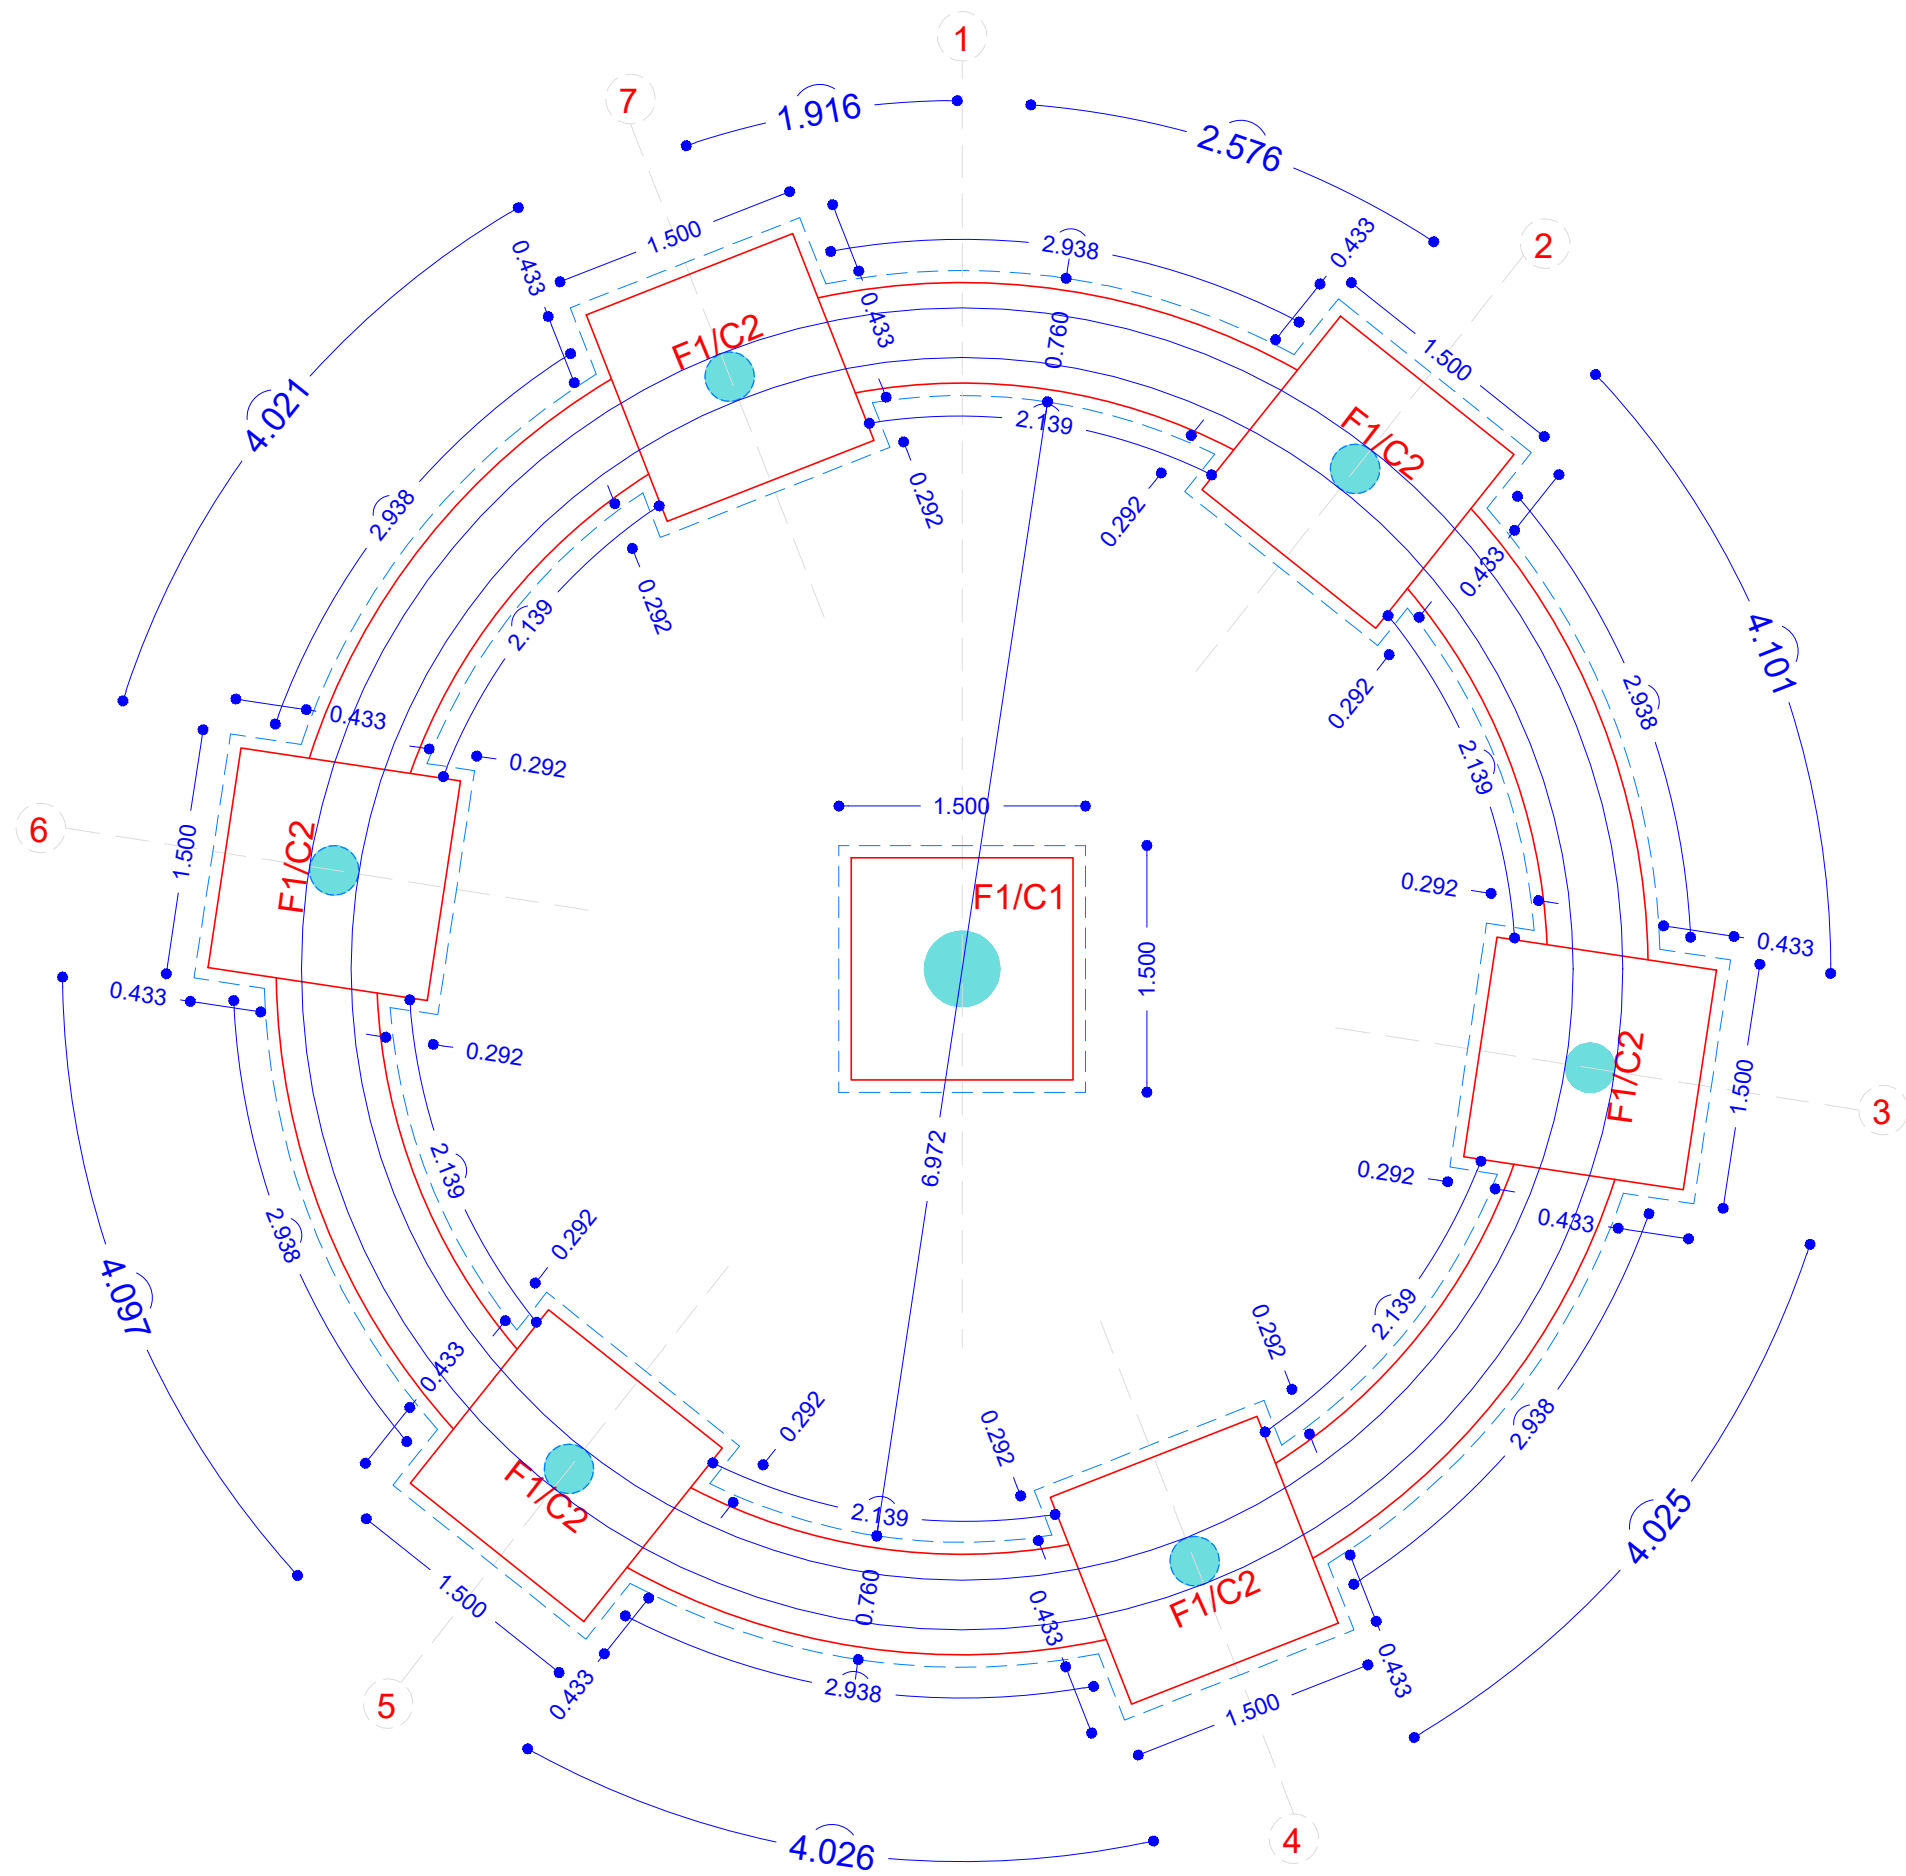

FOUNDATION LAYOUT PLAN

PROJECT:- CONSTRUCTION OF PARK HAMIDA AT MC YAMUNANAGAR (HARYANA)			
PURPOSE OF ISSUE: ISSUED FOR CONSTRUCTION			
NORTH:			
BUILDING NAME:			
SHEET TITLE: GAZIBO FOUNDATION LAYOUT PLAN			
STRUCTURE CON.			
ARCHITECT: CREATIVE DESIGN GROUP ARCHITECT · INTERIOR DESIGNER · PLANNING AR: KAVITA (B.Arch) 8801326484 AR: RAVINDEER 9416884699 Shop no. 110 ,Divine City Part-2,Behind Bostom Gyn,Near New bus stand, Kurukshetra			
PROJECT No.		SHEET SIZE	A3
ISSUE DATE		SCALE	NTS
SHEET No.	GZ-ST-01	REV. No	0

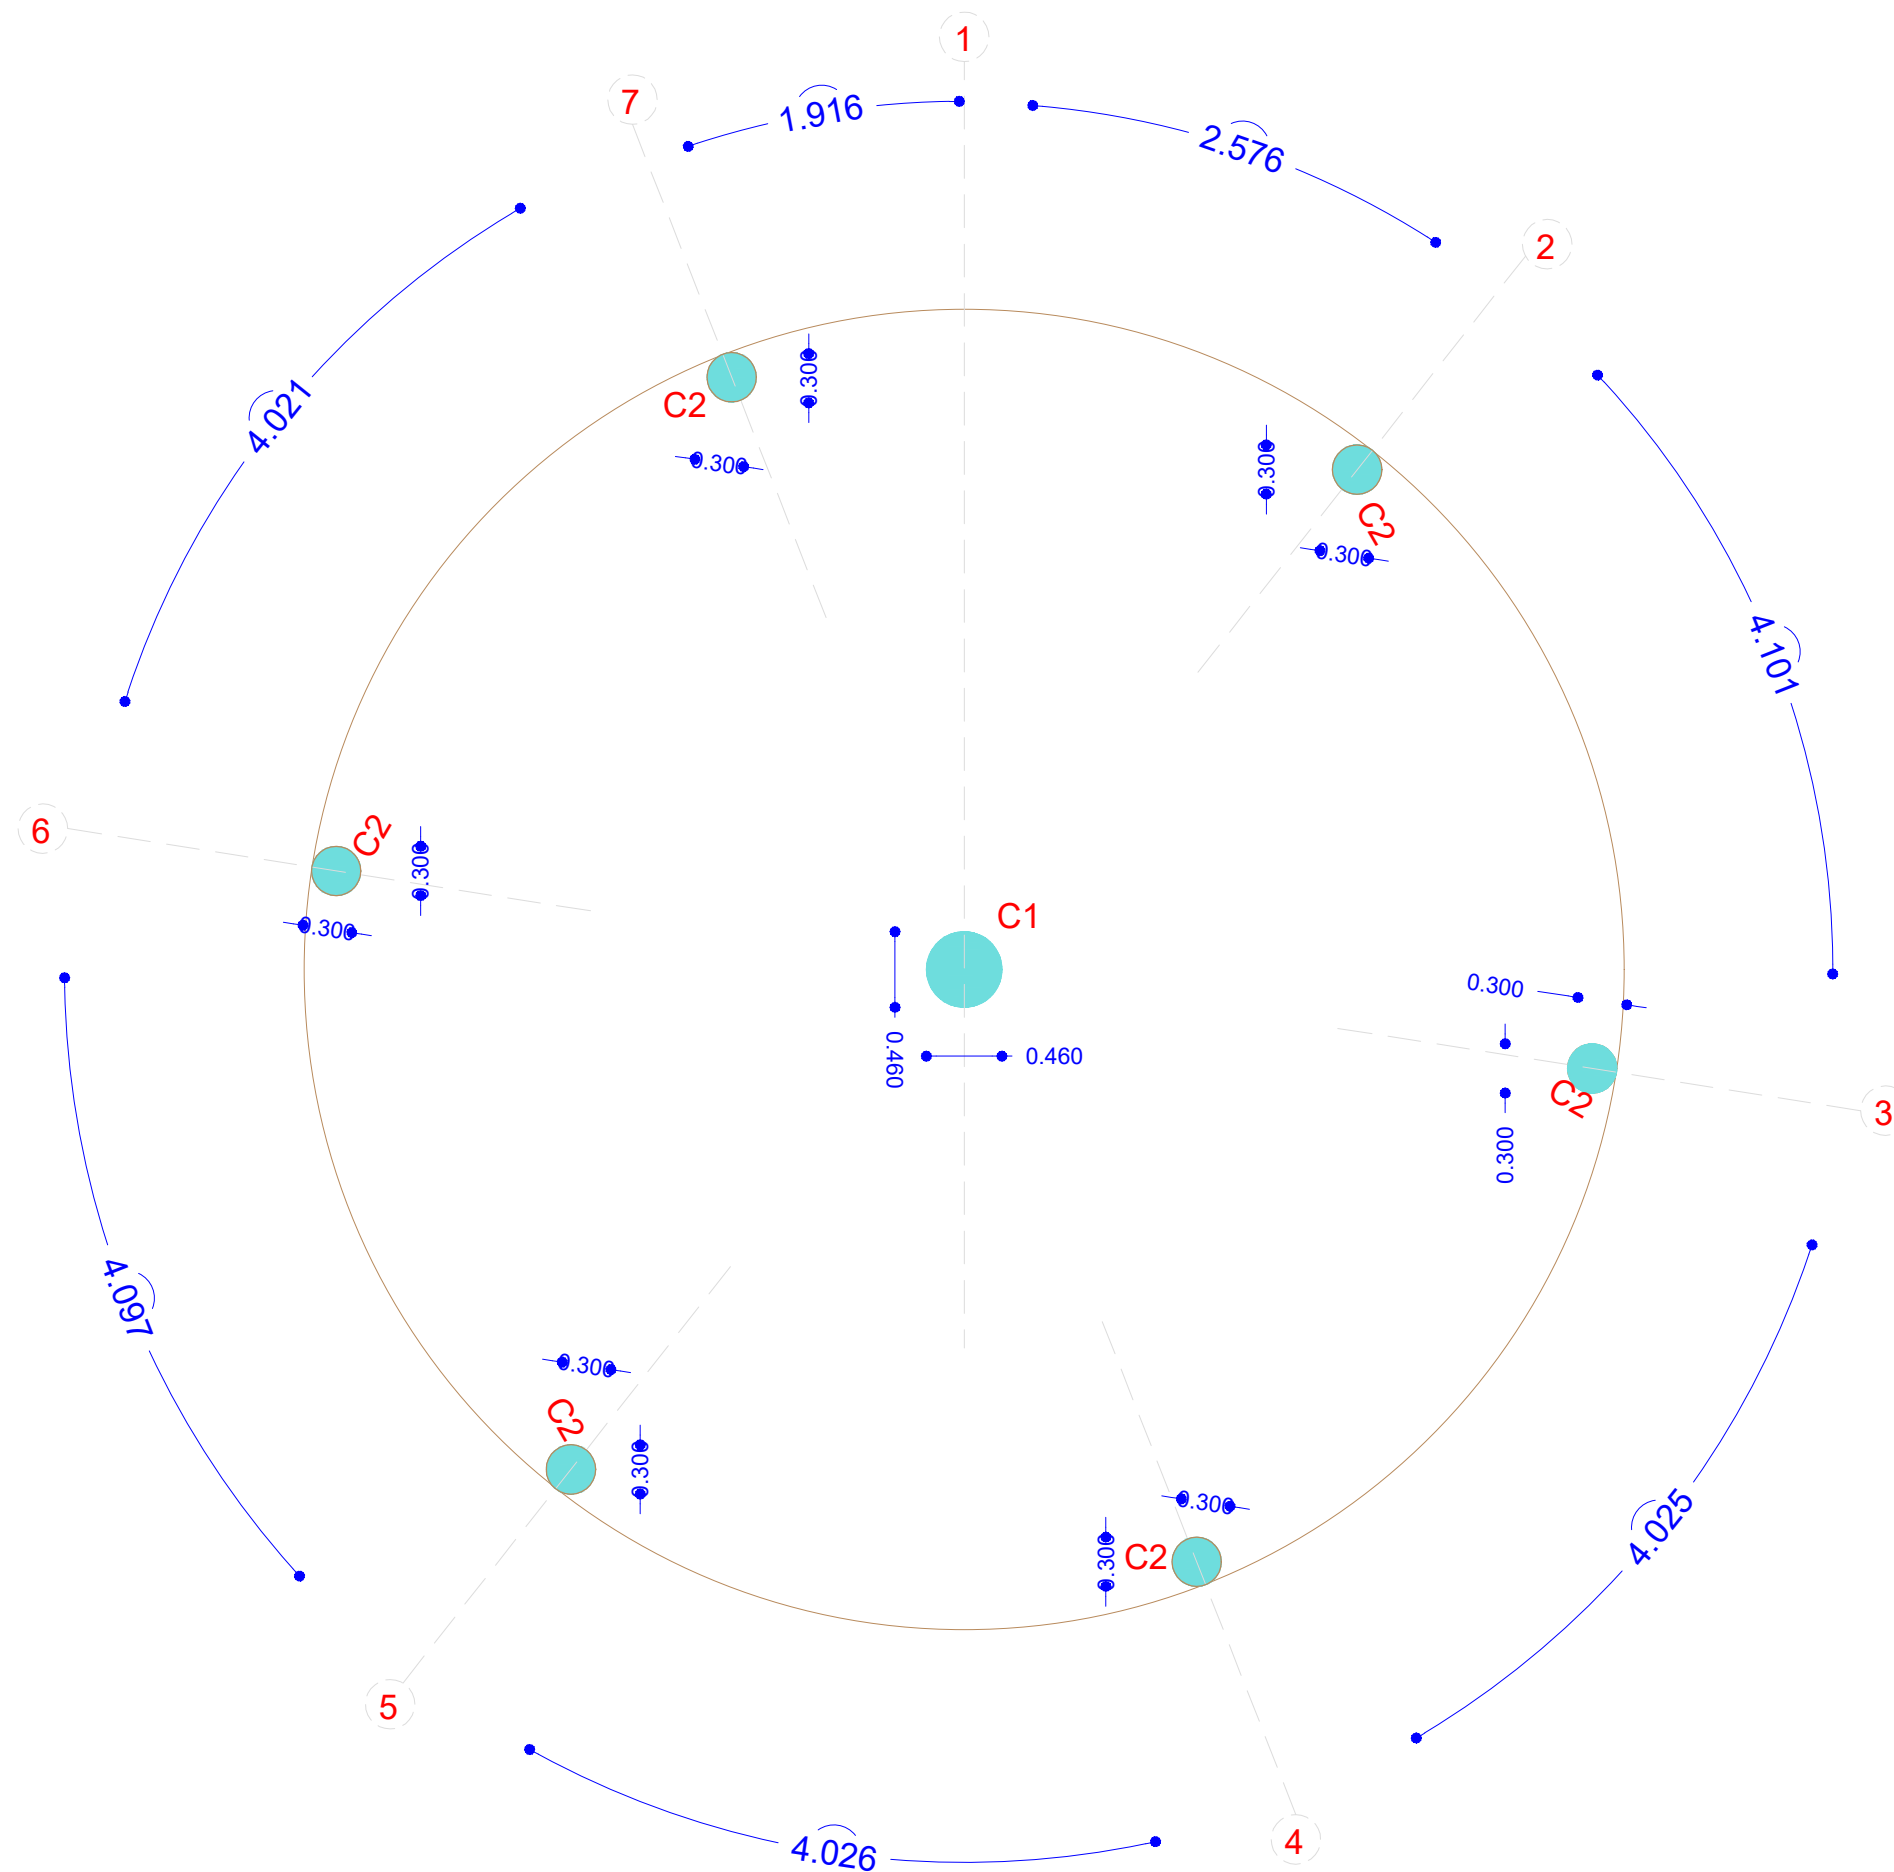

PROJECT:-

CONSTRUCTION OF PARK HAMIDA AT MC YAMUNANAGAR (HARYANA)

PURPOSE OF ISSUE:

**ISSUED FOR
CONSTRUCTION**

NORTH:

BUILDING NAME:

SHEET TITLE:

GAZIBO COLUMN AXIS LAYOUT PLAN

STRUCTURE CON.

ARCHITECT:


CREATIVE DESIGN GROUP
ARCHITECT . INTERIOR DESIGNER . PLANING
Ar. KAVITA (B.Arch) 8901326494
Ar. RAVINDER 9416889498
Top no. 110 ,Divine City Part-2,Behind Boston Gym,Near New bus stand, K...

Shop no. 110 ,Divine City Part-2,Behind Boston Gym,Near New bus stand, Kurukshetra

PROJECT No.	SHEET SIZE	A3
-------------	------------	----

ISSUE DATE	SCALE	NTS
------------	-------	-----

SHEET No.	GZ-ST-02	REV. No.0
-----------	----------	-----------

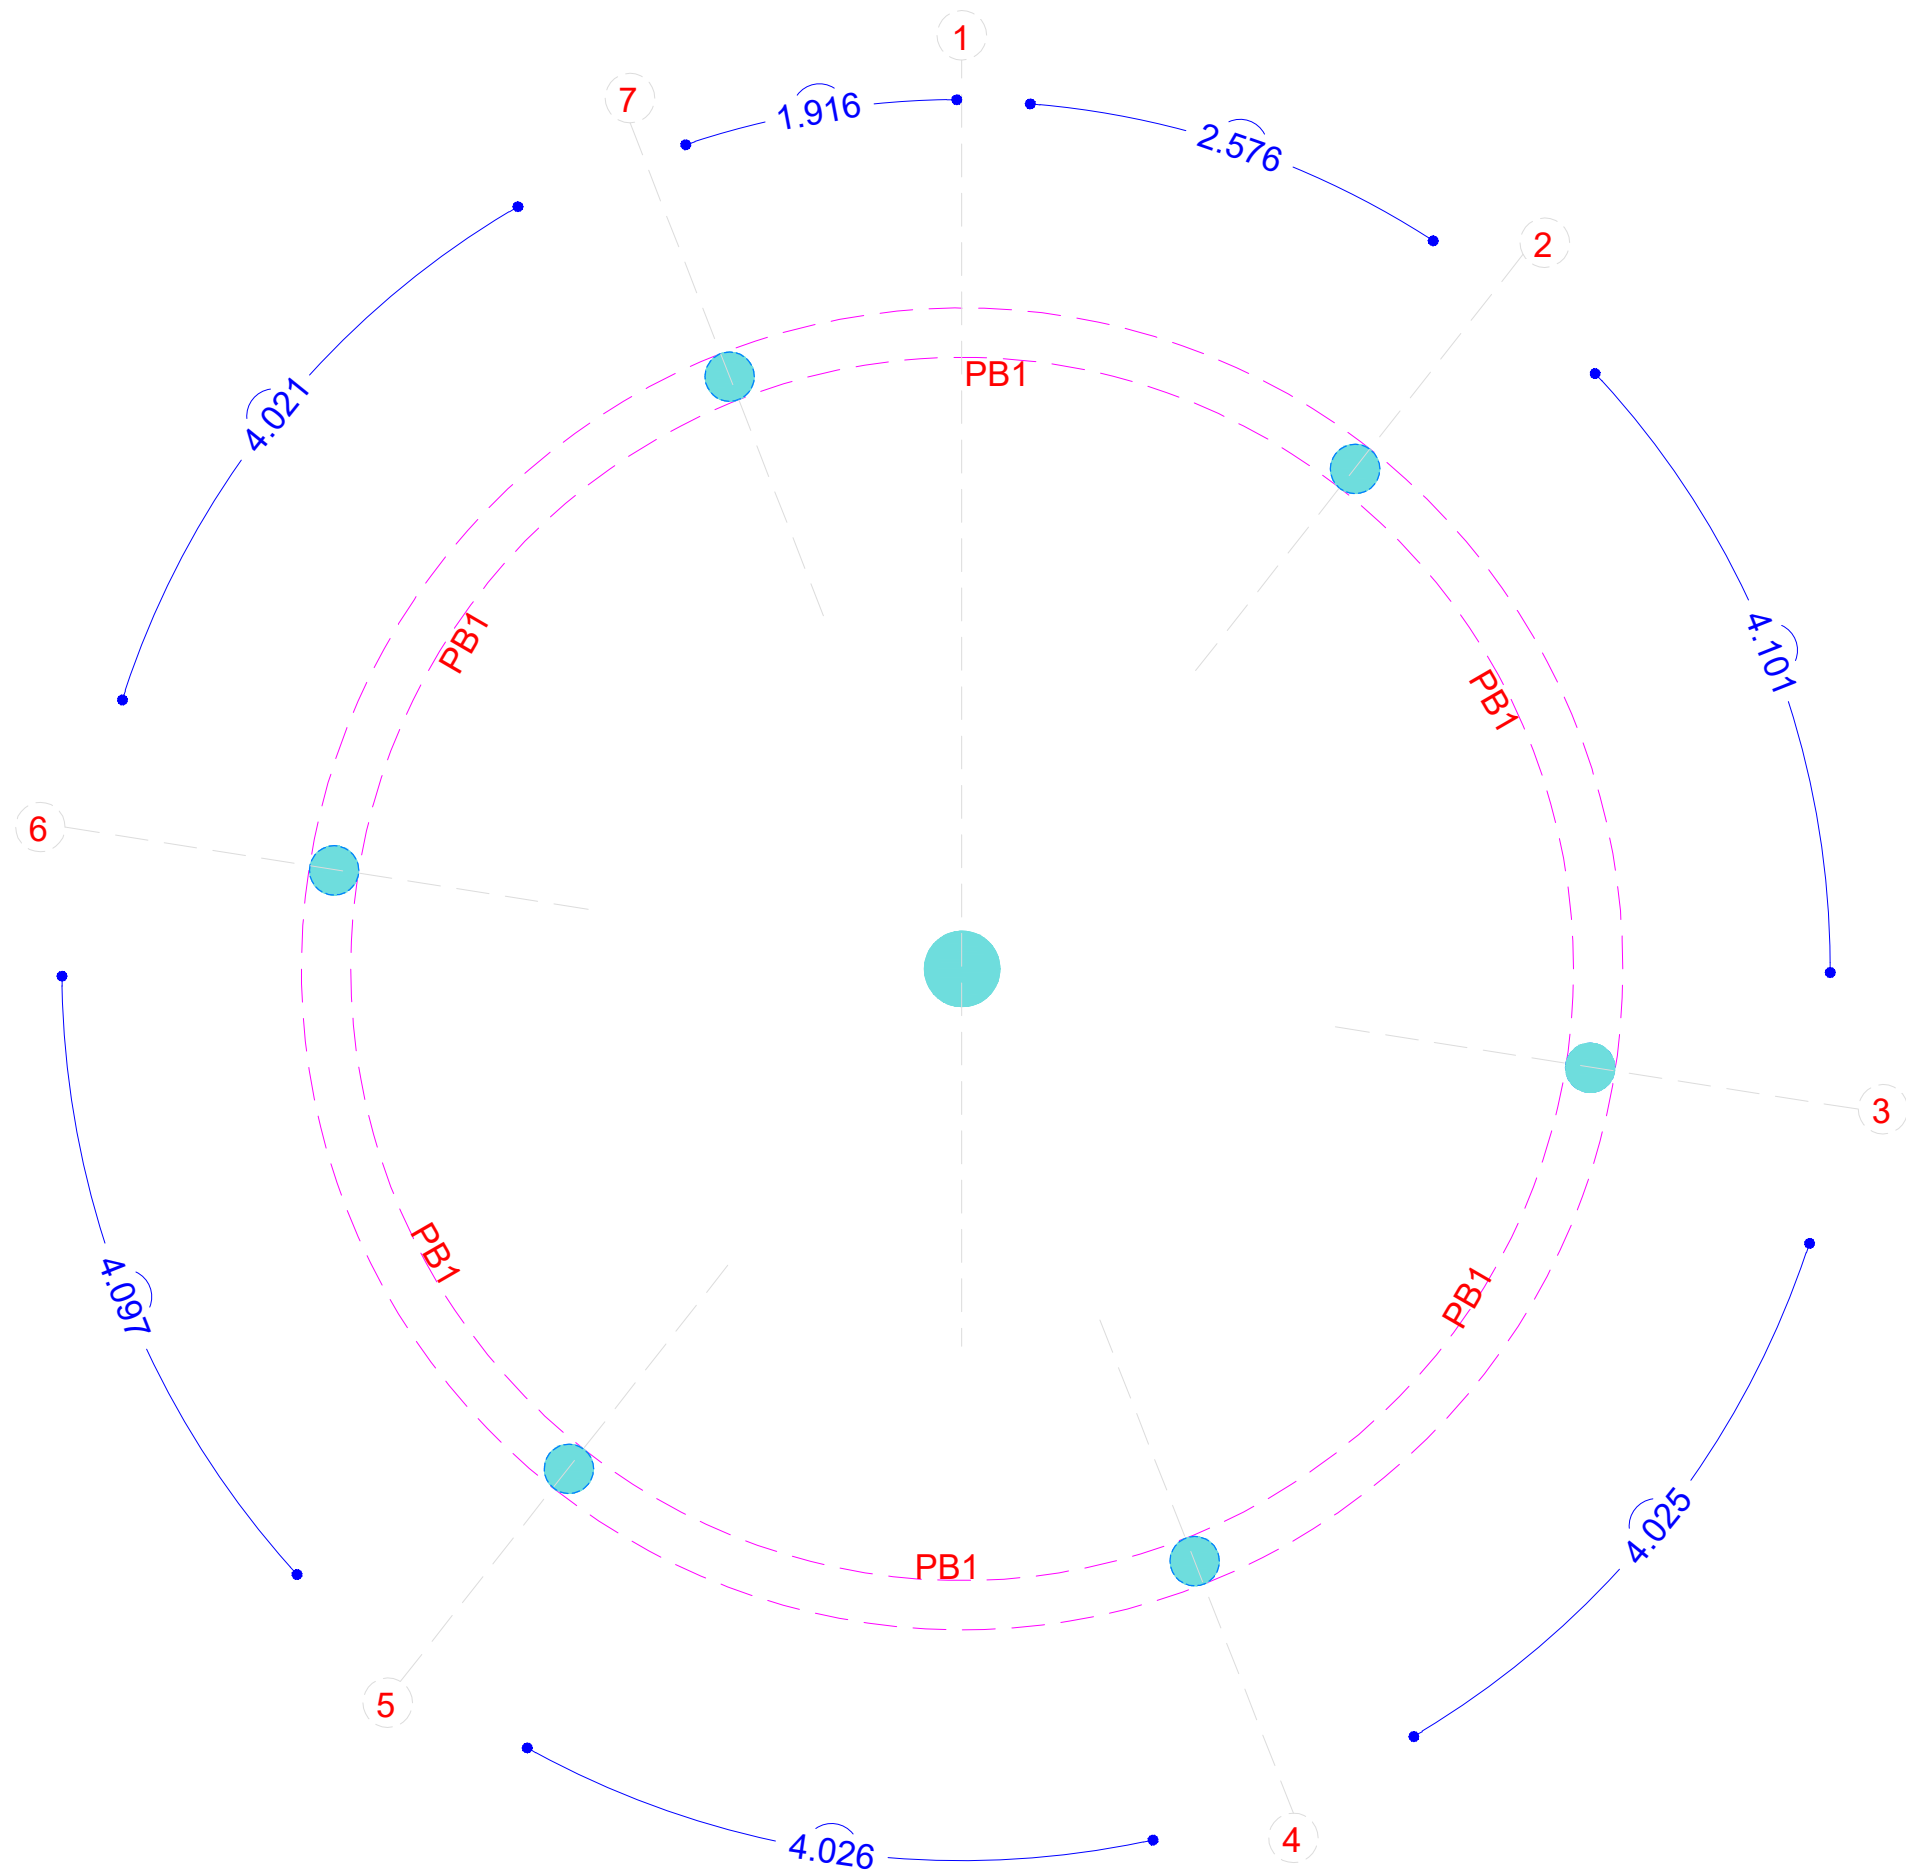

PROJECT:-

CONSTRUCTION OF PARK HAMIDA
AT MC YAMUNANAGAR (HARYANA)

PURPOSE OF ISSUE:

ISSUED FOR
CONSTRUCTION

NORTH:

BUILDING NAME:

SHEET TITLE:

GAZIBO PLINTH BEAM
LAYOUT PLAN

STRUCTURE CON.

ARCHITECT:

CDG

CREATIVE DESIGN GROUP


ARCHITECT . INTERIOR DESIGNER . PLANING

At: KAVITA (B.Arch) 8801326484

At: KAVINDER 9416884699



Shop no. 110 ,Divine City Part-2,Behind Boston Gyn,Near New bus stand, Kurukshetra

PROJECT No.		SHEET SIZE	A3
ISSUE DATE		SCALE	NTS
SHEET No.	GZ-ST-03		REV. No0

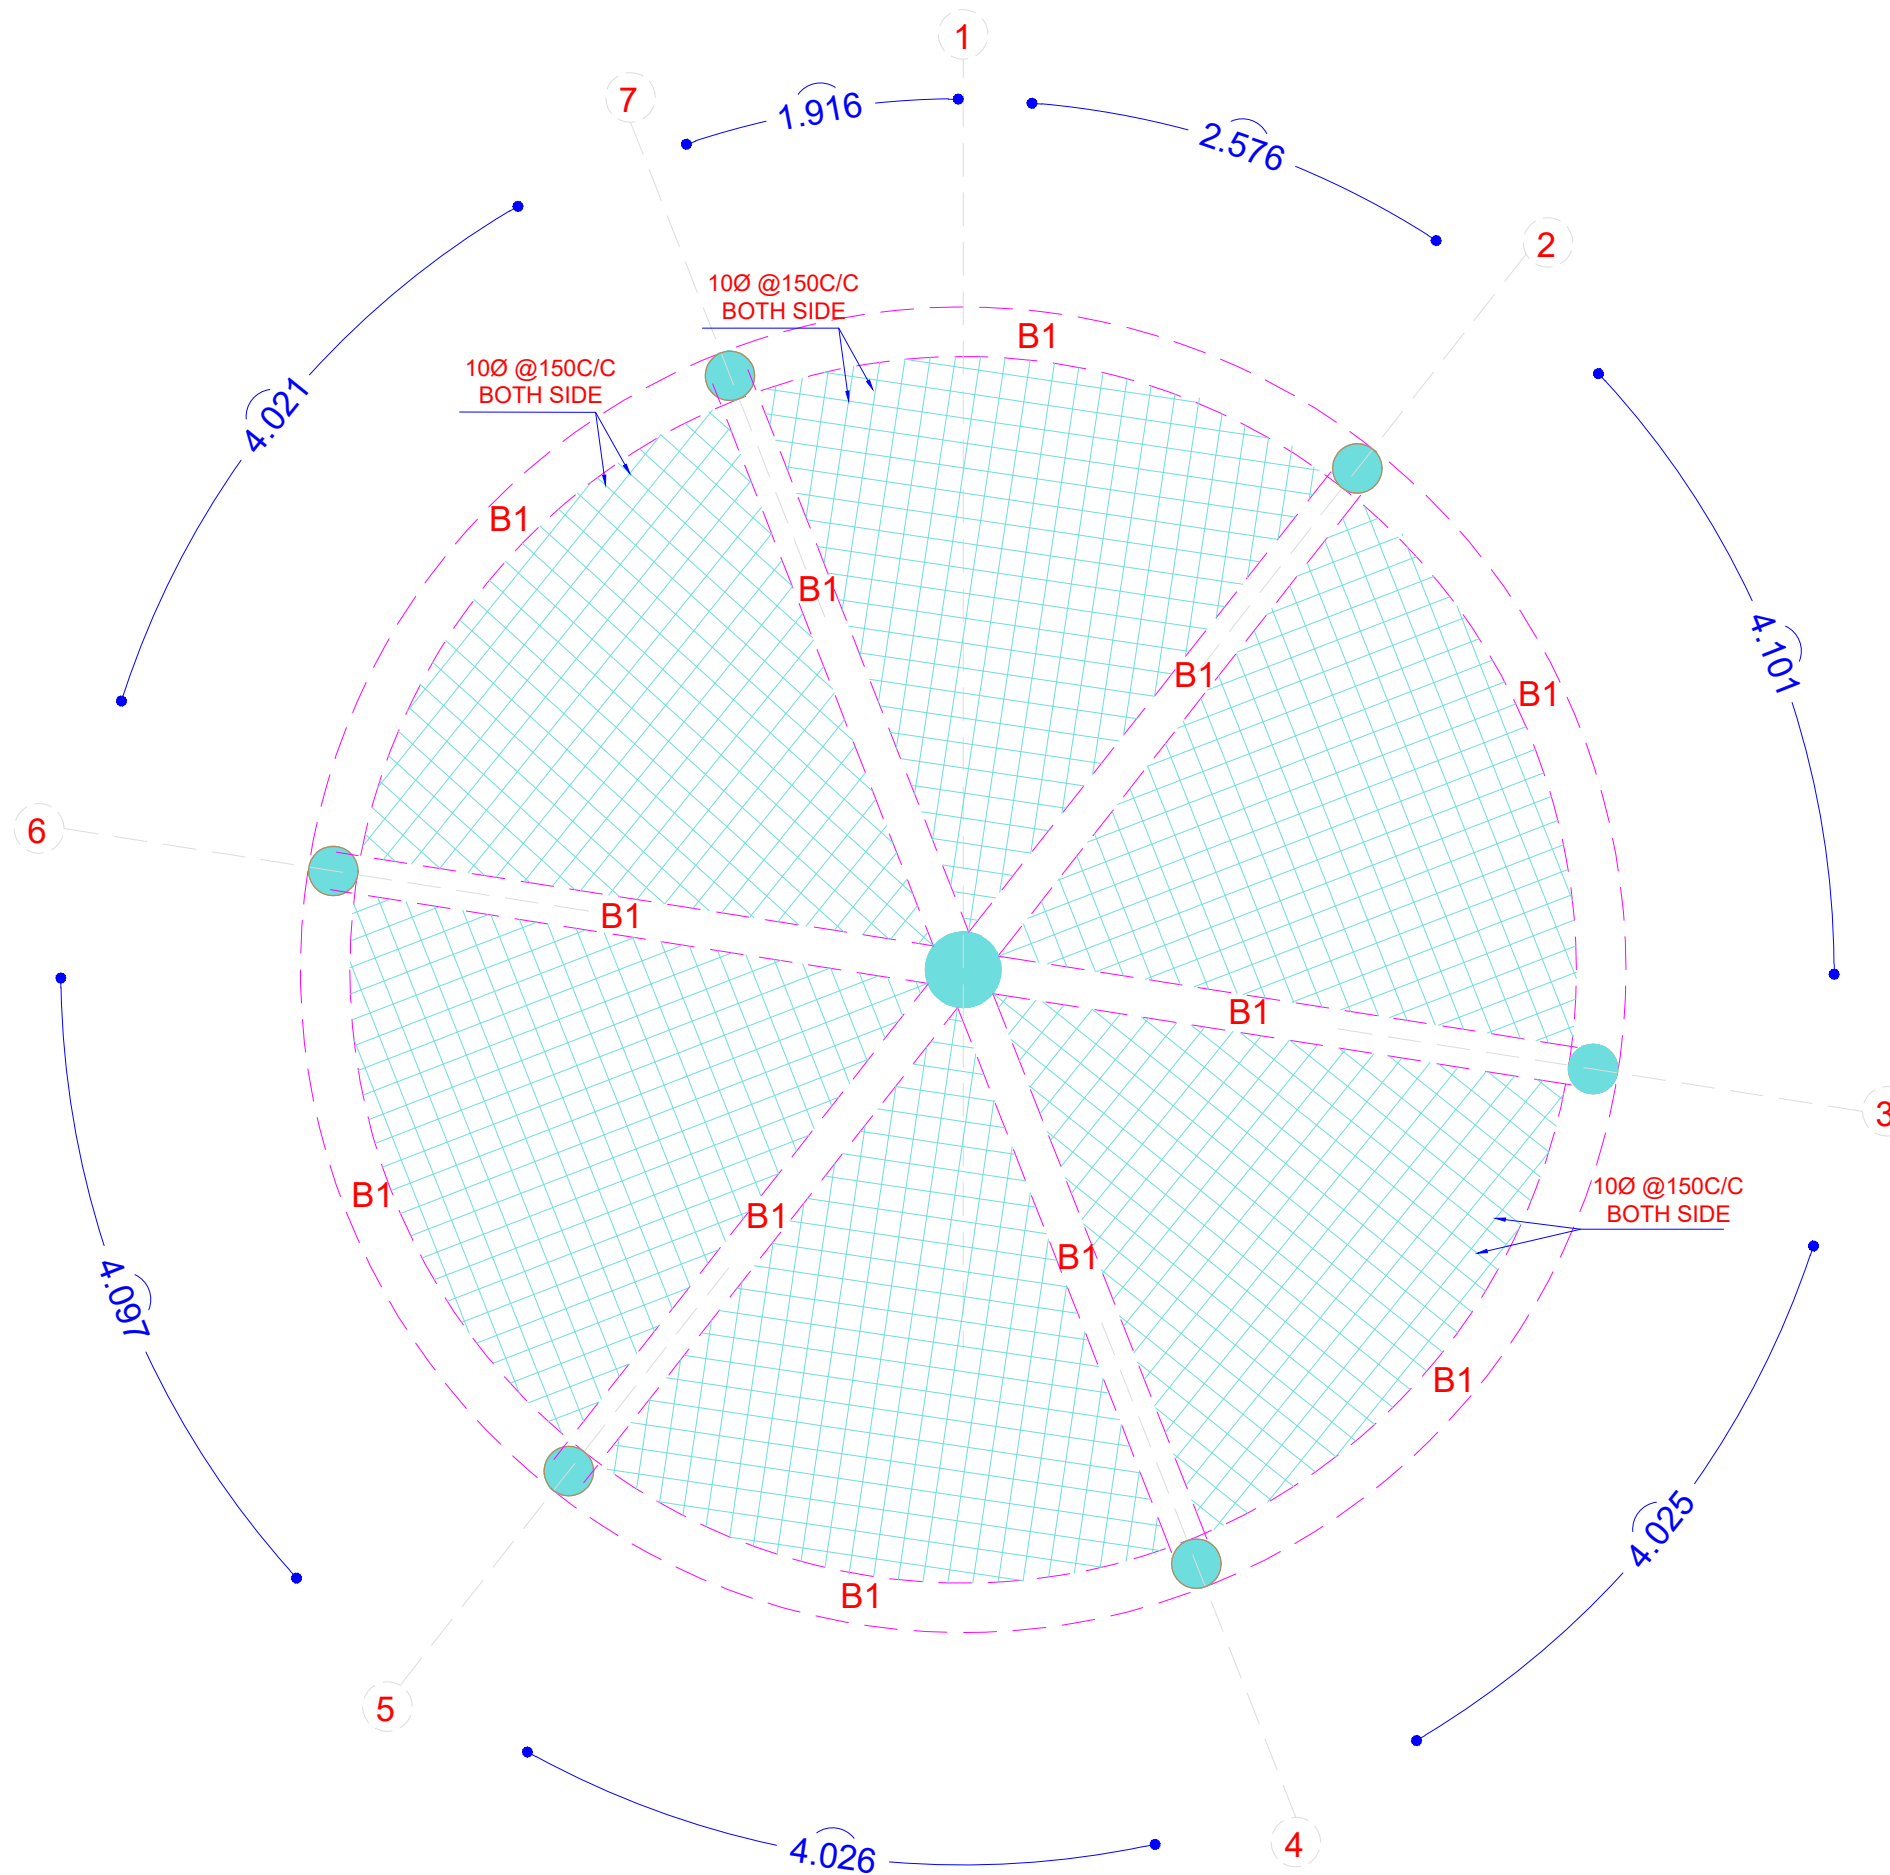






ROOF BEAM PLAN

PROJECT:-			
CONSTRUCTION OF PARK HAMIDA AT MC YAMUNANAGAR (HARYANA)			
PURPOSE OF ISSUE:			
ISSUED FOR CONSTRUCTION			
NORTH:			
BUILDING NAME:			
SHEET TITLE:			
GAZIBO ROOF BEAM LAYOUT PLAN			
STRUCTURE CON.			
ARCHITECT:			
CREATIVE DESIGN GROUP ARCHITECT . INTERIOR DESIGNER . PLANNING Ar. KAVITA (B.Arch) 8901326494 Ar. RAVINDER 9416888498 Shop no. 110 ,Divine City Park-2,Behind Botton Gym,Near New bus stand, Kurukshetra			
PROJECT No.		SHEET SIZE	A3
ISSUE DATE		SCALE	NTS
SHEET No.	GZ-ST-04		REV. No 0

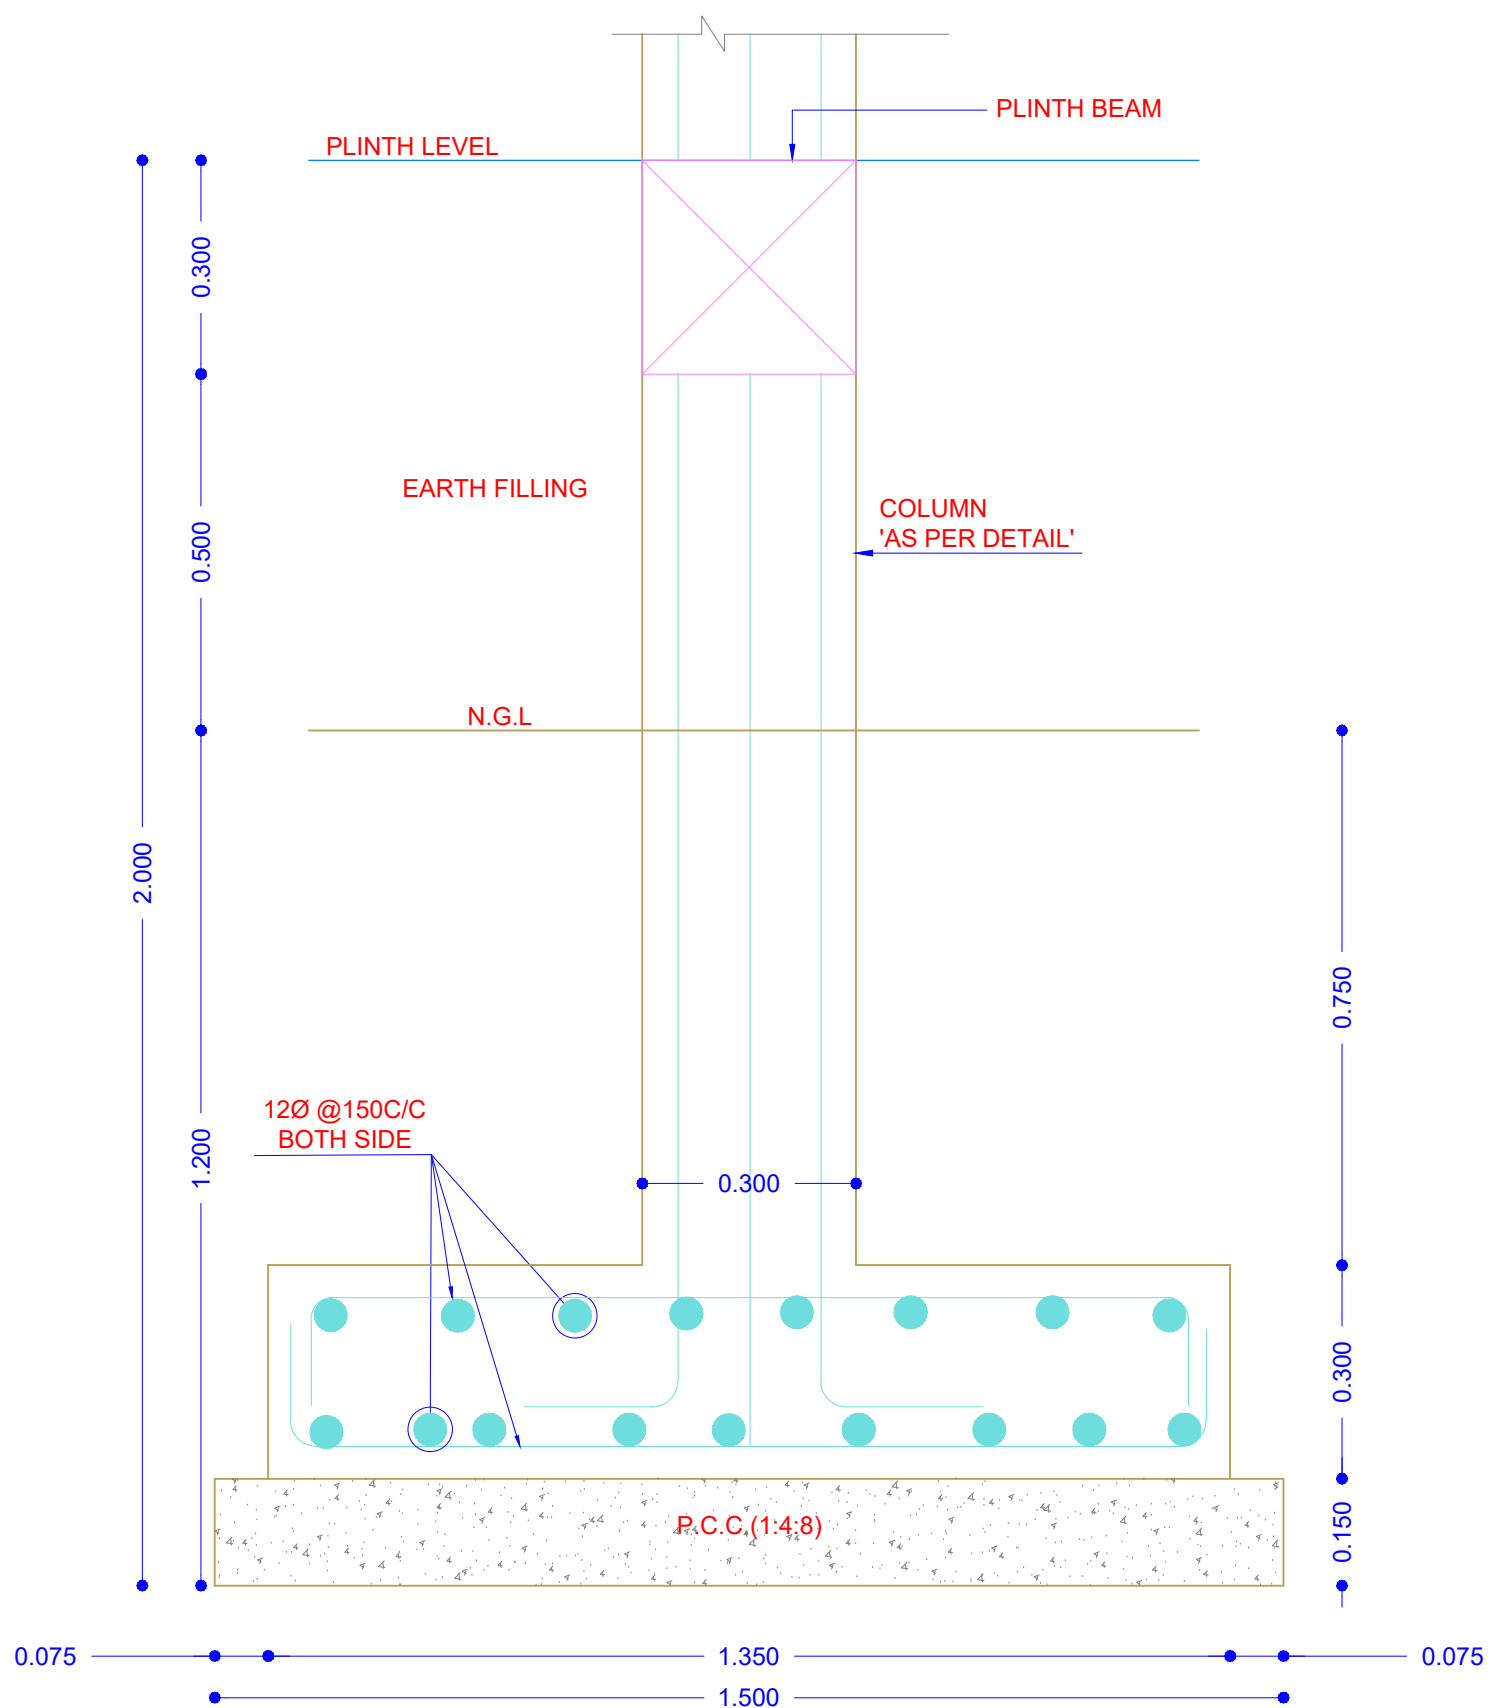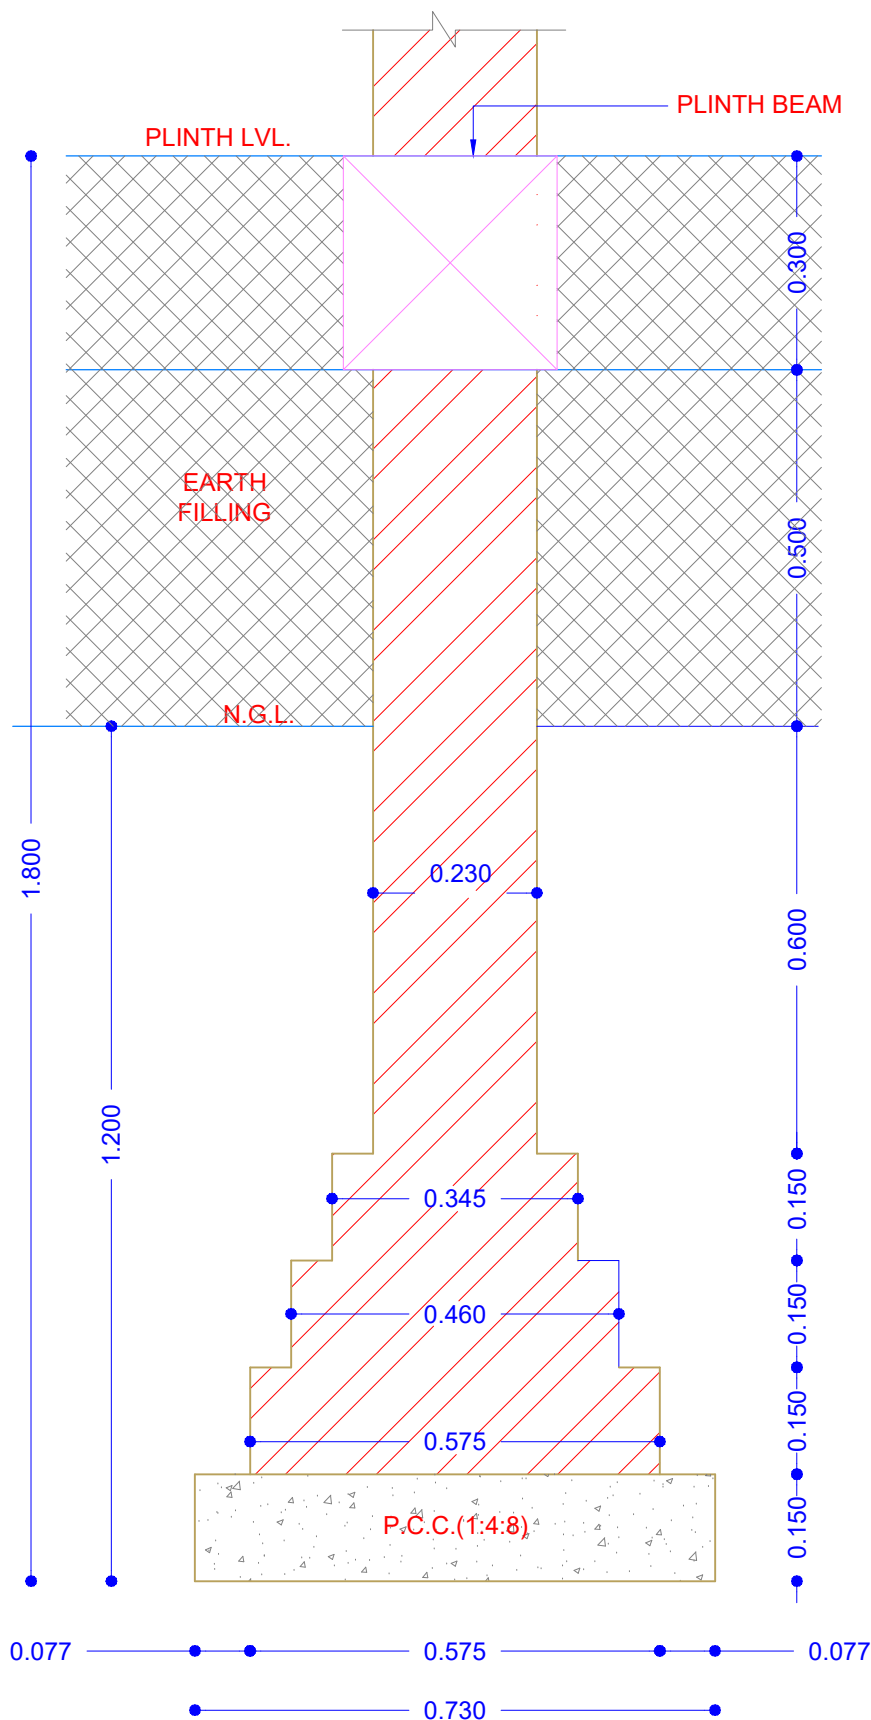

FOOTING DETAIL (F1)
1.500X1.500

PROJECT:- CONSTRUCTION OF PARK HAMIDA AT MC YAMUNANAGAR (HARYANA)			
PURPOSE OF ISSUE: ISSUED FOR CONSTRUCTION			
NORTH:			
BUILDING NAME:			
SHEET TITLE: GAZIBO FOUNDATION DETAIL			
STRUCTURE CON.			
ARCHITECT:			
 CREATIVE DESIGN GROUP ARCHITECT . INTERIOR DESIGNER . PLANING Ar. KAVITA (B.Arch) 8901326494 Ar. RAVINDER 9416889498 Shop no. 110 ,Divine City Part-2,Behind Boston Gym,Near New bus stand, Kurukshetra			
PROJECT No.		SHEET SIZE	A3
ISSUE DATE		SCALE	NTS
SHEET No.	AV-ST-05	REV. No.	0

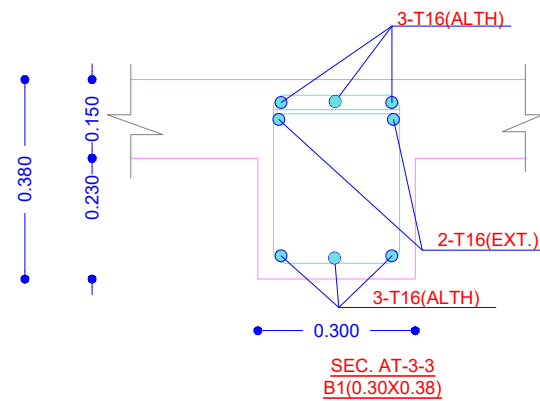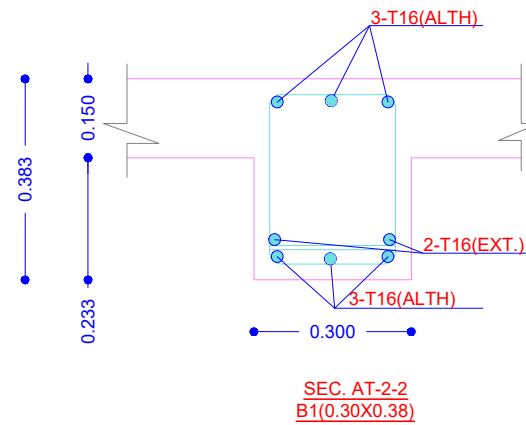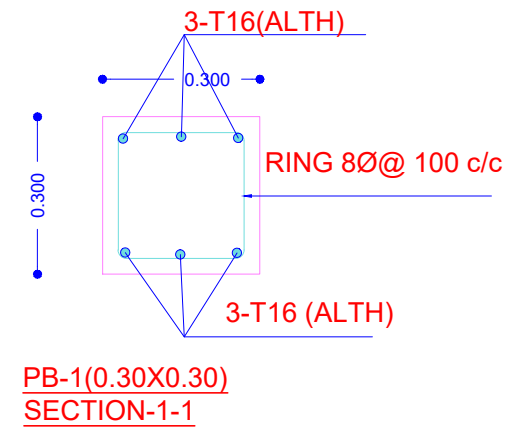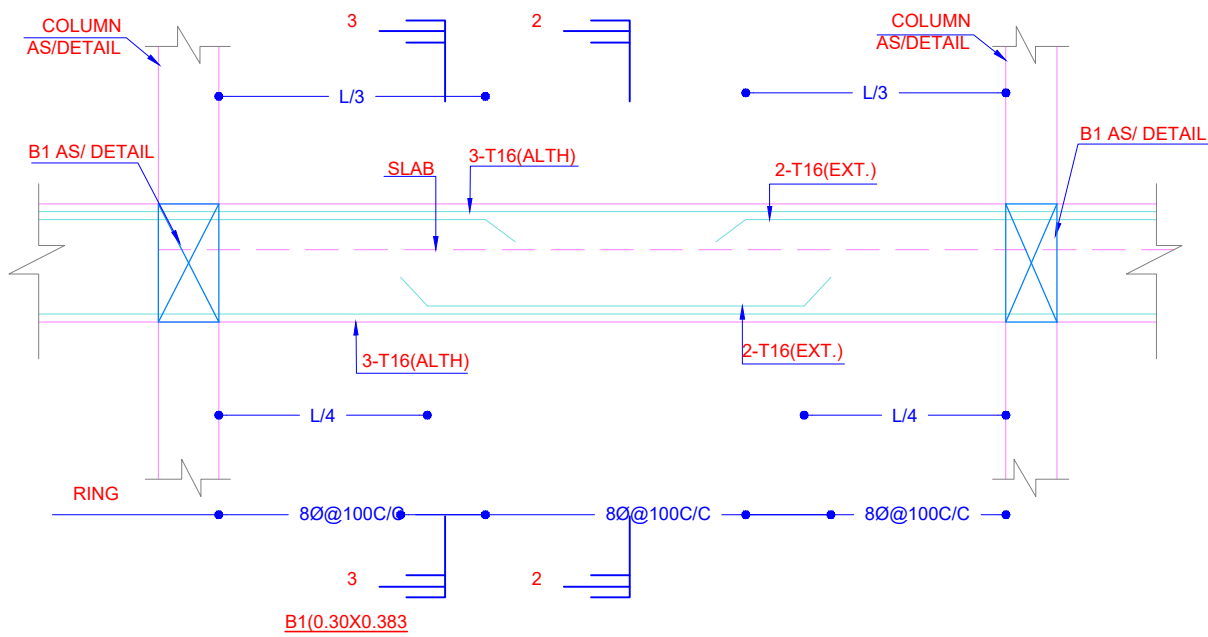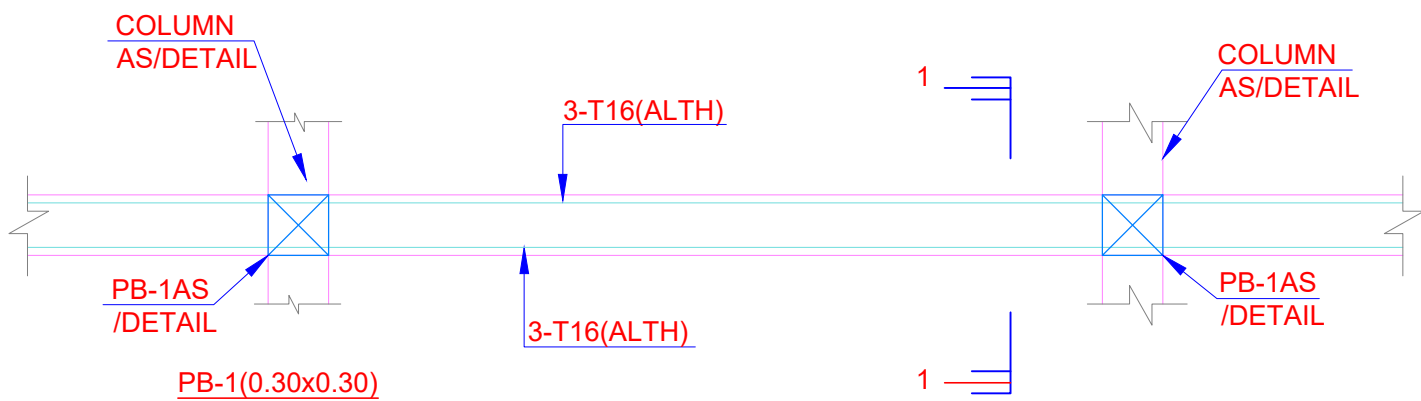

FLOOR LEVEL	COLUMN C-1		
	SIZE & SHAPE 0.46 Ø	REINFORCEMENT	
		VERT ST.:- 16 mm dia 12 nos. 1 to 12 TIES:- 8mm dia @200mm C/C	1 SETS

FLOOR LEVEL	COLUMN C-2		
	SIZE & SHAPE 0.300X0.300	REINFORCMENT	RING SET
FOUNDATION TO GROUND FLOOR		VERT ST.:- 16mm dia 6 nos TIES:- 8mm @150 C/C	1 SET

PROJECT:-
CONSTRUCTION OF PARK HAMIDA
AT MC YAMUNANAGAR (HARYANA)

PURPOSE OF ISSUE:

ISSUED FOR
CONSTRUCTION

NORTH:

BUILDING NAME:

SHEET TITLE:

GAZIBO PLINTH BEAM,
ROOF BEAM,&
COLUMN DETAIL

STRUCTURE CON.

ARCHITECT:

CREATIVE DESIGN GROUP
ARCHITECT . INTERIOR DESIGNER . PLANING
Ar. KAVITA (B.Arch) 8901326494
Ar. RAVINDER 9416889498

Shop no. 110 ,Divine City Part-2,Behind Boston Gym,Near New bus stand, Kurukshetra

PROJECT No. SHEET SIZE A3

ISSUE DATE SCALE NTS

SHEET No. AV-ST-06 REV. No. 0