

GENERAL NOTES:-

- THIS DRAWING IS THE PROPERTY OF THE DEPARTMENT OF ARCHITECTURE, GOVT. OF HARYANA. THIS DRAWING MAY NOT BE ALTERED, COPIED, USED IN WHOLE OR IN PART WITHOUT THE PERMISSION OF THIS DEPARTMENT IN WRITING.
- THE DISCREPANCY, IF ANY MUST BE BROUGHT TO THE NOTICE OF THE DEPARTMENT OF ARCHITECTURE HARYANA BEFORE ANY ACTION AT SITE.
- REVISED SPECIFICATIONS APPROVED BY THE ECONOMY COMMITTEE FOR P.H.C. / C.H.C. SHALL BE FOLLOWED.
- JOINERY MAY BE FABRICATED AFTER CONFIRMING THE SIZE OF PHYSICAL OPENING AT SITE.
- STANDARD SIZE OF PRESSED STEEL FRAME HAS BEEN MENTIONED IN THE DRAWINGS THESE SHALL BE AS PER APPROVED DNIT.

SPECIFICATION:-

- ALL DOOR AND WINDOW & VENTILATORS SHALL HAVE PRESSED STEEL FRAMES WITH STANDARD STEEL SECTIONS AS PER DETAILED DRAWINGS.
- SHUTTERS FOR ALL DOORS SHALL BE FLUSH SHUTTERS ISI MARKED.
- MS GRILL SHALL BE PROVIDED IN ALL EXTERNAL WINDOWS & VENTILATORS.
- EXHAUST FANS SHALL BE PROVIDED IN ALL TOILETS.
- OPENINGS FOR AIR CONDITIONER / DESERT COOLER SHALL BE KEPT EXACT AT SITE IN CONSULTATION WITH CONCERNED XEN, ELECT. DIVN. P.W.D.(B&R) BR.
- ENTRY DOORS SHALL HAVE FLUSH & WIREMESH SHUTTERS BOTH.

AR. SANJEEV KUMAR
(CHIEF ARCHITECT)

AR. DEVENDER SINGH
(SENIOR ARCHITECT)

AR. LALIT KUMAR
(ARCHITECT)

VACANT
(ASSTT. ARCHITECT)

OFFICE OF THE
CHIEF ARCHITECT
HARYANA, CHANDIGARH

STANDARD HEALTH WELLNESS CENTRE
DESIGN-I WITHOUT LABOUR ROOM AND
RESIDENCES

TARSEM KUMAR (A.D.)
DEALT BY:-

SUBHASH (A.A.)
CHECKED BY:-

JOB NO
3152

SCALE
NTS


DRG.NO
4C

DATE
NOV. 2024


DETAIL OF JOINERY

SCHEDULE OF JOINERY					
S.NO.	TYPE	SIZE	CILL	TOP	REMARKS
1	D/G	3.76 X 2.60	-	2.60	D=2.0 SOLID FLUSH DOOR WITH WIRE MESH SHUTTER
2	D1/G1	1.80 X 2.60	-	2.60	D1=1.06 SOLID FLUSH DOOR WITH WIRE MESH SHUTTER
3	D1	1.06 X 2.15	-	2.15	
4	D2	0.90 X 2.15	-	2.15	
5	W	1.80 X 1.70	0.90	2.60	
6	W-A	1.80 X 1.54	1.06	2.60	
7	W1	1.32 X 1.70	0.90	2.60	
8	V	0.90 X 0.45	2.15	2.60	

(GOOD FOR CONSTRUCTION)
NOTE:- ALL DIMENSIONS ARE IN METERS
UNLESS OTHERWISE SPECIFIED

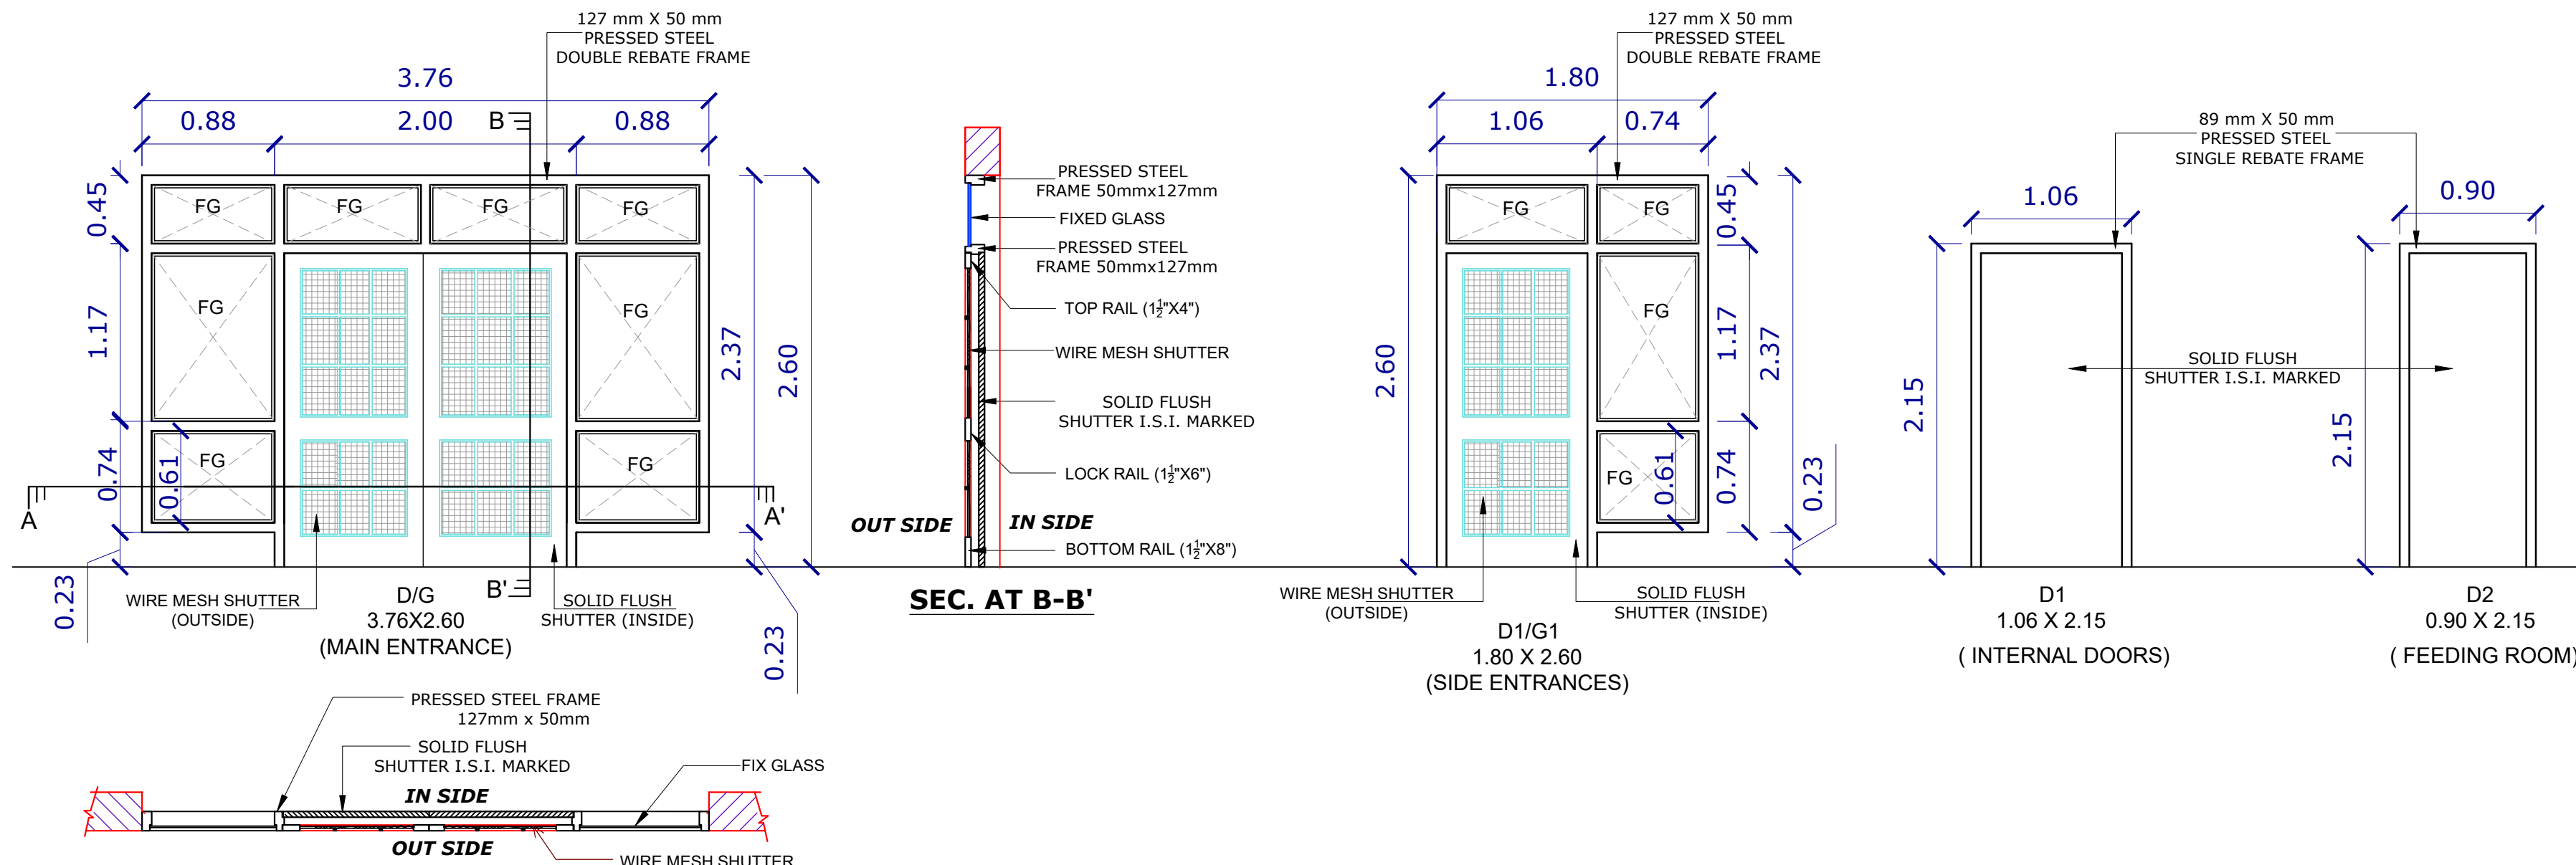

TYPICAL DETAIL OF M.S GRILL

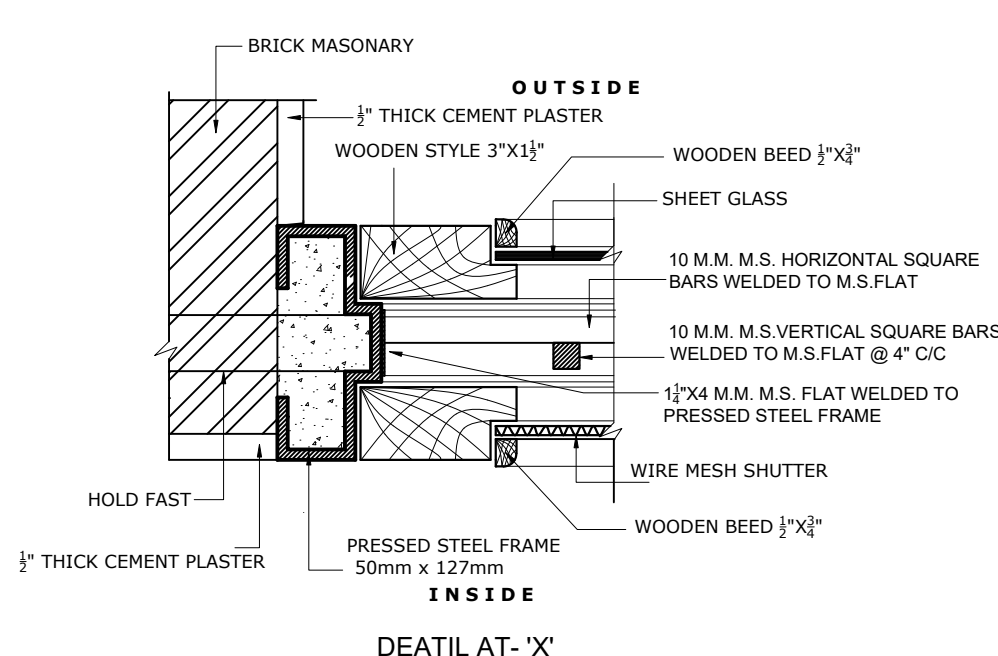

DEATIL AT- 'X'