



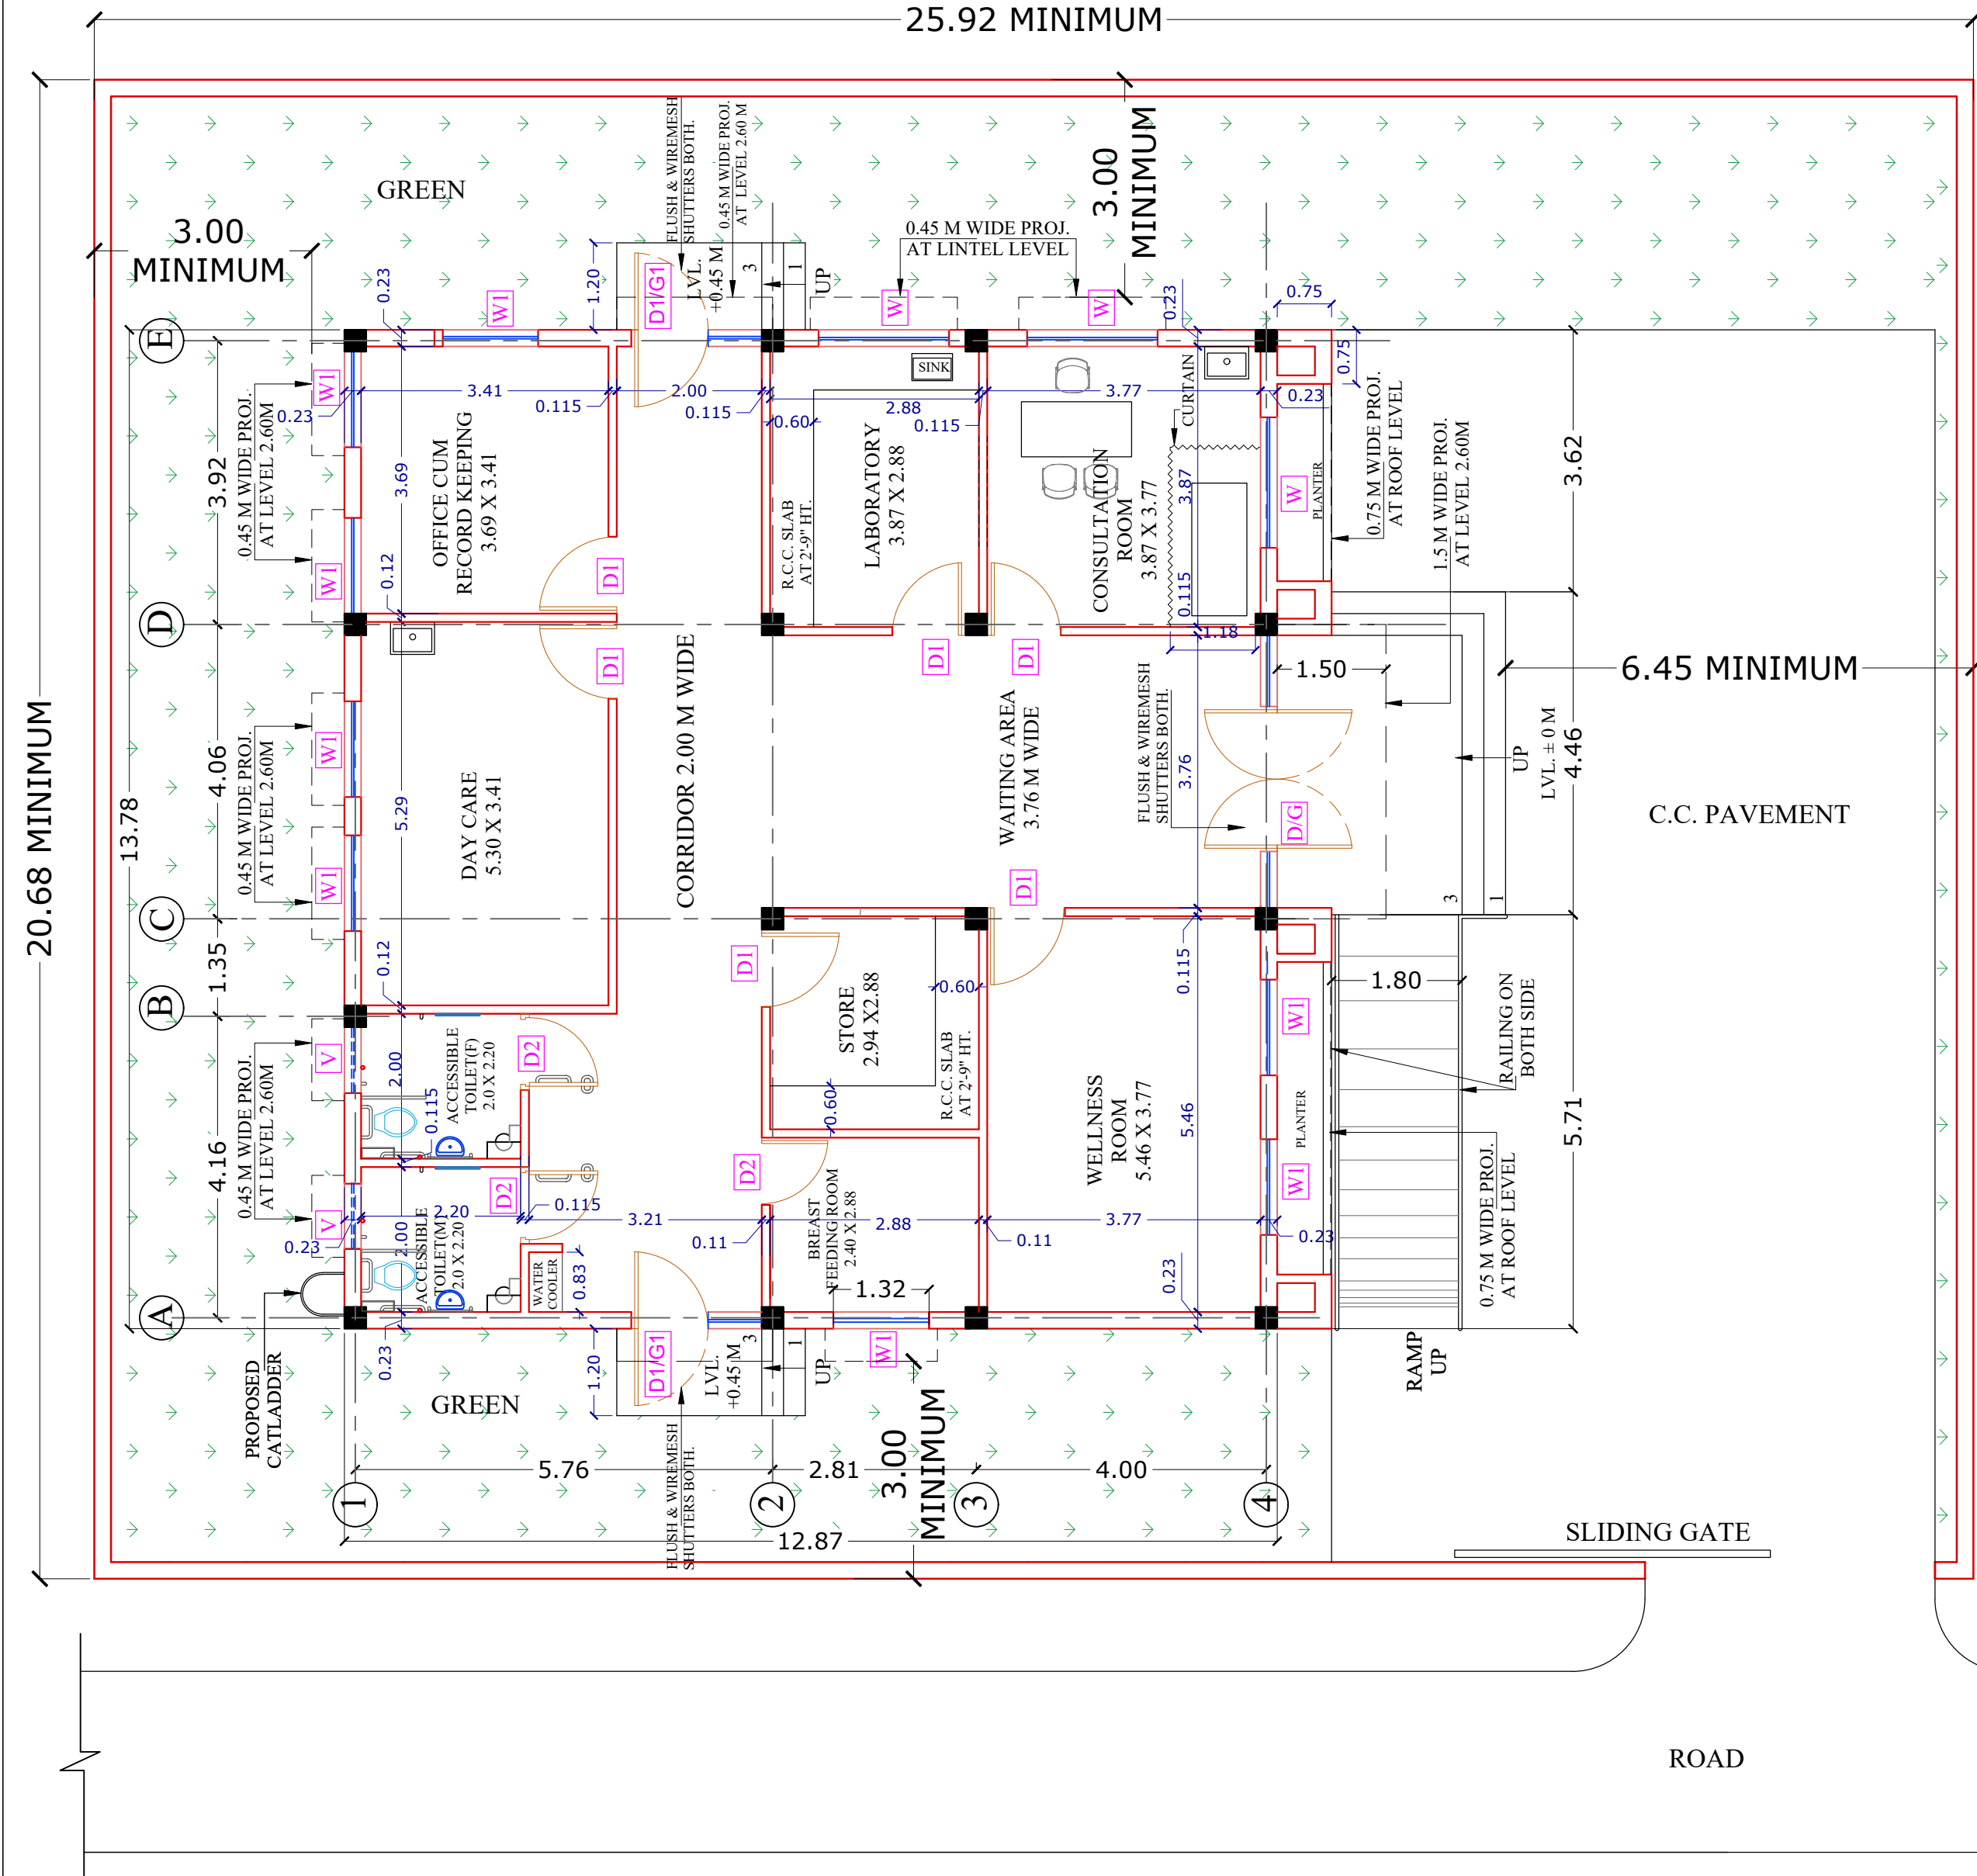

- GENERAL NOTES:-
- THESE STANDARD LAYOUT PLANS SHALL BE ADOPTED ON THE SITES HAVING AN AREA OF 536.02 SQ.MTR WITH MINIMUM SIDE DIMENSIONS OF 25.92 MTR. X 20.68 MTR. AND ON THOSE SITES HAVING AREA AND SIDE DIMENSIONS ARE MORE THAN AS SPECIFIED ABOVE.
 - ALL THE PROVISIONS OF HARYANA BUILDING CODE-2017 SHALL BE FULLY COMPLIED WITH DURING THE CONSTRUCTION.
 - THE EXECUTING AGENCY SHALL ENSURE PROPER ACCESS TO THE SUB HEALTH CENTRE IN COMPLIANCE WITH CHAPTER-IV OF HARYANA BUILDING CODE-2017.
 - THE HEIGHT OF THE BUILDING, MINIMUM SETBACKS AROUND THE BUILDING, F.A.R, GROUND COVERAGE ETC. SHALL BE MAINTAINED AS PER THE PROVISIONS OF HARYANA BUILDING CODE-2017.
 - ENSURE ADEQUATE NATURAL LIGHT AND VENTILATION AS STIPULATED IN CHAPTER-VI OF HARYANA BUILDING CODE-2017. THE MINIMUM SETBACKS AROUND THE HWC-SHC BUILDING SHALL BE LEFT OUT AS SHOWN IN THE STANDARD LAYOUT PLANS.
 - IF POSSIBLE, THE MAIN ENTRANCE OF THE HWC-SHC BUILDING SHALL PREFERABLY BE ALIGNED TOWARDS EAST OR NORTH DIRECTIONS TO TAKE ADVANTAGE OF NATURAL SUN LIGHT.
 - GATE AND BOUNDARY WALL SHALL BE PROVIDED AS PER THE PROVISIONS OF HARYANA BUILDING CODE-2017.
 - MANDATORY PROVISION OF PLINTH RAMP, RAILING, AND WASHROOM FOR DIVYANGS SHALL BE MADE.
 - APPLICABILITY OF SCHEDULED ROAD ACT ON ANY SITE SHALL BE CONFIRMED FROM THE CONCERNED AGENCY AND MINIMUM DISTANCE REQUIRED FROM THE ROAD BOUNDARY FOR PLACEMENT OF PROPOSED BUILDING BE LEFT PRIOR TO THE START OF CONSTRUCTION.
 - IF ANY SITE FALLS IN HSVP, MUNICIPAL LIMIT OR ANY OTHER JURISDICTION THEN ZONING PLAN OF THE SITE MAY BE ARRANGED FROM THE CONCERNED AUTHORITY PRIOR TO THE START OF CONSTRUCTION AND ITS ZONING CLAUSES SHALL BE ADHERED TO DURING CONSTRUCTION.
 - ANY RESTRICTION REGARDING GREEN BELT, ROAD WIDENING ETC IF APPLICABLE ON ANY SITE AS PER DEVELOPMENT/ SECTORAL PLAN TO BE CLARIFIED FROM THE CONCERNED DISTRICT TOWN PLANNER OFFICE PRIOR TO THE START OF CONSTRUCTION.
 - IF ANY SITE FALLS IN FOREST AREA THEN CLEARANCE FROM THE CONCERNED AUTHORITY SHALL BE TAKEN PRIOR TO THE START OF CONSTRUCTION.
 - MINIMUM IN HOUSE PROVISIONS OF FIRE FIGHTING AS PER TABLE-7 OF PART-4 (FIRE & LIFE SAFETY) OF NATIONAL BUILDING CODE-2016 SHALL BE MADE SO THAT IN CASE OF ANY FIRE EMERGENCY, THE SAME CAN BE IMMEDIATELY USED AND MAJOR LOSS OF LIFE AND PROPERTY CAN BE PREVENTED.
 - ALL THE MATERIAL SPECIFICATIONS AND FINISHING SHALL BE KEPT AS PER THE REVISED SPECIFICATIONS FOR BUILDING WORKS APPROVED BY THE GOVERNMENT AND ISSUED BY ENGINEER-IN-CHIEF (BUILDINGS), PWD B&R HARYANA VIDE MEMO NO. 99207/ WI DATED 24.07.2024.
 - THE APPROPRIATE PLINTH LEVEL OF THE SCHEME UNDER SUBJECT SHALL BE KEPT AFTER CONSULTING CONCERNED EXECUTIVE ENGINEER, PUBLIC HEALTH ENGINEERING/ IRRIGATION DEPARTMENT TO PREVENT FLOODING OF THE CAMPUS. FURTHER, IN CASE, EARTH FILLING IS REQUIRED TO BE UNDERTAKEN AT SITE THEN PRIOR INTIMATION & APPROVAL OF THE SAME SHALL BE OBTAINED FROM THE CLIENT DEPARTMENT BEFORE START OF EXECUTION OF WORK.
 - THE PLOT AREA/ DIMENSIONS ANGLES/ OWNERSHIP SHALL BE CROSS CHECKED AND CONFIRMED BY CONCERNED EXECUTING AGENCY AS PER ALLOTMENT LETTER/ REVENUE RECORD BEFORE TAKING ANY ACTION AT SITE.
 - THE PROPOSAL IS VALID SUBJECT TO TECHNICAL & STRUCTURAL FEASIBILITY AS PER SITE TO BE ASCERTAINED & CONFIRMED BY THE EXECUTING AGENCY AND ALL FINANCIAL REGULARITIES. THIS INCLUDES SHIFTING/RELOCATING OF PUBLIC HEALTH/ ELECTRICAL SERVICES, IF ANY AND REMOVAL OF EXISTING ENCUMBRANCES. REMOVAL OF EXISTING TREE, IF ANY, SHALL BE SUBJECT TO PRIOR APPROVAL OF THE COMPETENT AUTHORITY.
 - MINOR SITE SPECIFIC ADJUSTMENTS MAY BE MADE BY THE EXECUTING AGENCY AS NEEDED, PROVIDED THAT THEY REMAIN IN COMPLIANCE WITH THE ESSENTIAL REQUIREMENTS OF ACCESS, LIGHT AND VENTILATION AS OUTLINED IN THE HARYANA BUILDING CODE-2017.
 - IF THERE SHALL ANY PROBLEM DURING THE PROCESS OF LAYOUT AT ANY SITE THEN THAT PARTICULAR CASE BE SENT TO THIS OFFICE ALONGWITH T.S.S. AND ALL SITE DETAILS TO THIS OFFICE FOR PREPARATION OF THE LAYOUT PLAN.

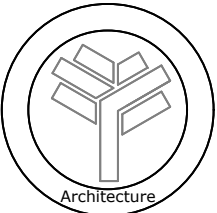

REVISIONS		
S.NO	DATE	DESCRIPTION

- NOTES:-
- THIS DRAWING IS THE PROPERTY OF THE DEPARTMENT OF ARCHITECTURE, GOVT. OF HARYANA. THIS DRAWING MAY NOT BE ALTERED, COPIED, USED IN WHOLE OR IN PART WITHOUT THE PERMISSION OF THIS DEPARTMENT IN WRITING.
 - THE DISCREPANCY, IF ANY MUST BE BROUGHT TO THE NOTICE OF THE DEPARTMENT OF ARCHITECTURE HARYANA BEFORE ANY ACTION AT SITE.
 - PLINTH LEVEL OF BUILDING SHALL BE FIXED IN CONSULTATION WITH CONCERNED EXECUTIVE ENGINEER PUBLIC HEALTH TO AVOID FLOODING OF CAMPUS.

THIS DESIGN OF HWC-SHC HAS BEEN FRAMED PURELY AS A SINGLE STOREY STRUCTURE WITH NO SCOPE OF FUTURE VERTICAL EXPANSION.

AREA STATEMENT	
TOTAL PLOT AREA	= 536.02 SQ.MT. = 0.13 ACRE
PERMISSIBLE GROUND COVERAGE	=35% OF 536.02= 187.60 SQ.MT.
GROUND COVERAGE ACHIEVED	= 187.60 SQ.MT. (2019.30 SQ.FT)

AR. SANJEEV KUMAR (CHIEF ARCHITECT)	
AR. DEVENDER SINGH (SENIOR ARCHITECT)	
AR. LALIT KUMAR (ARCHITECT)	VACANT (ASSTT.ARCHITECT)

OFFICE OF THE
CHIEF ARCHITECT
HARYANA, CHANDIGARH

STANDARD HEALTH WELLNESS
CENTRE DESIGN-I WITHOUT LABOUR
ROOM AND RESIDENCES

TARSEM KUMAR (A.D.) DEALT BY:-	SUBHASH (A.A.) CHECKED BY:-
JOB NO 3152	SCALE NTS
DRG.NO 3C	DATE NOV. 2024

STANDARD LAYOUT PLAN OPTION-02
(FOR STANDARD HEALTH WELLNESS CENTRE
DESIGN -I HAVING COVERED AREA OF 187.60 SQ.MT)

STANDARD HEALTH WELLNESS CENTRE DESIGN-I WITHOUT LABOUR ROOM AND RESIDENCES

(GOOD FOR CONSTRUCTION)

ALL DIMENSIONS ARE IN METERS
UNLESS OTHERWISE SPECIFIED