

From

The Director General,
Development & Panchayats Department,
Haryana, Chandigarh.

To

1. All Chief Executive Officers,
Zila Parishads in the state of Haryana.
2. All Executive Engineers,
Zila Parishads in the state of Haryana.

Memo No.PRC/2024/8853-54 Dated :- 25/11/2024

Ref. :- Director General, Health Services, Haryana, Const./2024/2055 dated 29.10.2024
& Chief Architect, Haryana memo no.Arch-2024/SA-III/11258-67 dated
08.11.2024 (copy enclosed).

Subject:- Construction of Health Wellness Centre (HWC - SHC) without labor room and
without residence at various village in the State of Haryana.

On the subject cited above, vide letter under reference it has been intimated by
Director General, Health services, Haryana that the standard design of Sub Health Centre
having a covered area of 187.60 sq. mtr. with standard layout plans (Option-1 & 2) of SHC-HWC
has been approved which is enclosed as Annexure "A".

In view of above, you are requested to prepare rough cost estimate (according
to new plinth area 187.60 sq. mtr. basis) for construction of HWC-SHC at various villages within
the budget i.e. Rs.55.5 lakh approved under 15th Finance Commission at the earliest.


for Sub-Divisional Officer
Director General,
Development & Panchayats Department
Haryana, Chandigarh

Endst. No. PRC/2024/ 8855-60

Dated : 25/11/2024

A copy of the above is forwarded to the following for information & necessary
action:-

1. The Director General, Health Services, Haryana for issuance of necessary guidelines to
CMO regarding identification of land/site.
2. The Chief Engineer, Panchayati Raj Public Works, Haryana.
3. The Chief Architect, Haryana.
4. PS to C&S, DP for kind information of Worthy Commissioner & Secretary to Government
of Haryana, Development & Panchayats Department.
5. PS to ACS for kind information of Worthy Additional Chief Secretary to Government of
Haryana, Health & Family Welfare Department.
6. Circle Head Draftsman, Drawing Branch, H.Q.


for Sub-Divisional Officer
Director General,
Development & Panchayats Department
Haryana, Chandigarh



Department of Architecture, Haryana

वास्तुकला विभाग, हरियाणा

Plot No. 1, Nirman Sadan, Sector 33-A, Chandigarh. 160020

प्लॉट नं. 1, निर्माण सदन, सेक्टर -33 ए, चंडीगढ़ 160020

E-mail: cahry@hry.nic.in



To

1. The Director General,
Development and Panchayats Department Haryana,
Panchayat Bhawan,
Plot No. 3, Sector-28, Chandigarh.
2. The Director,
Urban Local Bodies Department, Haryana,
Bays No. 11-14, Sector-4, Panchkula
3. The Engineer-In-Chief (Buildings) Haryana,
PWD B&R, Nirman Sadan,
Sector-33A, Chandigarh

Memo No. Arch-2024/SA-III/ 11258 - 60
Dated, Chandigarh the 08/11/24

Subject: - Construction of Health Wellness Centre (HWC - SHC) without labor room and without residence at various village in the State of Haryana.

Ref:- Memo no. Const./2024/2055 dated 29.10.2024 from the Director General Health Services, Haryana, Panchkula (photocopy attached)

In this regard, It is intimated that vide minutes of Meeting dated 10.10.2024 held under the chairmanship of worthy Addl. Chief Secretary to Govt. Haryana, Health Department received from the office of the Director General Health Services Haryana vide e-mail dated 18.10.2024, Health Department had requested this office to revise the earlier approved standard design of Health Wellness Centre (HWC-SHC) having a covered area of 212 Sq.mtr to 192 Sq.mtr to reduce the estimated cost of construction so that HWC-SHC at various villages can be constructed within the budget approved under 15th Finance Commission.

Further, in the above mentioned minutes of meeting, it was conveyed that large number of HWC-SHC are to be constructed in various villages of the State of Haryana and presently there is a delay in the process of preparation and submission of Total Station Survey (T.S.S.) plans and site details by the executing agencies and thereafter preparation of layout plans of each site by Department of Architecture, Haryana. To avoid delays and to ensure timely construction of these HWC-SHC, it will be better to allow executing agencies to proceed further for construction at their own level. To facilitate the executing agency, standard layout plans with execution guidelines shall required to be issued by the Department of Architecture, Haryana to Panchayati Raj Department Haryana so that Panchayati Raj Department need not to sent individual site plans to Department of Architecture and straight way take up the construction work as per the standard layout plans and execution guidelines issued by the Department of Architecture, Haryana.

Accordingly, as per the request of Health Department, the earlier approved design of HWC-SHC was revised by reducing the sizes of few rooms as per the discussions held with the Deputy Director (Construction) O/o the DGHS Haryana and Chief Engineer, Panchayati Raj, Haryana during their visit to this office on dated 10.10.2024. The covered area of the HWC-SHC had been reduced to 187.60 Sq.mtr. Also, based on the above mentioned standard design of Sub Health Centre (HWC-SHC) having a covered area of 187.60 Sq. mtr, this office had prepared 02 nos. standard layout plans to facilitate the construction agencies to take up the proposal of HWC-SHC buildings at own level.

The new design of HWC-SHC design - I having a covered area of 187.60 Sq.mtr and two nos. standard layout plans have been approved by the Director General Health Services, Haryana, Panchkula vide memo under reference under the intimation to the Director General Development and Panchayat Department Haryana, the Director Urban Local Bodies Haryana and the Engineer-In-Chief (Buildings) PWD B&R Haryana. The officers of Health Department telephonically informed that the approved drawings shall require to be supplied to the above mentioned Engineering Departments for taking up the proposal of HWC-SHC buildings at their own level.

Accordingly, attached please find the following approved drawings for taking further necessary action regarding construction of HWC-SHC buildings in various villages of the State of Haryana (except the villages of District Nuh) :-

Sr.No.	Description	Drg. No.	Job No.
1.	Standard Health Wellness Centre Design-I without labor room and without residence having a covered area of 187.60 Sq.mtr.	1C	3152
2.	Standard layout plan Option-I	2C	3152
3.	Standard layout plan Option-II	3C	3152
4.	Detail of Joinery	4C	3152

As such, the construction work of HWC-SHC buildings shall be taken up by the executing agencies at their own level subject to the following conditions:-

- The sizes of columns and beams as shown in the new standard design of HWC-SHC building having a covered area of 187.60 sq.mtr. bearing Drg. No. 1C of Job No. 3152 have been kept

same as of the original standard design having a covered area of 212.70 Sq.mtr. bearing Drg. No. 3R-1 of Job no. HWC and the same may be followed as per the revised structural advice. However, the location of columns and beams have been changed due to change in the size of few rooms to reduce the covered area of HWC-SHC building. Accordingly, the revised structural advice as per the new design of HWC-SHC building bearing Drg. No 1C of Job No. 3152 shall be taken prior to start of construction. The steel reinforcement in the columns, beams, lintels and roof slabs shall be designed and provided as per the requirement of seismic/ earthquake zone in which the proposed site falls. The foundation of the proposed HWC-SHC building shall be designed separately for each site according to the type of soil exists at different sites. Further, any requirement of drawings, if any, may be communicated to this office.

- The main entry side facade of the proposed SHC building has slightly been modified by providing joinery upto the height of 8'-6", projection over main entrance has been provided at 8'-6" height to enhance the appearance of the HWC-SHC building. The floor to ceiling height has also been reduced from 3.41 mtr. to 3.05 mtr.
- The proposal/provisions of sewerage disposal, water supply, rain water harvesting, fire safety measures, Light Emitting Diode (LED) lights for internal as well as campus lighting, Solar Photovoltaic Power Plant and other mandatory services shall be incorporated as per provisions made in Haryana Building Code-2017 in consultation with concerned department.
- A comprehensive public health and storm water drainage scheme may be worked out for the proposed HWC-SHC (without labour room and without residence) building before start of construction work.
- Electrical scheme shall be worked out prior to start of construction work and all partitions shall be aligned/flushed with R.C.C beams for proper conduit layout.
- The architectural drawings and structure drawings shall be cross checked/verified as per the public health advice, storm water advice, fire advice prepared by the consultant engaged through your office for its feasibility and shall be confirmed to this office before construction at site. In case of any discrepancy in any drawing this office shall be consulted before any action at site.
- The proposal is valid subject to technical & structural feasibility as per site to be ascertained & confirmed by your office and all financial regularities. This includes shifting/relocating of existing Public Health/ Electrical services, if any and removal of existing encumbrances. Removal of existing tree, if any, shall be subject to prior approval of the competent authority. The horticulture/landscape scheme may be got prepared through concerned Horticulture department in consultation with client department.
- All the material specifications and finishing shall be kept as per recommendation of the revised specification for building works approved by the Govt. vide letter no. 01/62/2024-1 B&R (W) dated 09.07.2024 and received in this office from E.I.C. (Buildings), PWD B&R, Haryana vide memo no. 99207/WI dated 24.07.2024. (copy attached through e-mail)
- Further, please refer to this office memo no. Arch-2023/Works/2102-03 dated 15.02.2023 (copy attached through email) & and Engineer-In-Chief, PWD B&R Haryana memo no. 32339-51 dated 09/03/2023 issued to all the Superintending Engineers and Executive Engineers vide which check list for preparation of Rough Cost Estimates and Detailed Estimates of the buildings was circulated. The provisions mentioned in the checklists shall be included in the estimates/ DNIT. Also, the notes as mentioned on the drawings may be gone through before preparing of estimates/ DNIT etc.
- This standard design of HWC-SHC building shall be adopted for construction in the various villages of the State of Haryana except the villages of District Nuh.
- These standard layout plans shall be adopted on the sites having an area of 536.02 Sq.mtr with minimum side dimensions of 25.92 mtr. X 20.68 mtr. and on those sites having area and side dimensions are more than as specified above.
- All the provisions of Haryana Building Code-2017 shall be fully complied with during the construction.
- The executing agency shall ensure proper access to the Sub Health Centre in compliance with Chapter-IV of Haryana Building Code-2017.
- The height of the building, minimum setbacks around the building, F.A.R, ground coverage etc. shall be maintained as per the provision of Haryana Building Code-2017.
- Ensure adequate natural light and ventilation as stipulated in Chapter-VI of Haryana Building Code-2017. The minimum setbacks around the HWC-SHC building shall be left out as shown in the standard layout plans.
- If possible, the main entrance of the HWC-SHC building shall preferably be aligned towards East or North directions to take advantage of natural Sun light.
- Gate and boundary wall shall be provided as per the provisions of Haryana Building Code-2017.
- Mandatory provision of plinth ramp, railing, and washroom for divyangs shall be made.
- Applicability of Scheduled Road Act on any site shall be confirmed from the concerned agency and minimum distance required from the road boundary for placement of proposed building be left prior to the start of construction.
- If any site falls in HSVP, municipal limit or any other jurisdiction then zoning plan of the site

- may be arranged from the concerned authority prior to start of construction and its zoning clauses shall be adhered to during construction.
- Any restriction regarding green belt, road widening etc if applicable on any site as per Development/ Sectoral Plan to be clarified from the concerned District Town Planner office prior to the start of construction.
- If any site falls in forest area then clearance from the concerned authority shall be taken prior to the start of construction.
- Minimum in house provisions of fire fighting as per table-7 of Part-4 (Fire & Life Safety) of National Building Code-2016 shall be made so that in case of any fire emergency, the same can be immediately used and major loss of life and property can be prevented.
- The appropriate plinth level of the scheme shall be kept after consulting concerned Executive Engineer, Public Health Engineering/ Irrigation Department to prevent flooding of the campus. Further, in case, earth filling is required to be undertaken at site then prior intimation & approval of the same shall be obtained from the client department before start of execution of work.
- The plot area/ dimensions angles/ ownership shall be cross checked and confirmed by concerned executing agency as per allotment letter/ Revenue Record before taking any action at site.
- Minor site specific adjustments may be made by the executing agency as needed, provided that they remain in compliance with the essential requirements of access, light and ventilation as outlined in the Haryana Building Code-2017.
- This design of HWC-SHC has been framed purely framed as a single storey structure with no scope of future expansion.
- If there shall any problem during the process of layout at any site, then that particular case be sent to this office along with T.S.S. and all site details to this office for preparation of the layout plan.

In case of any discrepancy in the drawings/ specifications, this office shall be consulted before taking any further action in the matter.

Lali
08 Nov 2024

(Ar. Lalit Kumar)
Architect
Chief Architect, Haryana,
Chandigarh.

DA/As above

S/C for

Endst.No. Arch-2024/SA-III/ 11261 - 67

Dated, the 08/11/24

A copy of the above is forwarded to the following for Information and necessary action: -

1. The Director General Health Services, Haryana, Swasthya Bhawan, Sector-6, Panchkula.
2. The Engineer-In-Chief, Public Health Engineering Department, Haryana, Bays No. 13-18, Sector-4, Panchkula.
3. The Chief Engineer, Panchayati Raj Haryana, Panchayat Bhawan, Plot No. 3, Sector-28, Chandigarh.
4. The Chief Engineer (Buildings), Haryana, PWD B&R, Nirman Sadan, Chandigarh.
5. The Chief Engineer (Electrical), Haryana, PWD B&R, Nirman Sadan, Chandigarh.
6. The Chief Engineer, Urban Local Bodies Department Haryana, Bays No. 11-14, Sector-4, Panchkula.
7. The Superintending Engineer, Haryana PWD B&R, Horticulture Circle, Chandigarh for evolving landscaping/ plantation plan.


Soft copy of the drawings (.pdf & dwg formats) of the above mentioned drawings have been sent through e-mail on dated 08.11.2024.

Lali
08/11/2024


DA/As above

S/C for

Architect,
Chief Architect Haryana,
Department of Architecture,
Chandigarh.

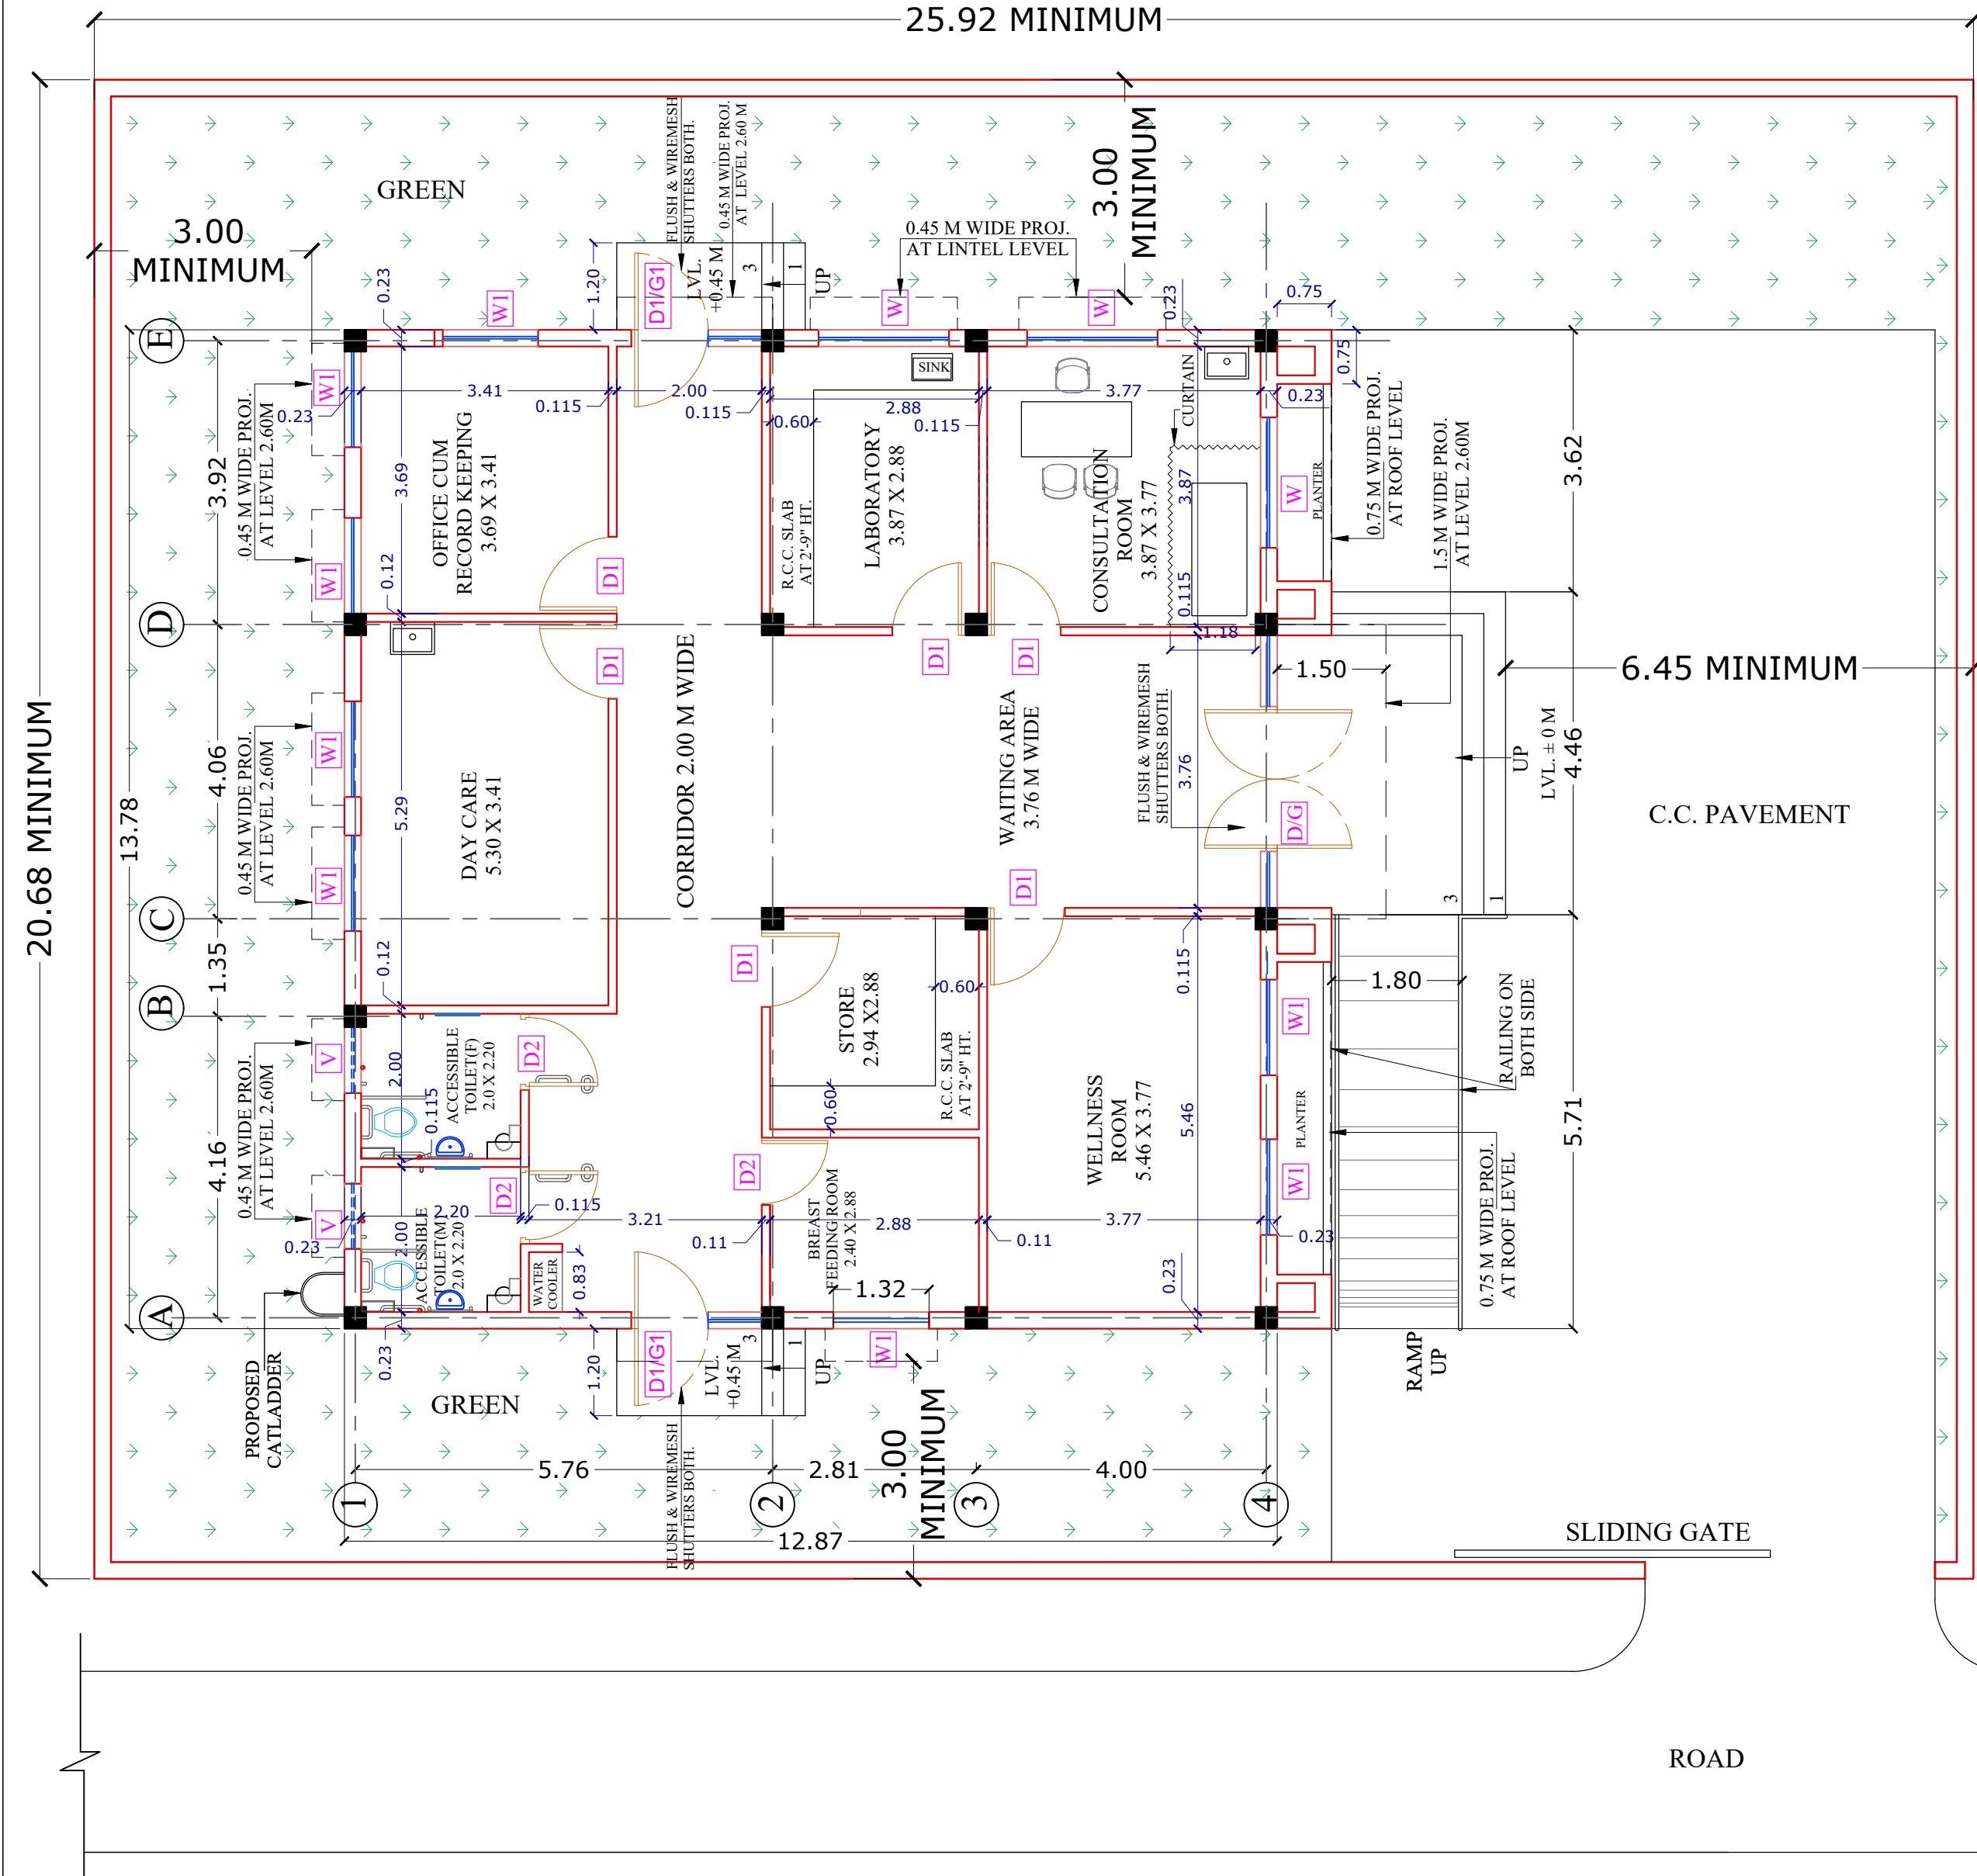

- GENERAL NOTES:-
- THESE STANDARD LAYOUT PLANS SHALL BE ADOPTED ON THE SITES HAVING AN AREA OF 536.02 SQ.MTR WITH MINIMUM SIDE DIMENSIONS OF 25.92 MTR. X 20.68 MTR. AND ON THOSE SITES HAVING AREA AND SIDE DIMENSIONS ARE MORE THAN AS SPECIFIED ABOVE.
 - ALL THE PROVISIONS OF HARYANA BUILDING CODE-2017 SHALL BE FULLY COMPLIED WITH DURING THE CONSTRUCTION.
 - THE EXECUTING AGENCY SHALL ENSURE PROPER ACCESS TO THE SUB HEALTH CENTRE IN COMPLIANCE WITH CHAPTER-IV OF HARYANA BUILDING CODE-2017.
 - THE HEIGHT OF THE BUILDING, MINIMUM SETBACKS AROUND THE BUILDING, F.A.R, GROUND COVERAGE ETC. SHALL BE MAINTAINED AS PER THE PROVISIONS OF HARYANA BUILDING CODE-2017.
 - ENSURE ADEQUATE NATURAL LIGHT AND VENTILATION AS STIPULATED IN CHAPTER-VI OF HARYANA BUILDING CODE-2017. THE MINIMUM SETBACKS AROUND THE HWC-SHC BUILDING SHALL BE LEFT OUT AS SHOWN IN THE STANDARD LAYOUT PLANS.
 - IF POSSIBLE, THE MAIN ENTRANCE OF THE HWC-SHC BUILDING SHALL PREFERABLY BE ALIGNED TOWARDS EAST OR NORTH DIRECTIONS TO TAKE ADVANTAGE OF NATURAL SUN LIGHT.
 - GATE AND BOUNDARY WALL SHALL BE PROVIDED AS PER THE PROVISIONS OF HARYANA BUILDING CODE-2017.
 - MANDATORY PROVISION OF PLINTH RAMP, RAILING, AND WASHROOM FOR DIVYANGS SHALL BE MADE.
 - APPLICABILITY OF SCHEDULED ROAD ACT ON ANY SITE SHALL BE CONFIRMED FROM THE CONCERNED AGENCY AND MINIMUM DISTANCE REQUIRED FROM THE ROAD BOUNDARY FOR PLACEMENT OF PROPOSED BUILDING BE LEFT PRIOR TO THE START OF CONSTRUCTION.
 - IF ANY SITE FALLS IN HSVP, MUNICIPAL LIMIT OR ANY OTHER JURISDICTION THEN ZONING PLAN OF THE SITE MAY BE ARRANGED FROM THE CONCERNED AUTHORITY PRIOR TO THE START OF CONSTRUCTION AND ITS ZONING CLAUSES SHALL BE ADHERED TO DURING CONSTRUCTION.
 - ANY RESTRICTION REGARDING GREEN BELT, ROAD WIDENING ETC IF APPLICABLE ON ANY SITE AS PER DEVELOPMENT/ SECTORAL PLAN TO BE CLARIFIED FROM THE CONCERNED DISTRICT TOWN PLANNER OFFICE PRIOR TO THE START OF CONSTRUCTION.
 - IF ANY SITE FALLS IN FOREST AREA THEN CLEARANCE FROM THE CONCERNED AUTHORITY SHALL BE TAKEN PRIOR TO THE START OF CONSTRUCTION.
 - MINIMUM IN HOUSE PROVISIONS OF FIRE FIGHTING AS PER TABLE-7 OF PART-4 (FIRE & LIFE SAFETY) OF NATIONAL BUILDING CODE-2016 SHALL BE MADE SO THAT IN CASE OF ANY FIRE EMERGENCY, THE SAME CAN BE IMMEDIATELY USED AND MAJOR LOSS OF LIFE AND PROPERTY CAN BE PREVENTED.
 - ALL THE MATERIAL SPECIFICATIONS AND FINISHING SHALL BE KEPT AS PER THE REVISED SPECIFICATIONS FOR BUILDING WORKS APPROVED BY THE GOVERNMENT AND ISSUED BY ENGINEER-IN-CHIEF (BUILDINGS), PWD B&R HARYANA VIDE MEMO NO. 99207/ WI DATED 24.07.2024.
 - THE APPROPRIATE PLINTH LEVEL OF THE SCHEME UNDER SUBJECT SHALL BE KEPT AFTER CONSULTING CONCERNED EXECUTIVE ENGINEER, PUBLIC HEALTH ENGINEERING/ IRRIGATION DEPARTMENT TO PREVENT FLOODING OF THE CAMPUS. FURTHER, IN CASE, EARTH FILLING IS REQUIRED TO BE UNDERTAKEN AT SITE THEN PRIOR INTIMATION & APPROVAL OF THE SAME SHALL BE OBTAINED FROM THE CLIENT DEPARTMENT BEFORE START OF EXECUTION OF WORK.
 - THE PLOT AREA/ DIMENSIONS ANGLES/ OWNERSHIP SHALL BE CROSS CHECKED AND CONFIRMED BY CONCERNED EXECUTING AGENCY AS PER ALLOTMENT LETTER/ REVENUE RECORD BEFORE TAKING ANY ACTION AT SITE.
 - THE PROPOSAL IS VALID SUBJECT TO TECHNICAL & STRUCTURAL FEASIBILITY AS PER SITE TO BE ASCERTAINED & CONFIRMED BY THE EXECUTING AGENCY AND ALL FINANCIAL REGULARITIES. THIS INCLUDES SHIFTING/RELOCATING OF PUBLIC HEALTH/ ELECTRICAL SERVICES, IF ANY AND REMOVAL OF EXISTING ENCUMBRANCES. REMOVAL OF EXISTING TREE, IF ANY, SHALL BE SUBJECT TO PRIOR APPROVAL OF THE COMPETENT AUTHORITY.
 - MINOR SITE SPECIFIC ADJUSTMENTS MAY BE MADE BY THE EXECUTING AGENCY AS NEEDED, PROVIDED THAT THEY REMAIN IN COMPLIANCE WITH THE ESSENTIAL REQUIREMENTS OF ACCESS, LIGHT AND VENTILATION AS OUTLINED IN THE HARYANA BUILDING CODE-2017.
 - IF THERE SHALL ANY PROBLEM DURING THE PROCESS OF LAYOUT AT ANY SITE THEN THAT PARTICULAR CASE BE SENT TO THIS OFFICE ALONGWITH T.S.S. AND ALL SITE DETAILS TO THIS OFFICE FOR PREPARATION OF THE LAYOUT PLAN.

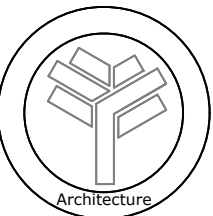

REVISIONS		
S.NO	DATE	DESCRIPTION

- NOTES:-
- THIS DRAWING IS THE PROPERTY OF THE DEPARTMENT OF ARCHITECTURE, GOVT. OF HARYANA. THIS DRAWING MAY NOT BE ALTERED, COPIED, USED IN WHOLE OR IN PART WITHOUT THE PERMISSION OF THIS DEPARTMENT IN WRITING.
 - THE DISCREPANCY, IF ANY MUST BE BROUGHT TO THE NOTICE OF THE DEPARTMENT OF ARCHITECTURE HARYANA BEFORE ANY ACTION AT SITE.
 - PLINTH LEVEL OF BUILDING SHALL BE FIXED IN CONSULTATION WITH CONCERNED EXECUTIVE ENGINEER PUBLIC HEALTH TO AVOID FLOODING OF CAMPUS.

THIS DESIGN OF HWC-SHC HAS BEEN FRAMED PURELY AS A SINGLE STOREY STRUCTURE WITH NO SCOPE OF FUTURE VERTICAL EXPANSION.

AREA STATEMENT	
TOTAL PLOT AREA	= 536.02 SQ.MT. = 0.13 ACRE
PERMISSIBLE GROUND COVERAGE	=35% OF 536.02= 187.60 SQ.MT.
GROUND COVERAGE ACHIEVED	= 187.60 SQ.MT. (2019.30 SQ.FT)

AR. SANJEEV KUMAR
(CHIEF ARCHITECT)

AR. DEVENDER SINGH
(SENIOR ARCHITECT)

AR. LALIT KUMAR (ARCHITECT)	VACANT (ASSTT.ARCHITECT)
--------------------------------	-----------------------------

OFFICE OF THE
CHIEF ARCHITECT
HARYANA, CHANDIGARH

STANDARD HEALTH WELLNESS
CENTRE DESIGN-I WITHOUT LABOUR
ROOM AND RESIDENCES


TARSEM KUMAR (A.D.) DEALT BY:-	SUBHASH (A.A.) CHECKED BY:-
JOB NO 3152	SCALE NTS
DRG.NO 3C	DATE NOV. 2024

STANDARD LAYOUT PLAN OPTION-02
(FOR STANDARD HEALTH WELLNESS CENTRE
DESIGN -I HAVING COVERED AREA OF 187.60 SQ.MT)


STANDARD HEALTH WELLNESS CENTRE DESIGN-I WITHOUT LABOUR ROOM AND RESIDENCES

(GOOD FOR CONSTRUCTION)

ALL DIMENSIONS ARE IN METERS
UNLESS OTHERWISE SPECIFIED

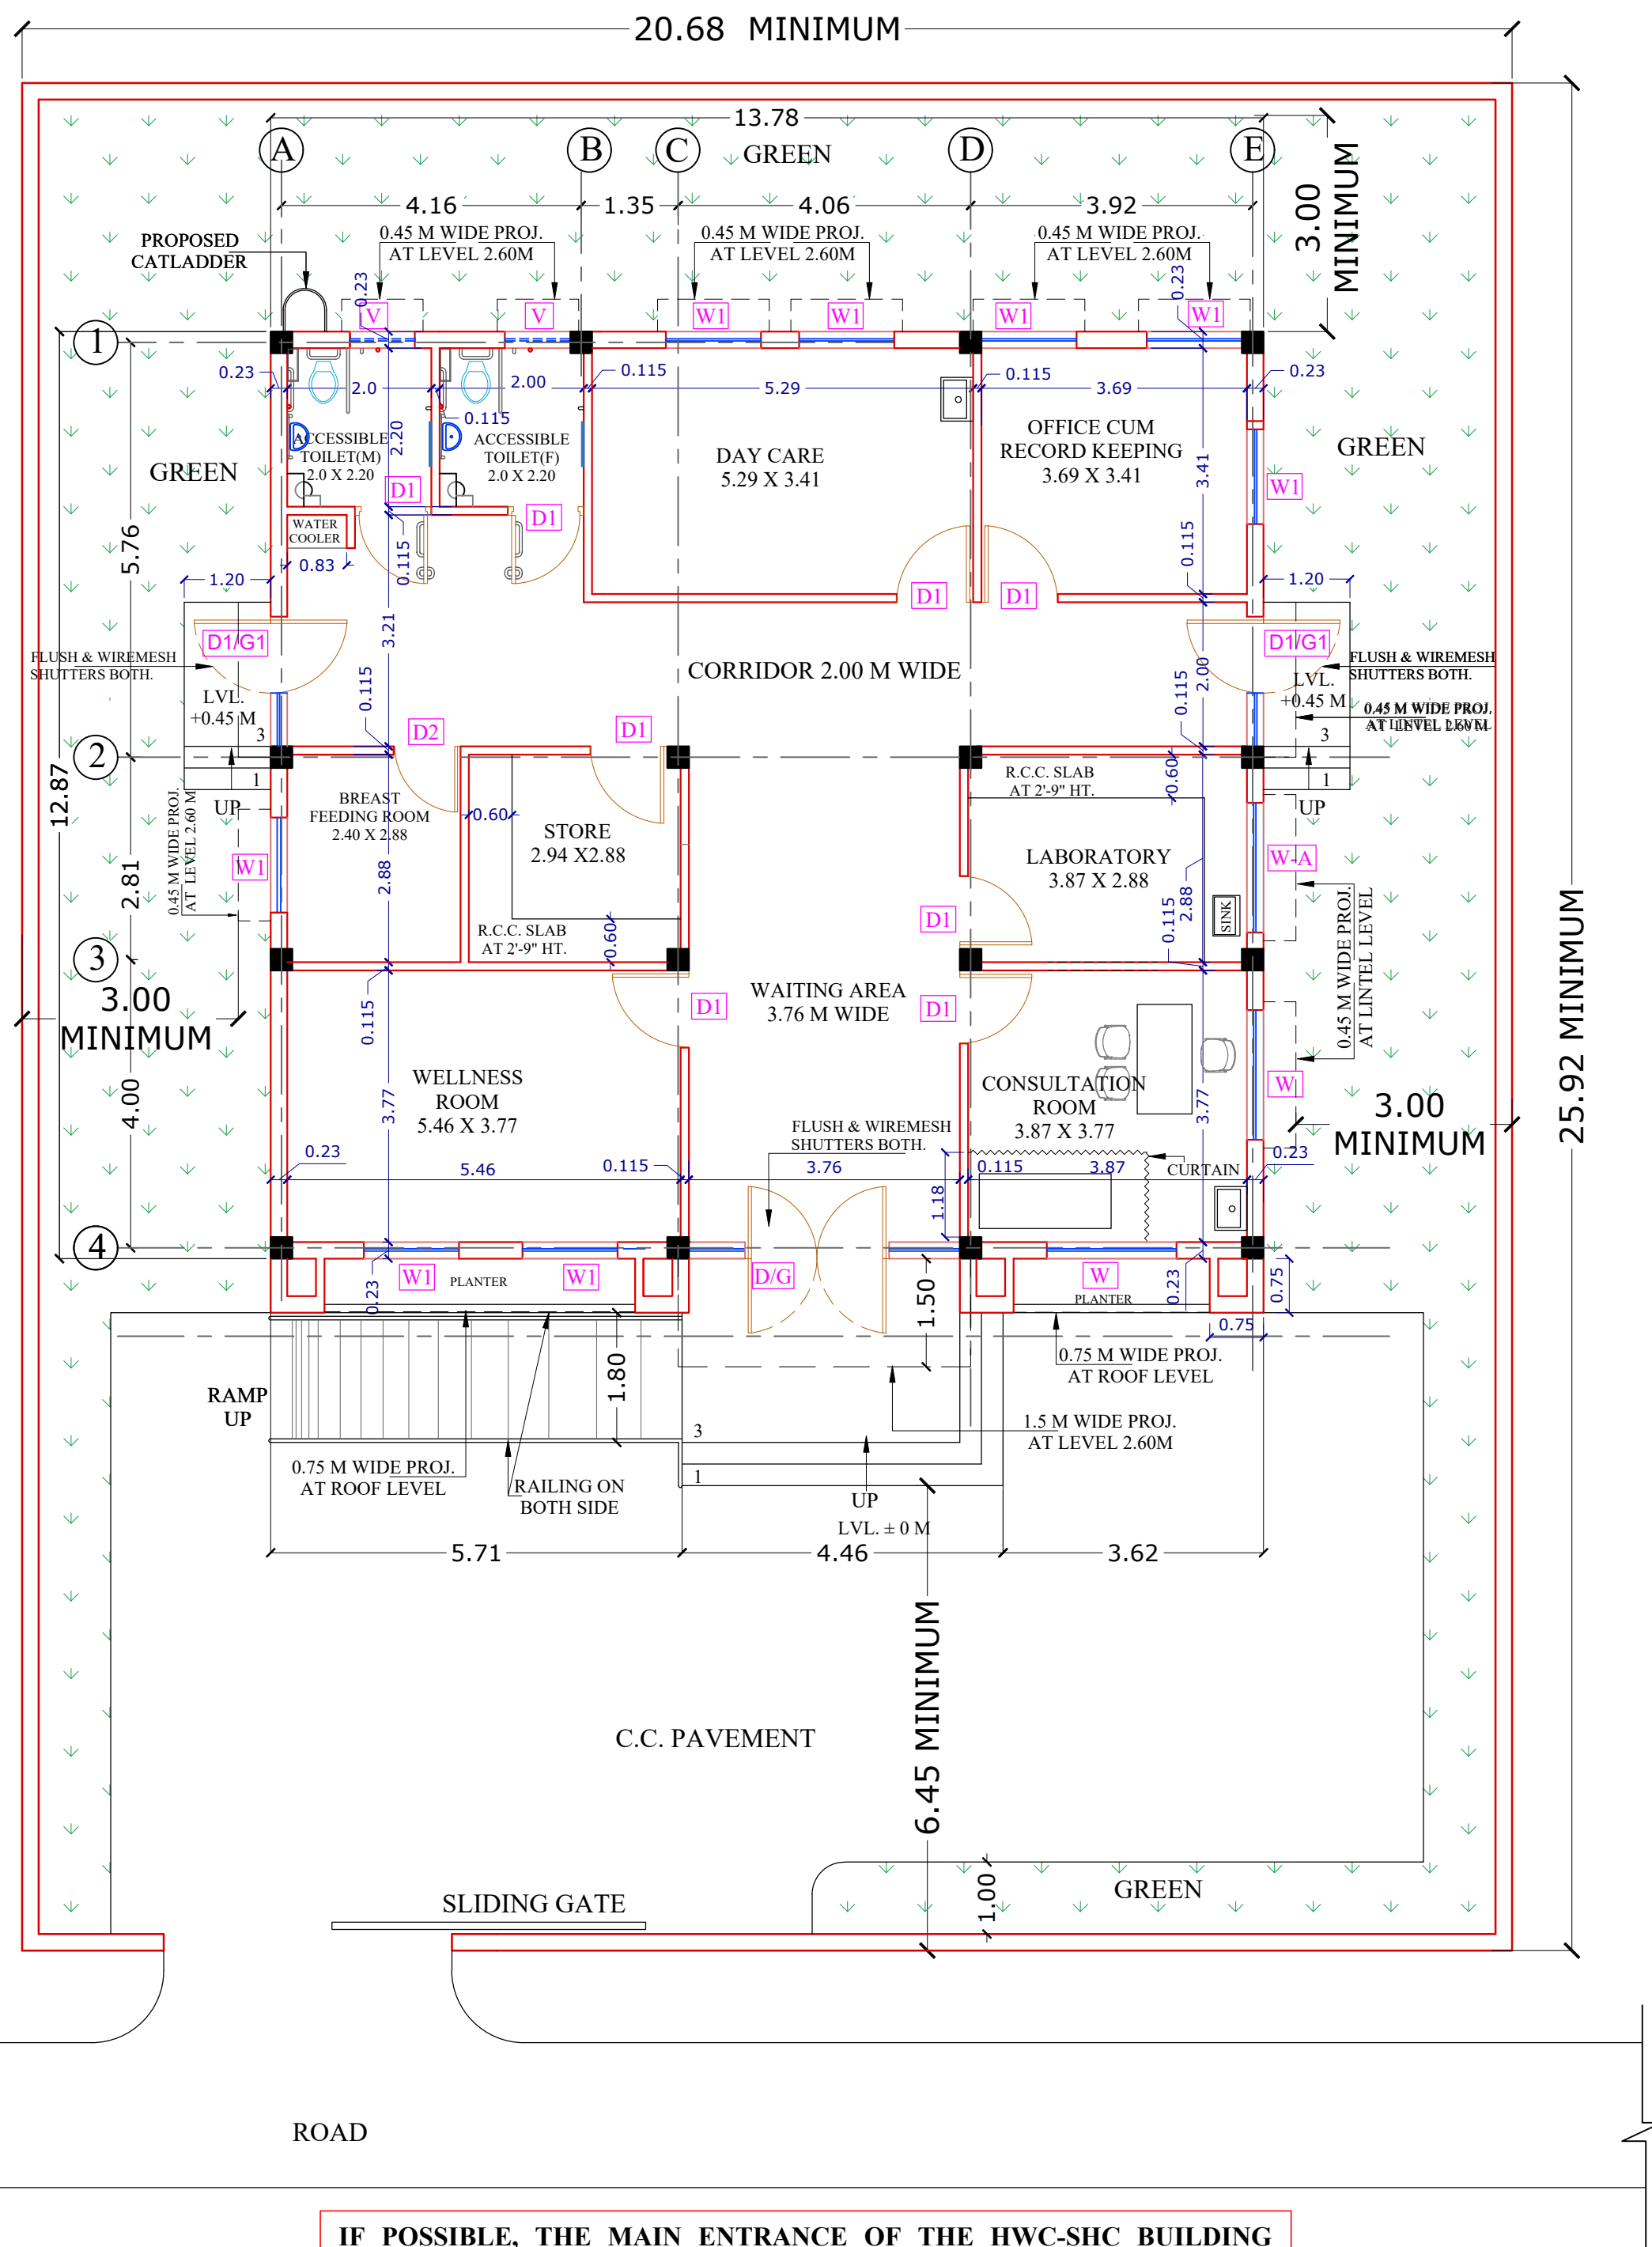

- GENERAL NOTES:-
- THESE STANDARD LAYOUT PLANS SHALL BE ADOPTED ON THE SITES HAVING AN AREA OF 536.02 SQ.MTR WITH MINIMUM SIDE DIMENSIONS OF 25.92 MTR. X 20.68 MTR. AND ON THOSE SITES HAVING AREA AND SIDE DIMENSIONS ARE MORE THAN AS SPECIFIED ABOVE.
 - ALL THE PROVISIONS OF HARYANA BUILDING CODE-2017 SHALL BE FULLY COMPLIED WITH DURING THE CONSTRUCTION.
 - THE EXECUTING AGENCY SHALL ENSURE PROPER ACCESS TO THE SUB HEALTH CENTRE IN COMPLIANCE WITH CHAPTER-IV OF HARYANA BUILDING CODE-2017.
 - THE HEIGHT OF THE BUILDING, MINIMUM SETBACKS AROUND THE BUILDING, F.A.R. GROUND COVERAGE ETC. SHALL BE MAINTAINED AS PER THE PROVISIONS OF HARYANA BUILDING CODE-2017.
 - ENSURE ADEQUATE NATURAL LIGHT AND VENTILATION AS STIPULATED IN CHAPTER-VI OF HARYANA BUILDING CODE-2017. THE MINIMUM SETBACKS AROUND THE HWC-SHC BUILDING SHALL BE LEFT OUT AS SHOWN IN THE STANDARD LAYOUT PLANS.
 - IF POSSIBLE, THE MAIN ENTRANCE OF THE HWC-SHC BUILDING SHALL PREFERABLY BE ALIGNED TOWARDS EAST OR NORTH DIRECTIONS TO TAKE ADVANTAGE OF NATURAL SUN LIGHT.
 - GATE AND BOUNDARY WALL SHALL BE PROVIDED AS PER THE PROVISIONS OF HARYANA BUILDING CODE-2017.
 - MANDATORY PROVISION OF PLINTH RAMP, RAILING, AND WASHROOM FOR DIVYANGS SHALL BE MADE.
 - APPLICABILITY OF SCHEDULED ROAD ACT ON ANY SITE SHALL BE CONFIRMED FROM THE CONCERNED AGENCY AND MINIMUM DISTANCE REQUIRED FROM THE ROAD BOUNDARY FOR PLACEMENT OF PROPOSED BUILDING BE LEFT PRIOR TO THE START OF CONSTRUCTION.
 - IF ANY SITE FALLS IN HSVP, MUNICIPAL LIMIT OR ANY OTHER JURISDICTION THEN ZONING PLAN OF THE SITE MAY BE ARRANGED FROM THE CONCERNED AUTHORITY PRIOR TO THE START OF CONSTRUCTION AND ITS ZONING CLAUSES SHALL BE ADHERED TO DURING CONSTRUCTION.
 - ANY RESTRICTION REGARDING GREEN BELT, ROAD WIDENING ETC IF APPLICABLE ON ANY SITE AS PER DEVELOPMENT/ SECTORAL PLAN TO BE CLARIFIED FROM THE CONCERNED DISTRICT TOWN PLANNER OFFICE PRIOR TO THE START OF CONSTRUCTION.
 - IF ANY SITE FALLS IN FOREST AREA THEN CLEARANCE FROM THE CONCERNED AUTHORITY SHALL BE TAKEN PRIOR TO THE START OF CONSTRUCTION.
 - MINIMUM IN HOUSE PROVISIONS OF FIRE FIGHTING AS PER TABLE-7 OF PART-4 (FIRE & LIFE SAFETY) OF NATIONAL BUILDING CODE-2016 SHALL BE MADE SO THAT IN CASE OF ANY FIRE EMERGENCY, THE SAME CAN BE IMMEDIATELY USED AND MAJOR LOSS OF LIFE AND PROPERTY CAN BE PREVENTED.
 - ALL THE MATERIAL SPECIFICATIONS AND FINISHING SHALL BE KEPT AS PER THE REVISED SPECIFICATIONS FOR BUILDING WORKS APPROVED BY THE GOVERNMENT AND ISSUED BY ENGINEER-IN-CHIEF (BUILDINGS), PWD B&R HARYANA VIDE MEMO NO. 99207/ WI DATED 24.07.2024.
 - THE APPROPRIATE PLINTH LEVEL OF THE SCHEME SHALL BE KEPT AFTER CONSULTING CONCERNED EXECUTIVE ENGINEER, PUBLIC HEALTH ENGINEERING/ IRRIGATION DEPARTMENT TO PREVENT FLOODING OF THE CAMPUS. FURTHER, IN CASE, EARTH FILLING IS REQUIRED TO BE UNDERTAKEN AT SITE THEN PRIOR INTIMATION & APPROVAL OF THE SAME SHALL BE OBTAINED FROM THE CLIENT DEPARTMENT BEFORE START OF EXECUTION OF WORK.
 - THE PLOT AREA/ DIMENSIONS ANGLES/ OWNERSHIP SHALL BE CROSS CHECKED AND CONFIRMED BY CONCERNED EXECUTING AGENCY AS PER ALLOTMENT LETTER/ REVENUE RECORD BEFORE TAKING ANY ACTION AT SITE.
 - THE PROPOSAL IS VALID SUBJECT TO TECHNICAL & STRUCTURAL FEASIBILITY AS PER SITE TO BE ASCERTAINED & CONFIRMED BY THE EXECUTING AGENCY AND ALL FINANCIAL REGULARITIES, THIS INCLUDES SHIFTING/RELOCATING OF PUBLIC HEALTH/ ELECTRICAL SERVICES, IF ANY AND REMOVAL OF EXISTING ENCUMBRANCES. REMOVAL OF EXISTING TREE, IF ANY, SHALL BE SUBJECT TO PRIOR APPROVAL OF THE COMPETENT AUTHORITY.
 - MINOR SITE SPECIFIC ADJUSTMENTS MAY BE MADE BY THE EXECUTING AGENCY AS NEEDED, PROVIDED THAT THEY REMAIN IN COMPLIANCE WITH THE ESSENTIAL REQUIREMENTS OF ACCESS, LIGHT AND VENTILATION AS OUTLINED IN THE HARYANA BUILDING CODE-2017.
 - IF THERE SHALL ANY PROBLEM DURING THE PROCESS OF LAYOUT AT ANY SITE THEN THAT PARTICULAR CASE BE SENT TO THIS OFFICE ALONGWITH T.S.S. AND ALL SITE DETAILS TO THIS OFFICE FOR PREPARATION OF THE LAYOUT PLAN.

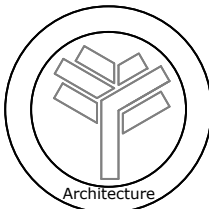

REVISIONS		
S.NO	DATE	DESCRIPTION

- NOTES:-
- THIS DRAWING IS THE PROPERTY OF THE DEPARTMENT OF ARCHITECTURE, GOVT. OF HARYANA. THIS DRAWING MAY NOT BE ALTERED, COPIED, USED IN WHOLE OR IN PART WITHOUT THE PERMISSION OF THIS DEPARTMENT IN WRITING.
 - THE DISCREPANCY, IF ANY MUST BE BROUGHT TO THE NOTICE OF THE DEPARTMENT OF ARCHITECTURE HARYANA BEFORE ANY ACTION AT SITE.
 - PLINTH LEVEL OF BUILDING SHALL BE FIXED IN CONSULTATION WITH CONCERNED EXECUTIVE ENGINEER PUBLIC HEALTH TO AVOID FLOODING OF CAMPUS.

THIS DESIGN OF HWC-SHC HAS BEEN FRAMED PURELY AS A SINGLE STOREY STRUCTURE WITH NO SCOPE OF FUTURE VERTICAL EXPANSION.

AREA STATEMENT	
TOTAL PLOT AREA	= 536.02 SQ.MT. = 0.13 ACRE
PERMISSIBLE GROUND COVERAGE	=35% OF 536.02= 187.60 SQ.MT.
GROUND COVERAGE ACHIEVED	= 187.60 SQ.MT. (2019.30 SQ.FT)


AR. SANJEEV KUMAR (CHIEF ARCHITECT)	
AR. DEVENDER SINGH (SENIOR ARCHITECT)	
AR. LALIT KUMAR (ARCHITECT)	VACANT (ASSTT.ARCHITECT)

OFFICE OF THE CHIEF ARCHITECT HARYANA, CHANDIGARH	
STANDARD HEALTH WELLNESS CENTRE DESIGN-I WITHOUT LABOUR ROOM AND RESIDENCES	
TARSEM KUMAR (A.D.) DEALT BY:-	SUBHASH (A.A.) CHECKED BY:-
JOB NO 3152	SCALE NTS
DRG.NO 2C	DATE NOV. 2024

STANDARD LAYOUT PLAN OPTION-01
(FOR STANDARD HEALTH WELLNESS CENTRE
DESIGN -I HAVING COVERED AREA OF 187.60 SQ.MT)






(GOOD FOR CONSTRUCTION)

ALL DIMENSIONS ARE IN METERS
UNLESS OTHERWISE SPECIFIED

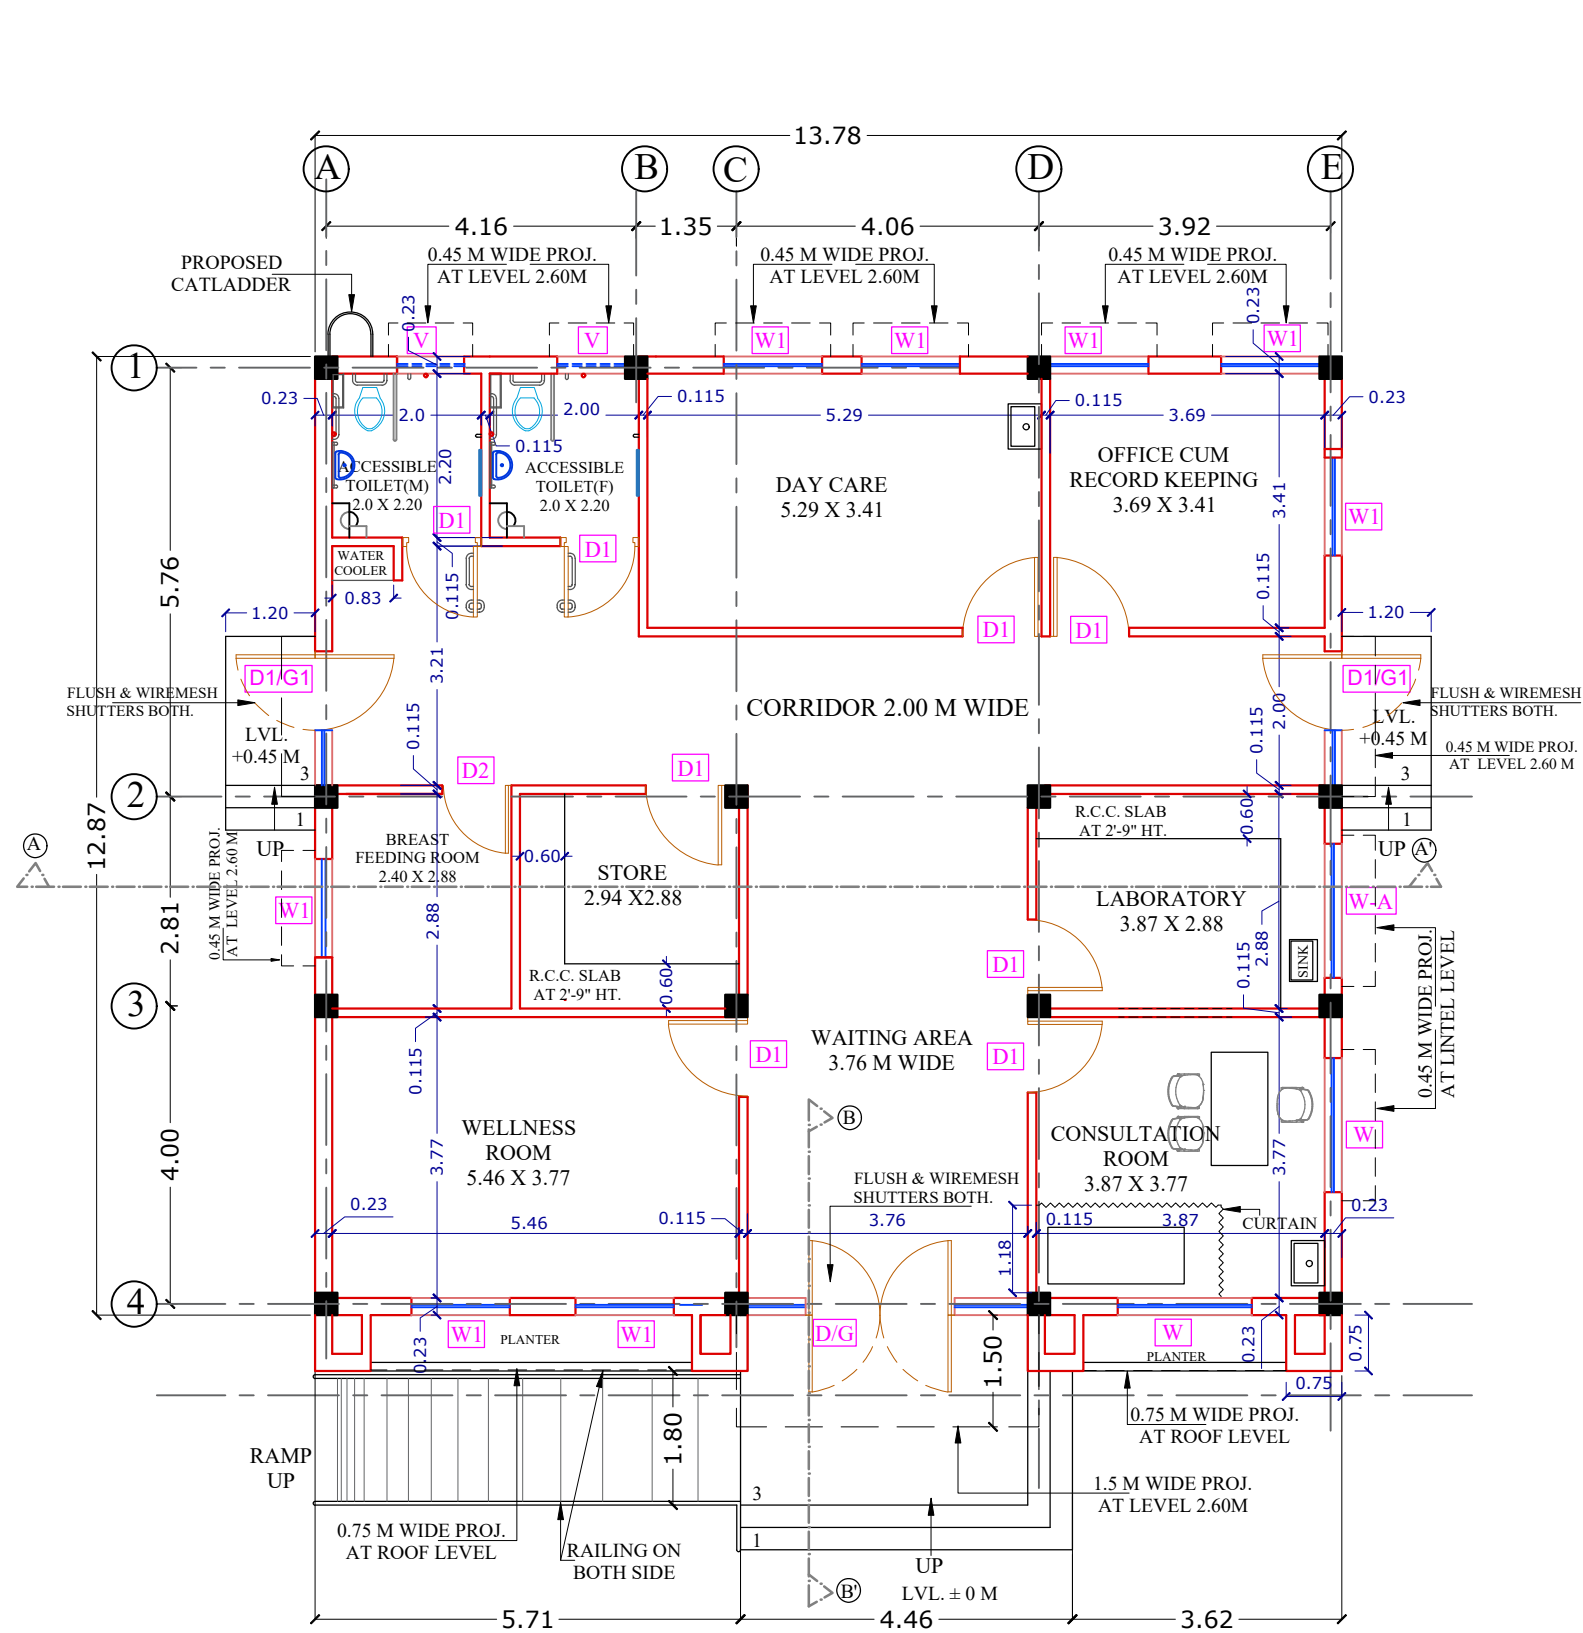

ACTUAL SIZE AND STEEL REINFORCEMENT IN COLUMNS AND BEAMS SHALL BE AS PER STRUCTURE ADVISE.

TENTATIVE SIZE OF COLUMNS & BEAMS	
COLUMN	BEAM

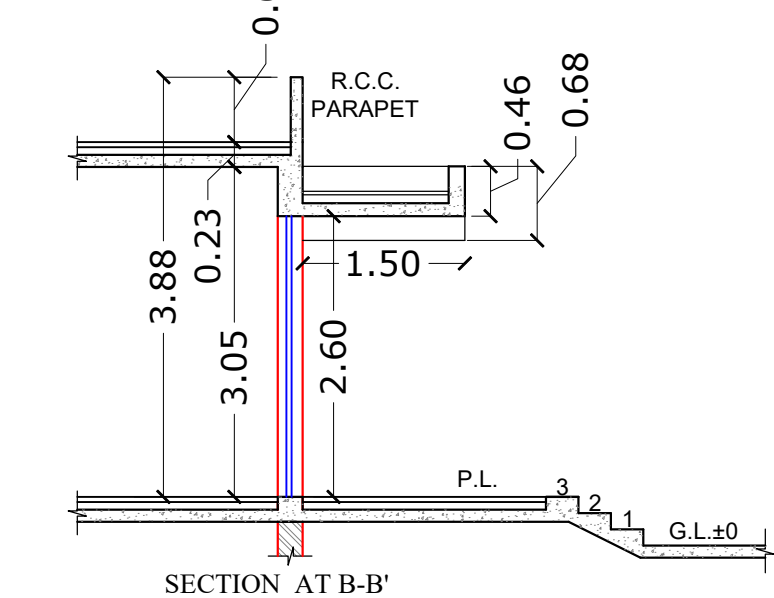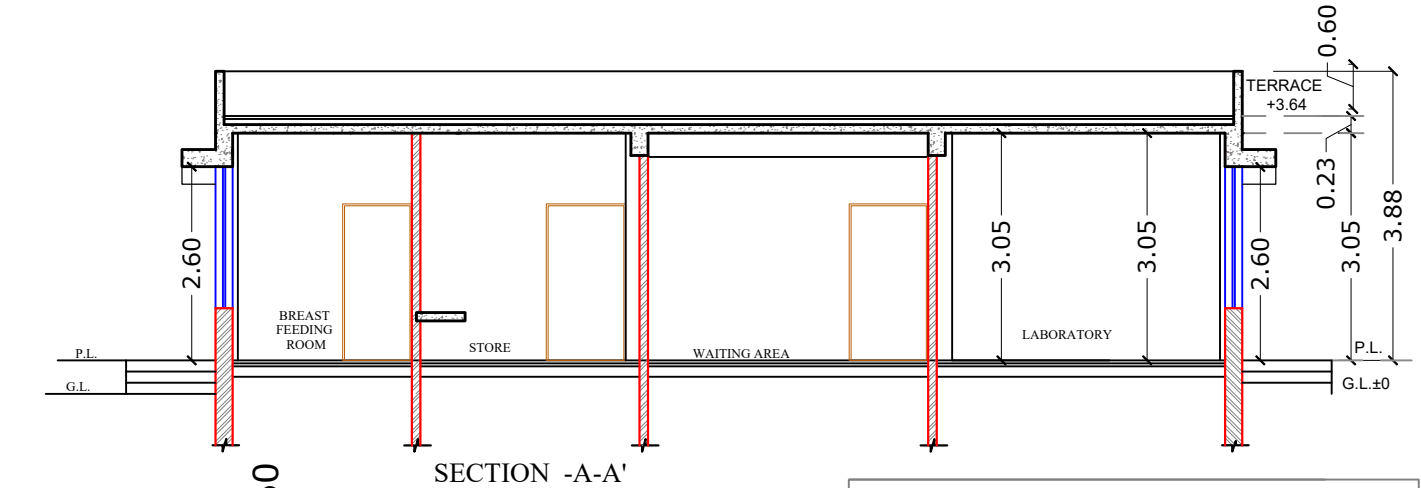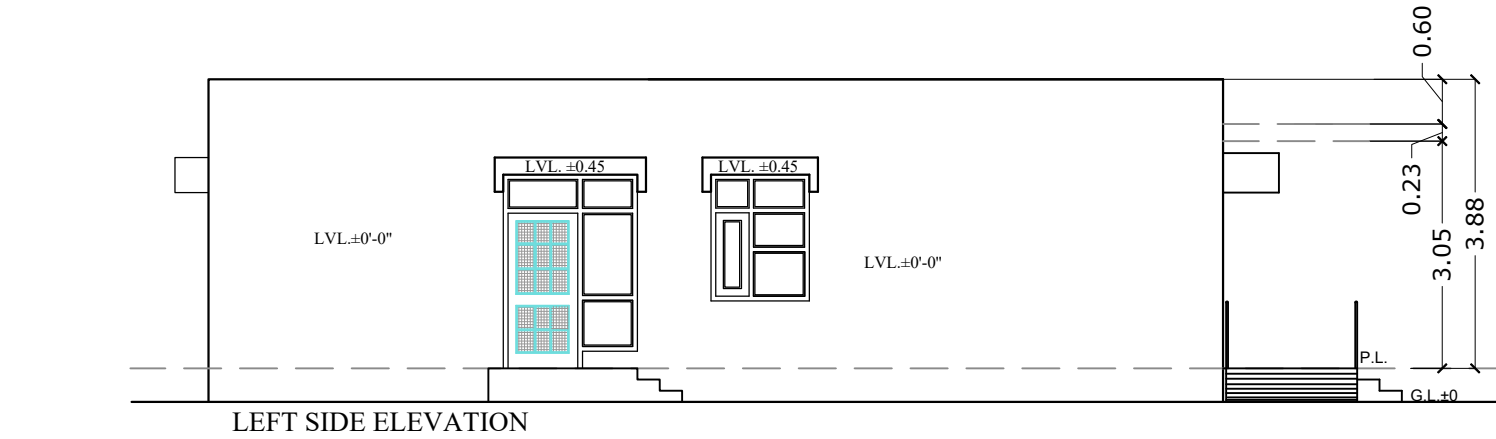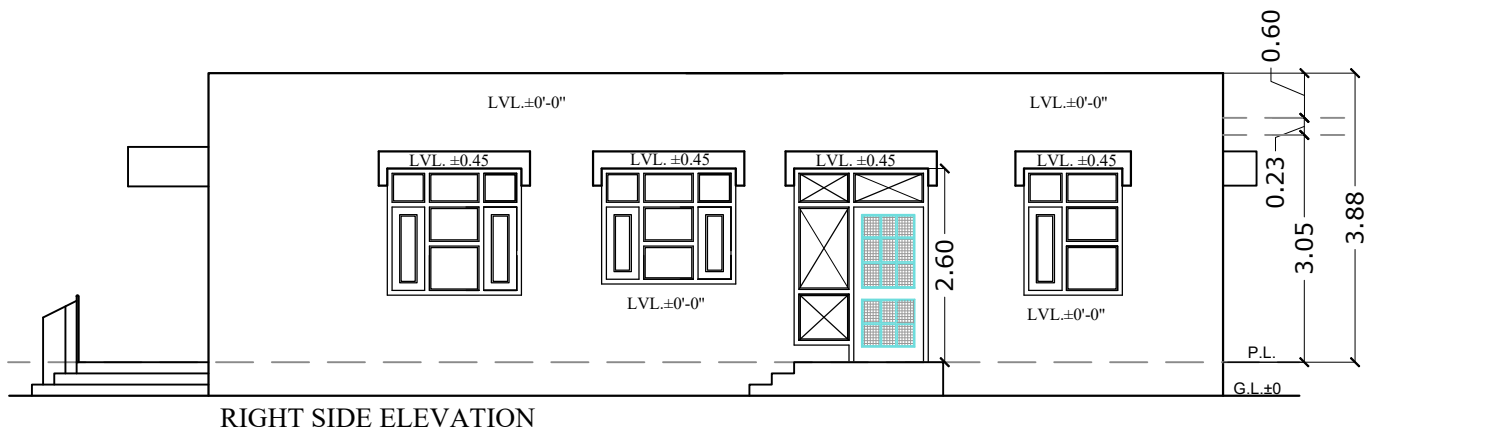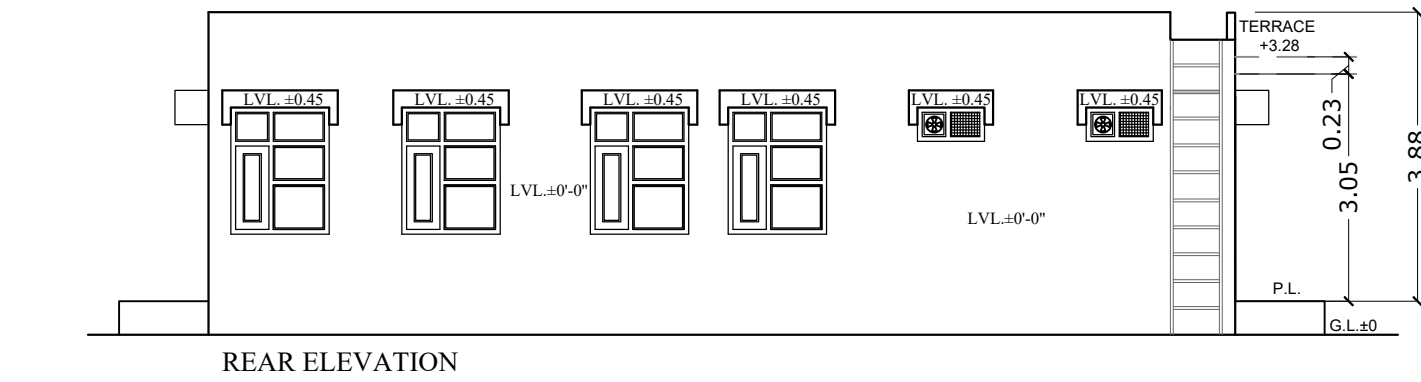


SCHEDULE OF JOINERY					
S.NO.	TYPE	SIZE	CILL	TOP	REMARKS
1	D/G	3.76 X 2.60	-	2.60	D=2.0 SOLID FLUSH DOOR WITH WIRE MESH SHUTTER
2	D1/G1	1.80 X 2.60	-	2.60	D1=1.06 SOLID FLUSH DOOR WITH WIRE MESH SHUTTER
3	D1	1.06 X 2.15	-	2.15	
4	D2	0.90 X 2.15	-	2.15	
5	W	1.80 X 1.70	0.90	2.60	
6	W-A	1.80 X 1.54	1.06	2.60	
7	W1	1.32 X 1.70	0.90	2.60	
8	V	0.90 X 0.45	2.15	2.60	

THIS DESIGN OF HWC-SHC HAS BEEN FRAMED PURELY AS A SINGLE STOREY STRUCTURE WITH NO SCOPE OF FUTURE VERTICAL EXPANSION.

APPROVAL NOTE:-
THIS DRAWING HAS BEEN APPROVED BY WORTH DIRECTOR GENERAL HEALTH SERVICES, HARYANA VIDE HIS OFFICE MEMO NO. Const./2024/2055 DATED 29/10/2024.

- ALL THE PROVISIONS OF HARYANA BUILDING CODE-2017 SHALL BE FULLY COMPLIED WITH DURING THE CONSTRUCTION.
- THE EXECUTING AGENCY SHALL ENSURE PROPER ACCESS TO THE SUB HEALTH CENTRE IN COMPLIANCE WITH CHAPTER-IV OF HARYANA BUILDING CODE-2017.
- THE HEIGHT OF THE BUILDING, MINIMUM SETBACKS AROUND THE BUILDING, F.A.R, GROUND COVERAGE ETC. SHALL BE MAINTAINED AS PER THE PROVISIONS OF HARYANA BUILDING CODE-2017.
- ENSURE ADEQUATE NATURAL LIGHT AND VENTILATION AS STIPULATED IN CHAPTER-VI OF HARYANA BUILDING CODE-2017. THE MINIMUM SETBACKS AROUND THE HWC-SHC BUILDING SHALL BE LEFT OUT AS SHOWN IN THE STANDARD LAYOUT PLANS.
- IF POSSIBLE, THE MAIN ENTRANCE OF THE HWC-SHC BUILDING SHALL PREFERABLY BE ALIGNED TOWARDS EAST OR NORTH DIRECTIONS TO TAKE ADVANTAGE OF NATURAL SUN LIGHT.
- GATE AND BOUNDARY WALL SHALL BE PROVIDED AS PER THE PROVISIONS OF HARYANA BUILDING CODE-2017.
- MANDATORY PROVISION OF PLINTH RAMP, RAILING, AND WASHROOM FOR DIVYANGS SHALL BE MADE.
- APPLICABILITY OF SCHEDULED ROAD ACT ON ANY SITE SHALL BE CONFIRMED FROM THE CONCERNED AGENCY AND MINIMUM DISTANCE REQUIRED FROM THE ROAD BOUNDARY FOR PLACEMENT OF PROPOSED BUILDING BE LEFT PRIOR TO THE START OF CONSTRUCTION.
- IF ANY SITE FALLS IN HSVP, MUNICIPAL LIMIT OR ANY OTHER JURISDICTION THEN ZONING PLAN OF THE SITE MAY BE ARRANGED FROM THE CONCERNED AUTHORITY PRIOR TO THE START OF CONSTRUCTION AND ITS ZONING CLAUSES SHALL BE ADHERED TO DURING CONSTRUCTION.
- ANY RESTRICTION REGARDING GREEN BELT, ROAD WIDENING ETC IF APPLICABLE ON ANY SITE AS PER DEVELOPMENT/ SECTORAL PLAN TO BE CLARIFIED FROM THE CONCERNED DISTRICT TOWN PLANNER OFFICE PRIOR TO THE START OF CONSTRUCTION.
- IF ANY SITE FALLS IN FOREST AREA THEN CLEARANCE FROM THE CONCERNED AUTHORITY SHALL BE TAKEN PRIOR TO THE START OF CONSTRUCTION.
- MINIMUM IN HOUSE PROVISIONS OF FIRE FIGHTING AS PER TABLE-7 OF PART-4 (FIRE & LIFE SAFETY) OF NATIONAL BUILDING CODE-2016 SHALL BE MADE SO THAT IN CASE OF ANY FIRE EMERGENCY, THE SAME CAN BE IMMEDIATELY USED AND MAJOR LOSS OF LIFE AND PROPERTY CAN BE PREVENTED.
- ALL THE MATERIAL SPECIFICATIONS AND FINISHING SHALL BE KEPT AS PER THE REVISED SPECIFICATIONS FOR BUILDING WORKS APPROVED BY THE GOVERNMENT AND ISSUED BY ENGINEER-IN-CHIEF (BUILDINGS), PWD B&R HARYANA VIDE MEMO NO. 99207/ WI DATED 24.07.2024.
- THE APPROPRIATE PLINTH LEVEL OF THE SCHEME SHALL BE KEPT AFTER CONSULTING CONCERNED EXECUTIVE ENGINEER, PUBLIC HEALTH ENGINEERING/ IRRIGATION DEPARTMENT TO PREVENT FLOODING OF THE CAMPUS. FURTHER, IN CASE, EARTH FILLING IS REQUIRED TO BE UNDERTAKEN AT SITE THEN PRIOR INTIMATION & APPROVAL OF THE SAME SHALL BE OBTAINED FROM THE CLIENT DEPARTMENT BEFORE START OF EXECUTION OF WORK.
- THE PLOT AREA/ DIMENSIONS ANGLES/ OWNERSHIP SHALL BE CROSS CHECKED AND CONFIRMED BY CONCERNED EXECUTING AGENCY AS PER ALLOTMENT LETTER/ REVENUE RECORD BEFORE TAKING ANY ACTION AT SITE.
- THE PROPOSAL IS VALID SUBJECT TO TECHNICAL & STRUCTURAL FEASIBILITY AS PER SITE TO BE ASCERTAINED & CONFIRMED BY THE EXECUTING AGENCY AND ALL FINANCIAL REGULARITIES, THIS INCLUDES SHIFTING/RELOCATING OF PUBLIC HEALTH/ ELECTRICAL SERVICES, IF ANY AND REMOVAL OF EXISTING ENCUMBRANCES, REMOVAL OF EXISTING TREE, IF ANY, SHALL BE SUBJECT TO PRIOR APPROVAL OF THE COMPETENT AUTHORITY.
- MINOR SITE SPECIFIC ADJUSTMENTS MAY BE MADE BY THE EXECUTING AGENCY AS NEEDED, PROVIDED THAT THEY REMAIN IN COMPLIANCE WITH THE ESSENTIAL REQUIREMENTS OF ACCESS, LIGHT AND VENTILATION AS OUTLINED IN THE HARYANA BUILDING CODE-2017.
- IF THERE SHALL ANY PROBLEM DURING THE PROCESS OF LAYOUT AT ANY SITE THEN THAT PARTICULAR CASE BE SENT TO THIS OFFICE ALONGWITH T.S.S. AND ALL SITE DETAILS TO THIS OFFICE FOR PREPARATION OF THE LAYOUT PLAN.

(GOOD FOR CONSTRUCTION)
ALL DIMENSIONS ARE IN METERS
UNLESS OTHERWISE SPECIFIED

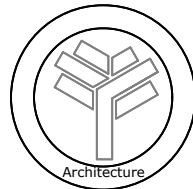

REVISIONS		
S.NO	DATE	DESCRIPTION

- NOTES:-**
- THIS DRAWING IS THE PROPERTY OF THE DEPARTMENT OF ARCHITECTURE, GOVT. OF HARYANA. THIS DRAWING MAY NOT BE ALTERED, COPIED, USED IN WHOLE OR IN PART WITHOUT THE PERMISSION OF THIS DEPARTMENT IN WRITING.
 - THE DISCREPANCY, IF ANY MUST BE BROUGHT TO THE NOTICE OF THE DEPARTMENT OF ARCHITECTURE HARYANA BEFORE ANY ACTION AT SITE.
 - PLINTH LEVEL OF BUILDING SHALL BE FIXED IN CONSULTATION WITH CONCERNED EXECUTIVE ENGINEER PUBLIC HEALTH TO AVOID FLOODING OF CAMPUS.
 - IT IS INTIMATED THAT VIDE MINUTES OF MEETING DATED 10-10-2024, DGHS HARYANA OFFICE HAS REQUESTED TO REVISE THE EARLIER APPROVED STANDARD DESIGN OF HEALTH WELLNESS CENTRE (HWC-SHC) HAVING A COVERED AREA OF 212 SQ.MTR TO 192 SQ.MTR TO REDUCE THE ESTIMATED COST OF CONSTRUCTION SO THAT HWC-SHC AT VARIOUS VILLAGES CAN BE CONSTRUCTED WITHIN THE BUDGET APPROVED UNDER 15TH FINANCE COMMISSION.
 - ACCORDINGLY, AS PER YOUR REQUEST, THE EARLIER APPROVED DESIGN OF HWC-SHC HAS BEEN REVISED BY REDUCING THE SIZES OF FEW ROOMS AS PER THE DISCUSSIONS HELD WITH THE DEPUTY DIRECTOR (CONSTRUCTION) O/O THE DGHS HARYANA AND CHIEF ENGINEER, PANCHAYATI RAJ, HARYANA DURING THEIR VISIT TO THIS OFFICE ON DATED 10.10.2024. THE COVERED AREA OF THE HWC-SHC HAS BEEN REDUCED TO 187.60 SQ.MTR.


AR. SANJEEV KUMAR (CHIEF ARCHITECT)	
AR. DEVENDER SINGH (SENIOR ARCHITECT)	
AR. LALIT KUMAR (ARCHITECT)	VACANT (ASSTT. ARCHITECT)

OFFICE OF THE
CHIEF ARCHITECT
HARYANA, CHANDIGARH

STANDARD HEALTH WELLNESS
CENTRE DESIGN-I WITHOUT LABOUR
ROOM AND RESIDENCES

TARSEM KUMAR (A.D.) DEALT BY:-	SUBHASH (A.A.) CHECKED BY:-
JOB NO 3152	SCALE NTS
DRG.NO 1C	DATE NOV. 2024

GROUND FLOOR PLAN,
ELEVATIONS & SECTION

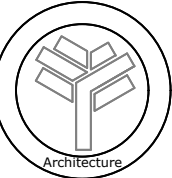

GENERAL NOTES:-

- THIS DRAWING IS THE PROPERTY OF THE DEPARTMENT OF ARCHITECTURE, GOVT. OF HARYANA. THIS DRAWING MAY NOT BE ALTERED, COPIED, USED IN WHOLE OR IN PART WITHOUT THE PERMISSION OF THIS DEPARTMENT IN WRITING.
- THE DISCREPANCY, IF ANY MUST BE BROUGHT TO THE NOTICE OF THE DEPARTMENT OF ARCHITECTURE HARYANA BEFORE ANY ACTION AT SITE.
- REVISED SPECIFICATIONS APPROVED BY THE ECONOMY COMMITTEE FOR P.H.C. / C.H.C. SHALL BE FOLLOWED.
- JOINERY MAY BE FABRICATED AFTER CONFIRMING THE SIZE OF PHYSICAL OPENING AT SITE.
- STANDARD SIZE OF PRESSED STEEL FRAME HAS BEEN MENTIONED IN THE DRAWINGS THESE SHALL BE AS PER APPROVED DNIT.

SPECIFICATION:-

- ALL DOOR AND WINDOW & VENTILATORS SHALL HAVE PRESSED STEEL FRAMES WITH STANDARD STEEL SECTIONS AS PER DETAILED DRAWINGS.
- SHUTTERS FOR ALL DOORS SHALL BE FLUSH SHUTTERS ISI MARKED.
- MS GRILL SHALL BE PROVIDED IN ALL EXTERNAL WINDOWS & VENTILATORS.
- EXHAUST FANS SHALL BE PROVIDED IN ALL TOILETS.
- OPENINGS FOR AIR CONDITIONER / DESERT COOLER SHALL BE KEPT EXACT AT SITE IN CONSULTATION WITH CONCERNED XEN, ELECT. DIVN. P.W.D.(B&R) BR.
- ENTRY DOORS SHALL HAVE FLUSH & WIREMESH SHUTTERS BOTH.

AR. SANJEEV KUMAR
(CHIEF ARCHITECT)

AR. DEVENDER SINGH
(SENIOR ARCHITECT)

AR. LALIT KUMAR
(ARCHITECT)

VACANT
(ASSTT. ARCHITECT)

OFFICE OF THE
CHIEF ARCHITECT
HARYANA, CHANDIGARH

STANDARD HEALTH WELLNESS CENTRE
DESIGN-I WITHOUT LABOUR ROOM AND
RESIDENCES

TARSEM KUMAR (A.D.)
DEALT BY:-

SUBHASH (A.A.)
CHECKED BY:-

JOB NO
3152

SCALE
NTS

DRG.NO
4C

DATE
NOV. 2024

DETAIL OF JOINERY

SCHEDULE OF JOINERY

S.NO.	TYPE	SIZE	CILL	TOP	REMARKS
1	D/G	3.76 X 2.60	-	2.60	D=2.0 SOLID FLUSH DOOR WITH WIRE MESH SHUTTER
2	D1/G1	1.80 X 2.60	-	2.60	D1=1.06 SOLID FLUSH DOOR WITH WIRE MESH SHUTTER
3	D1	1.06 X 2.15	-	2.15	
4	D2	0.90 X 2.15	-	2.15	
5	W	1.80 X 1.70	0.90	2.60	
6	W-A	1.80 X 1.54	1.06	2.60	
7	W1	1.32 X 1.70	0.90	2.60	
8	V	0.90 X 0.45	2.15	2.60	

(GOOD FOR CONSTRUCTION)

NOTE:- ALL DIMENSIONS ARE IN METERS
UNLESS OTHERWISE SPECIFIED

