
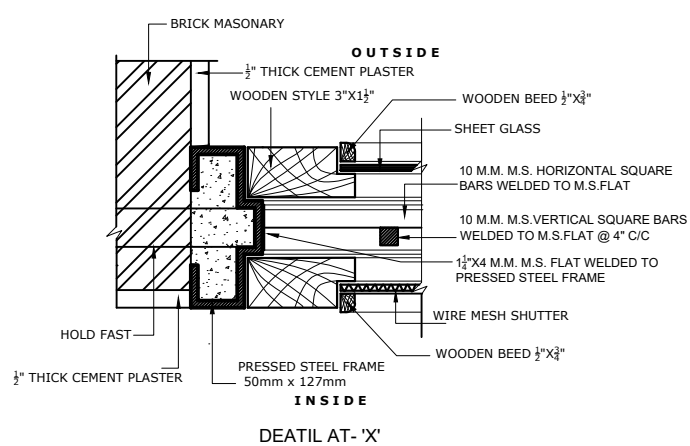
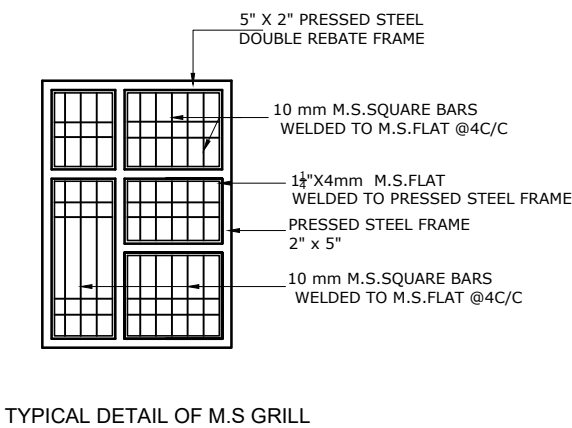
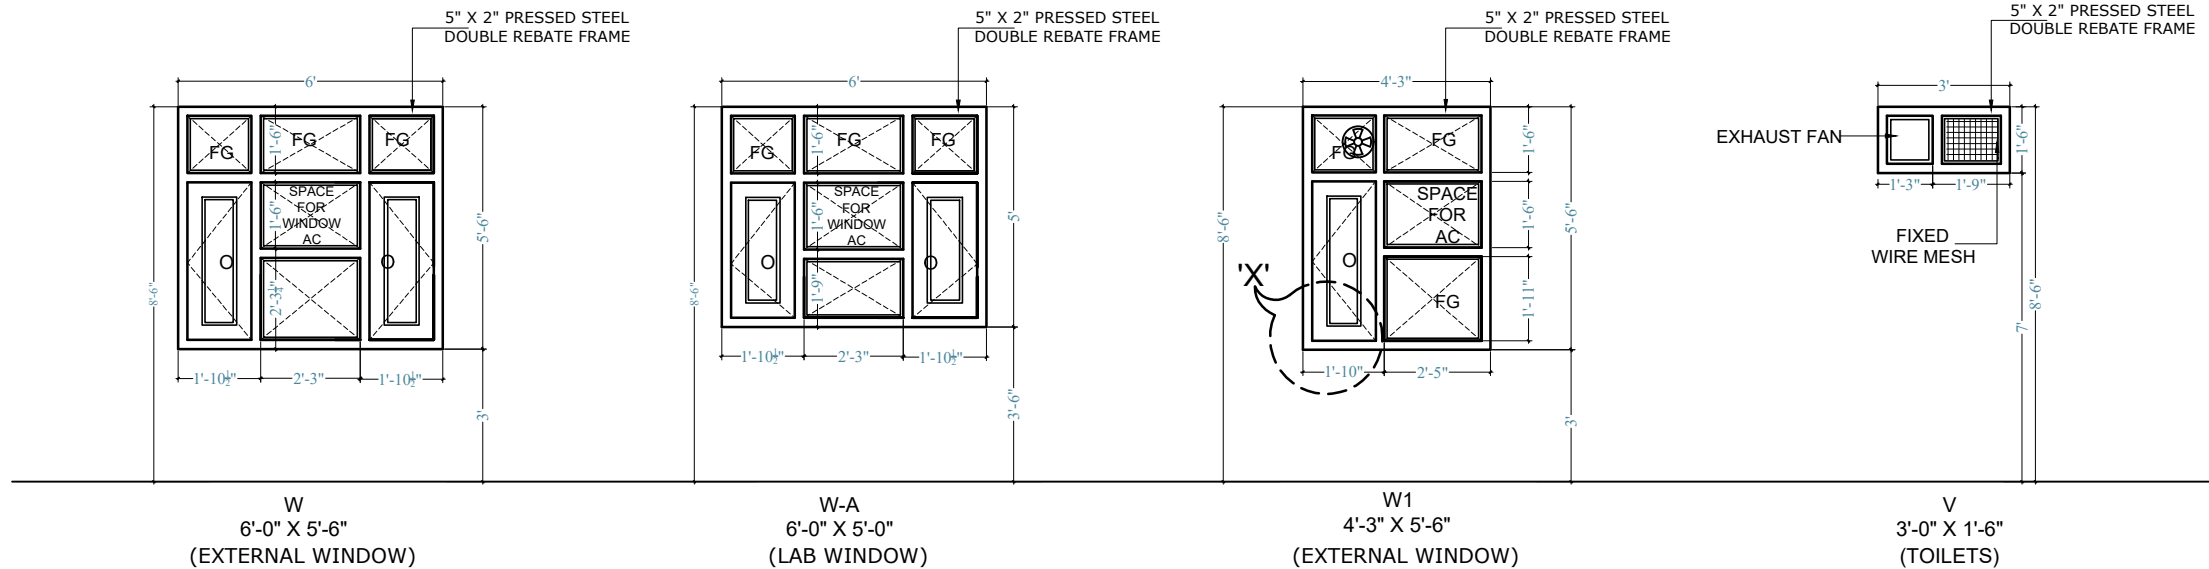
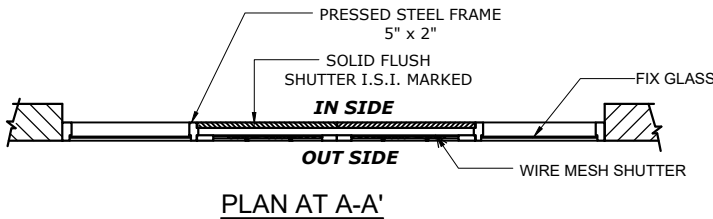


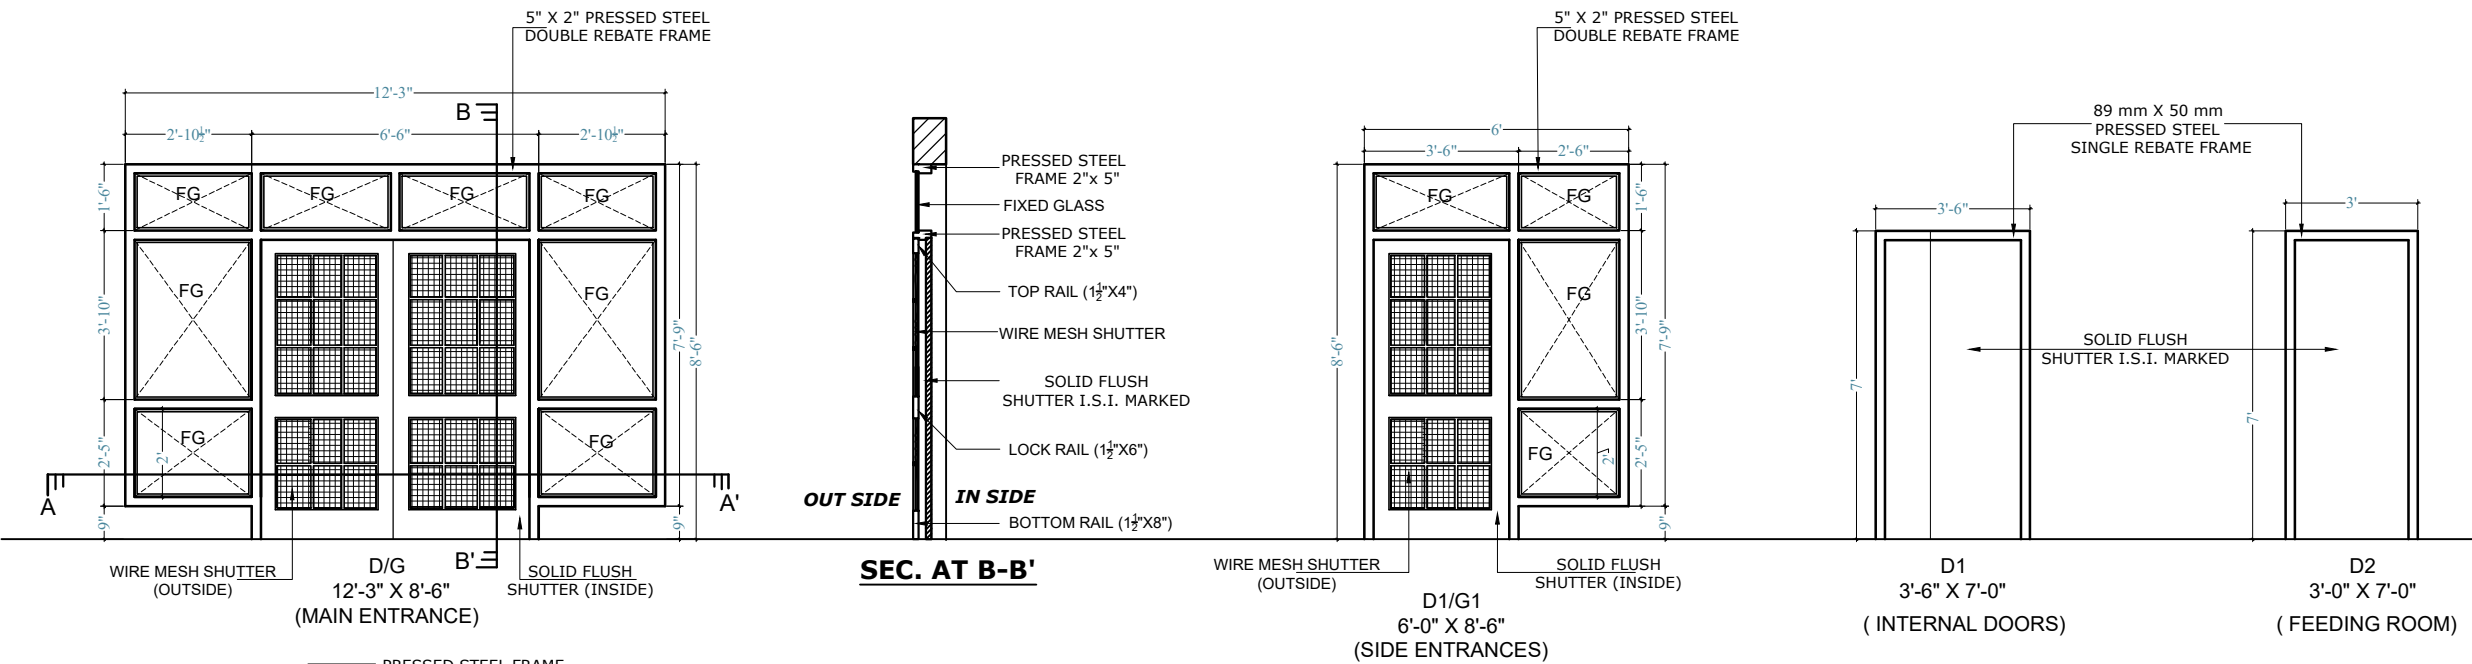

SCHEDULE OF JOINERY					
S.NO.	TYPE	SIZE	CILL	TOP	REMARKS
1	D/G	12'-3" X 8'-6"	-	2.60	D=6'-6" SOLID FLUSH DOOR WITH WIRE MESH SHUTTER
2	D1/G1	6'-0" X 8'-6"	-	8'-6"	D1=3'-6" SOLID FLUSH DOOR WITH WIRE MESH SHUTTER
3	D1	3'-6" X 7'-0"	-	2.15	
4	D2	3'-0" X 7'-0"	-	2.15	
5	W	6'-0" X 5'-6"	3'-0"	8'-6"	
6	W-A	6'-0" X 5'-0"	3'-6"	8'-6"	
7	W1	4'-3" X 5'-6"	3'-0"	8'-6"	
8	V	3'-0" X 1'-6"	7'-0"	8'-6"	

127 mm X 50 mm
PRESSED STEEL
DOUBLE REBATE FRAME

(GOOD FOR CONSTRUCTION)
NOTE:- ALL DIMENSIONS ARE IN METERS
UNLESS OTHERWISE SPECIFIED