


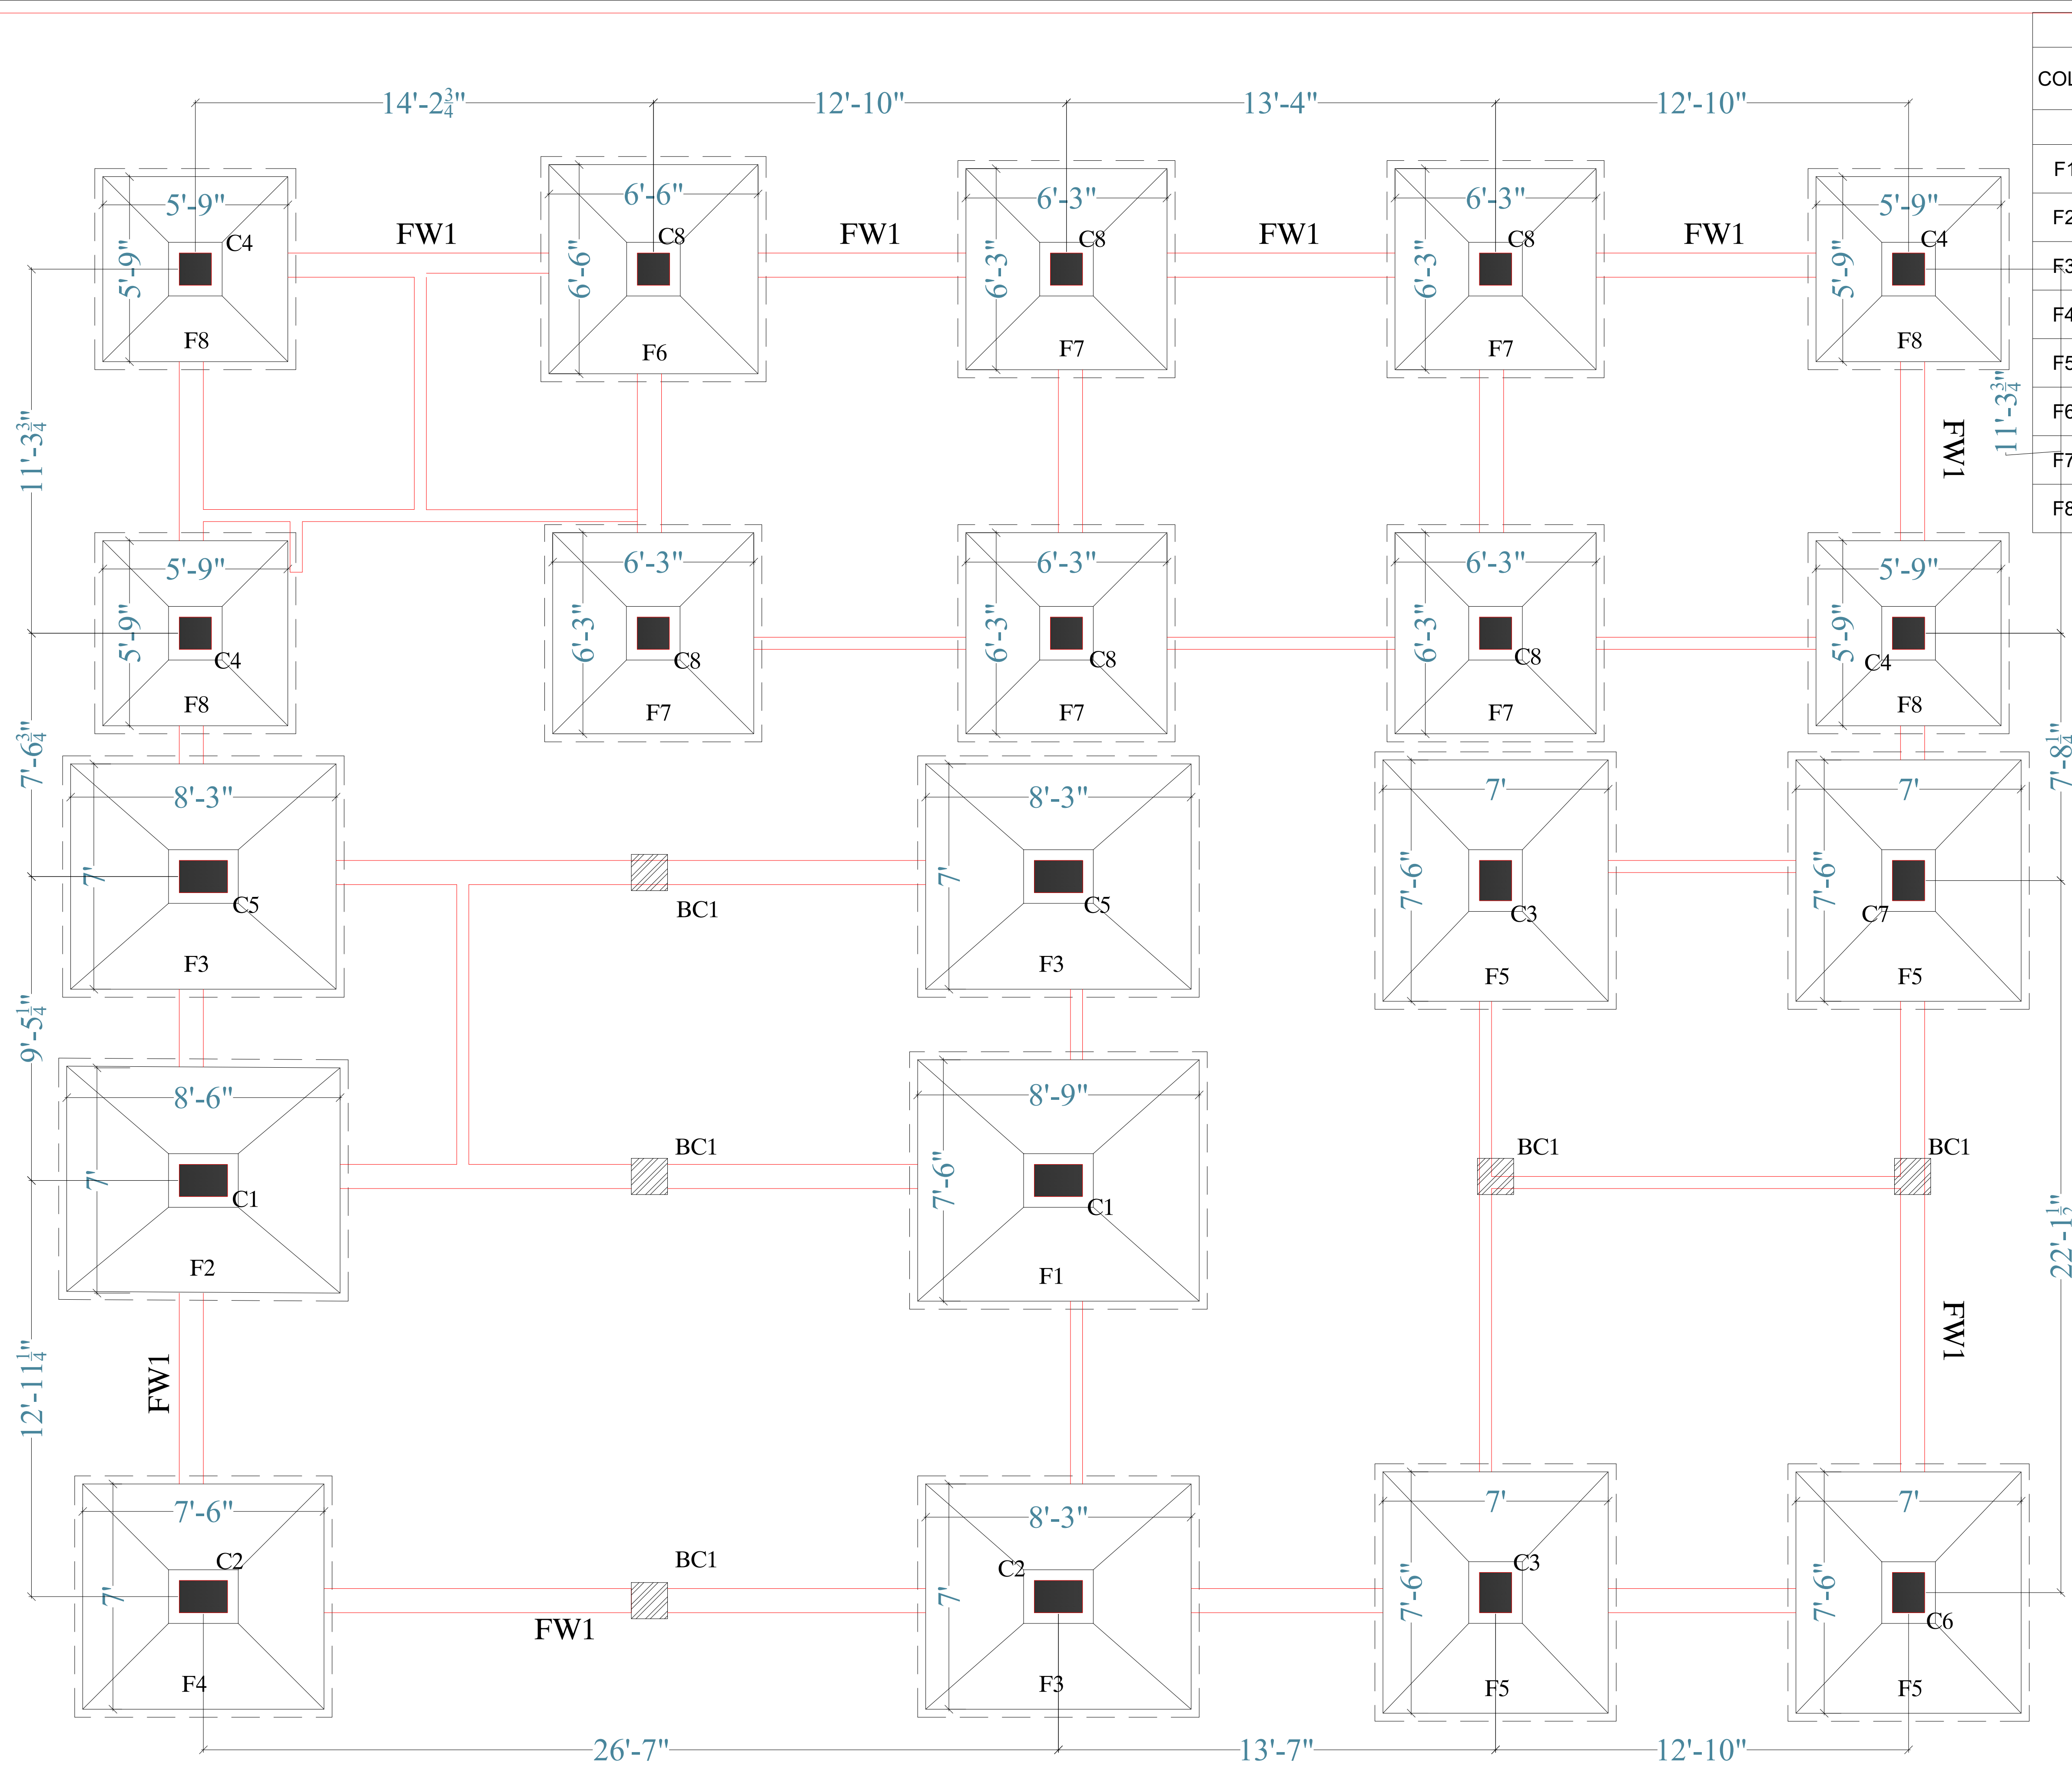

SCHEDULE FOR DETAIL OF COLUMN FOOTING									
COLUMN FOOTING			DIMENSION			REINFORCEMENT FOR FOOTING		PEDESTAL DIMENSION	
	L	B	H1	H1	D	R	S	L1	B1
F1	8'-9"	7'-6"	9"	1'-9"	5'-0"	10Ø TOR @6" C/C	10Ø TOR @6" C/C	2'-6"	2'-0"
F2	8'-6"	7'-0"	9"	1'-9"	5'-0"	10Ø TOR @6" C/C	10Ø TOR @6" C/C	2'-6"	2'-0"
F3	8'-3"	7'-0"	9"	1'-9"	5'-0"	10Ø TOR @6" C/C	10Ø TOR @6" C/C	2'-6"	2'-0"
F4	7'-6"	7'-0"	9"	1'-9"	5'-0"	10Ø TOR @6" C/C	10Ø TOR @6" C/C	2'-6"	2'-0"
F5	7'-0"	7'-6"	9"	1'-9"	5'-0"	10Ø TOR @6" C/C	10Ø TOR @6" C/C	2'-3"	2'-0"
F6	6'-6"	6'-6"	9"	1'-9"	5'-0"	10Ø TOR @6" C/C	10Ø TOR @6" C/C	2'-0"	2'-0"
F7	6'-3"	6'-3"	9"	1'-9"	5'-0"	10Ø TOR @6" C/C	10Ø TOR @6" C/C	2'-0"	2'-0"
F8	5'-9"	5'-9"	9"	1'-9"	5'-0"	10Ø TOR @6" C/C	10Ø TOR @6" C/C	2'-0"	2'-0"

FOUNDATION LAYOUT PLAN