


COLUMN LAYOUT

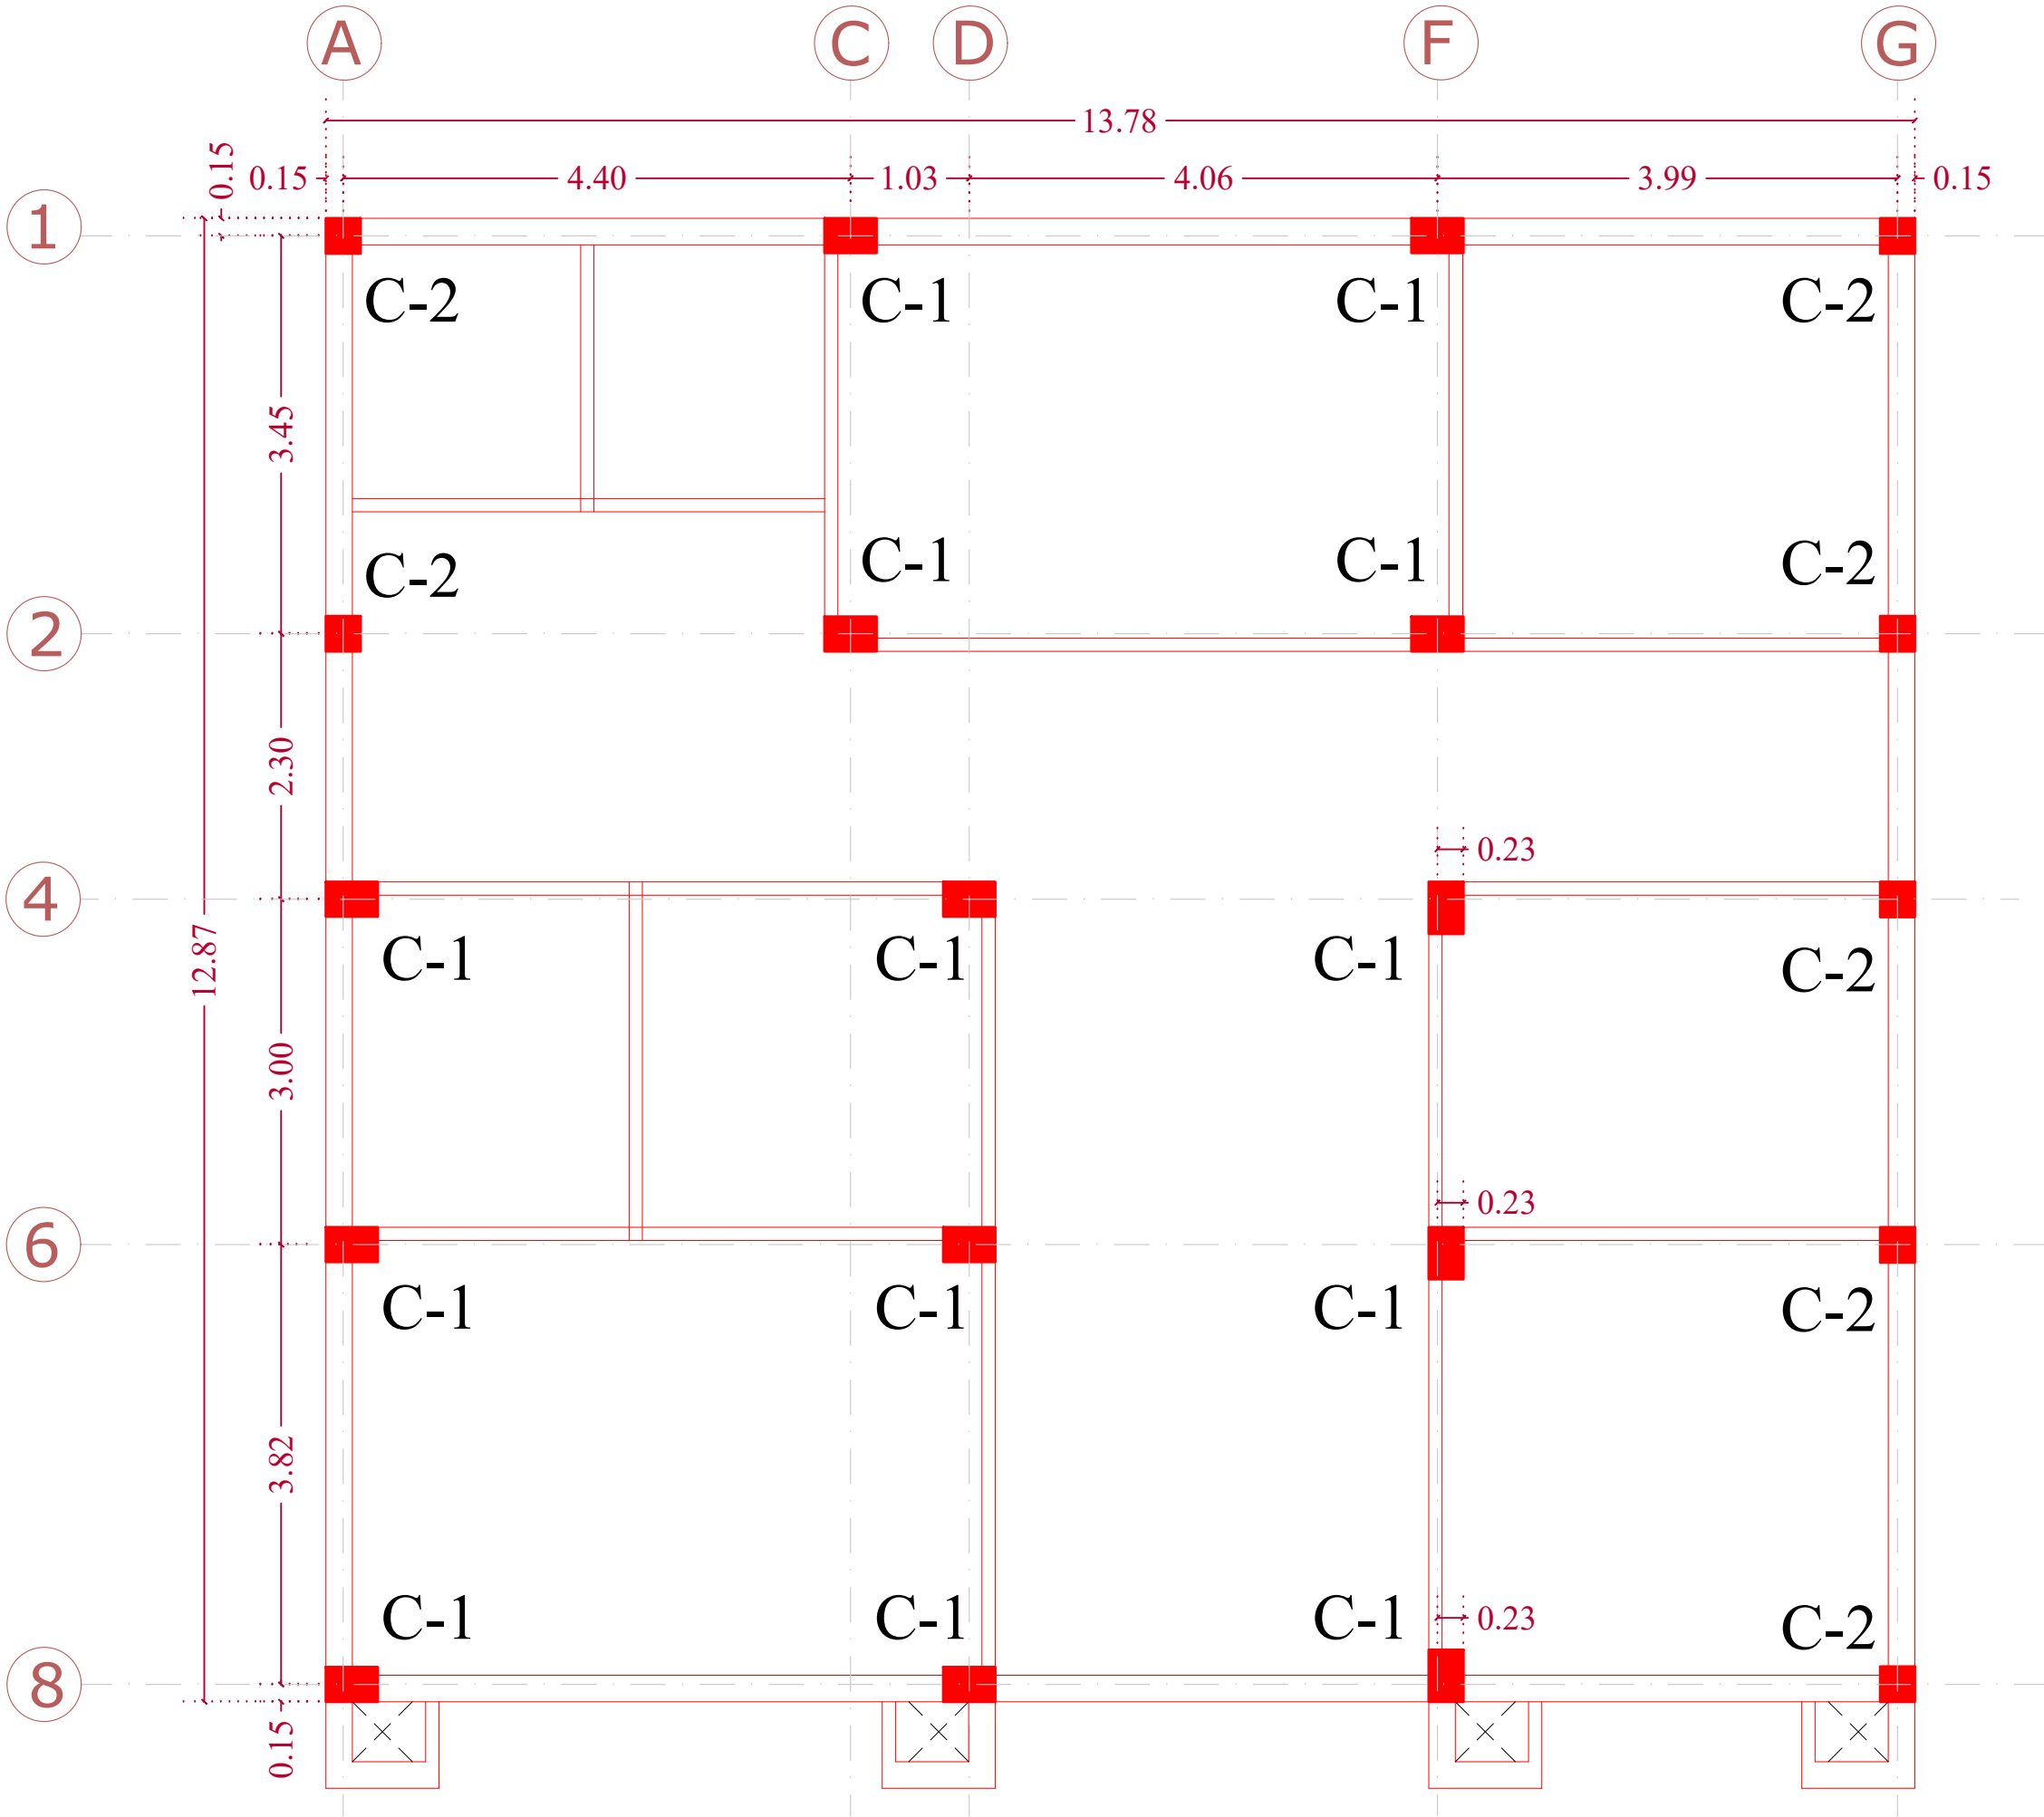

NOTE:-
1. CHECK ALL DIMENSIONS AND LEVELS WITH ARCHITECTURAL DRAWING.
2. THERE WILL BE NO FUTURE EXPANSION ABOVE GROUND FLOOR.

SUBMITTED BY :-

D.B.S.C.R.
GOVT. POLYTECHNIC
SAMPLA

CLIENT : THE EXECUTIVE ENGINEER
PANCHAYATI RAJ DISTRICT JIND
HARYANA

PROJECT:

DRAWING TITLE:
COLUMN LAYOUT

☐ CONCEPTUAL DRG☐ WORKING DRG

☐ SCHEMATIC DRG☐ AS BUILT DRG

QUANTITY.- 1

NOTE -

NOTE - DIMENSIONS HAS TO BE
CHECKED FROM SITE.

DISPATCH DATE: 03/09/2025

Scale: NTS

Drawn By:

Checked By:

NORTH

ISSUES AND REVISIONS

NO.	DATE	REMARKS
1		
2		
3		



NOTE:-
*This drawing is the property of 7 Frames Designs and shall not be copied or used in any way without their prior permission.
*All dimension are as indicated unless otherwise mentioned.
*Drawing not to be scaled, dimensions to be followed.
*All discrepancies to be brought to the notice of the designer before execution and his design to be final.
*This drawing is to be read in conjunction with detail scale drawings and other relevant drawing.

DETAIL OF COLUMNS								
SR. NO.	COL. NO.	SIZE	MIX	TIES REFER NOTE NO. 10		REINF. FROM FOUNDATION TO TERRACE	TIES	REMARKS
				Z - PORTION	Y - PORTION			
1.	C-1	0.30 x 0.45	M - 25	8 MM Φ @ 100MM C/C.	8 MM Φ @ 150MM C/C.	0.300 0.450 4-20 MM Φ 8-16 MM Φ 1 2 3 4		
2.	C-2	0.30 x 0.30	M - 25	8 MM Φ @ 100MM C/C.	8 MM Φ @ 150MM C/C.	0.300 0.300 8-16 MM Φ 1 2 3		


COLUMN DETAIL

PRINT THIS TYPE OF DRAWING ON A3 PAGE SIZE


NOTE:- *This drawing is the property of 7 Frames Designs and shall not be copied or used in any way without their prior permission. *All dimension are as indicated unless otherwise mentioned. *Drawing not to be scaled, dimensions to be followed. *All discrepancies to be brought to the notice of the designer before execution and his design to be final. *This drawing is to be read in conjunction with detail scale drawings and other relevant drawing.	NOTE - DIMENSIONS HAS TO BE CHECKED FROM SITE.			CLIENT : THE EXECUTIVE ENGINEER PANCHAYATI RAJ DISTRICT JIND HARYANA PROJECT: DRAWING TITLE: COLUMN DETAIL ☐ CONCEPTUAL DRG ☐ WORKING DRG ☐ SCHEMATIC DRG ☐ AS BUILT DRG QUANTITY.- 1	SUBMITTED BY :- D.B.S.C.R. GOVT. POLYTECHNIC SAMPLA
	DISPATCH DATE: 03/09/2025				
	Scale: NTS	NORTH			
	Drawn By:				
	Checked By:				
	ISSUES AND REVISIONS				
	NO.	DATE	REMARKS		
	1				
	2				
	3				

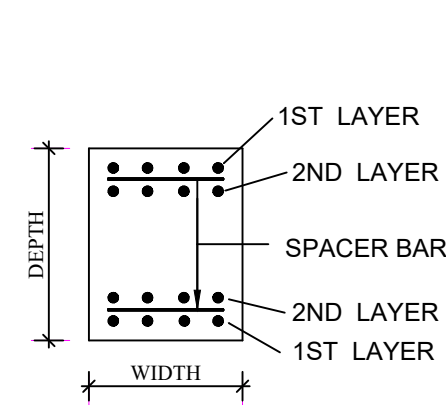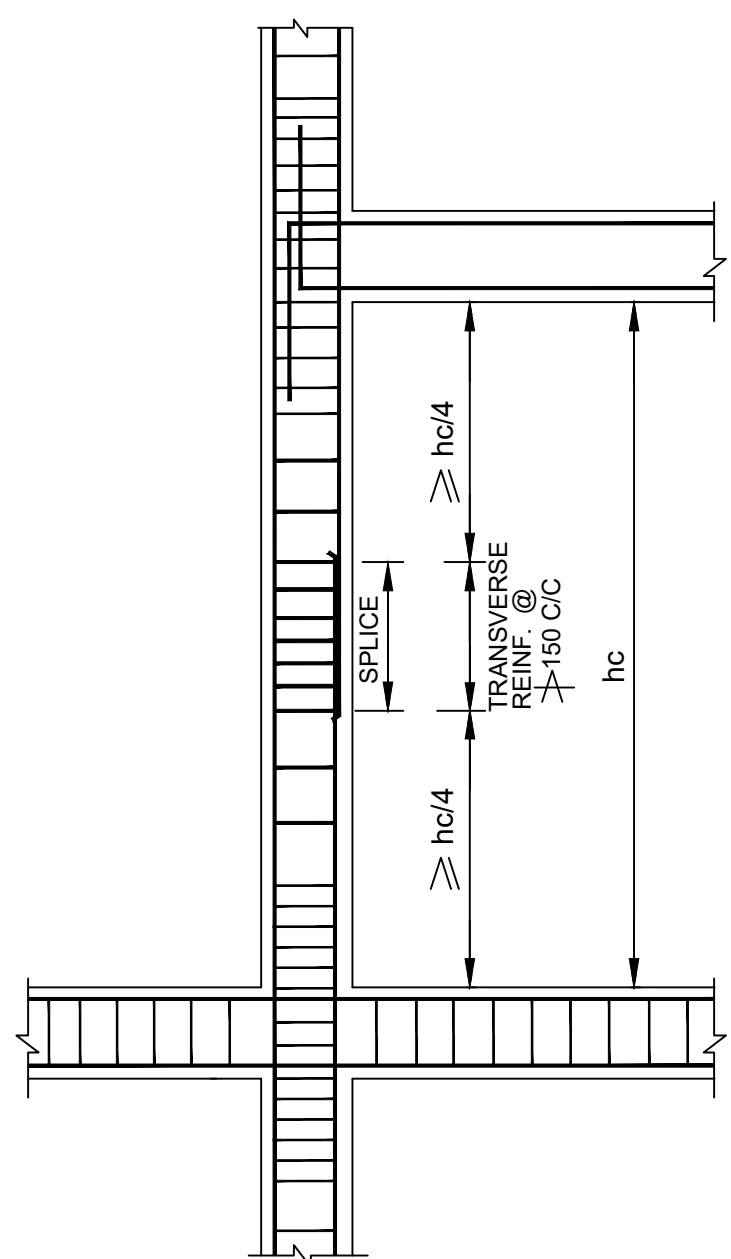


TYP. SEC. OF MAIN BEAM
(STIRRUPS NOT SHOWN)

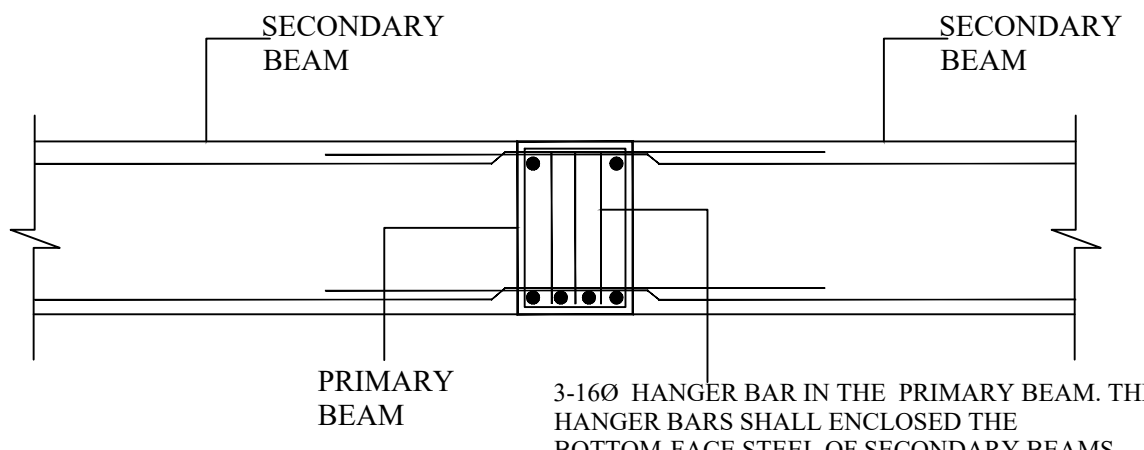


TYPICAL JUNCTION DETAILS
OF MAIN & SECONDARY BEAMS

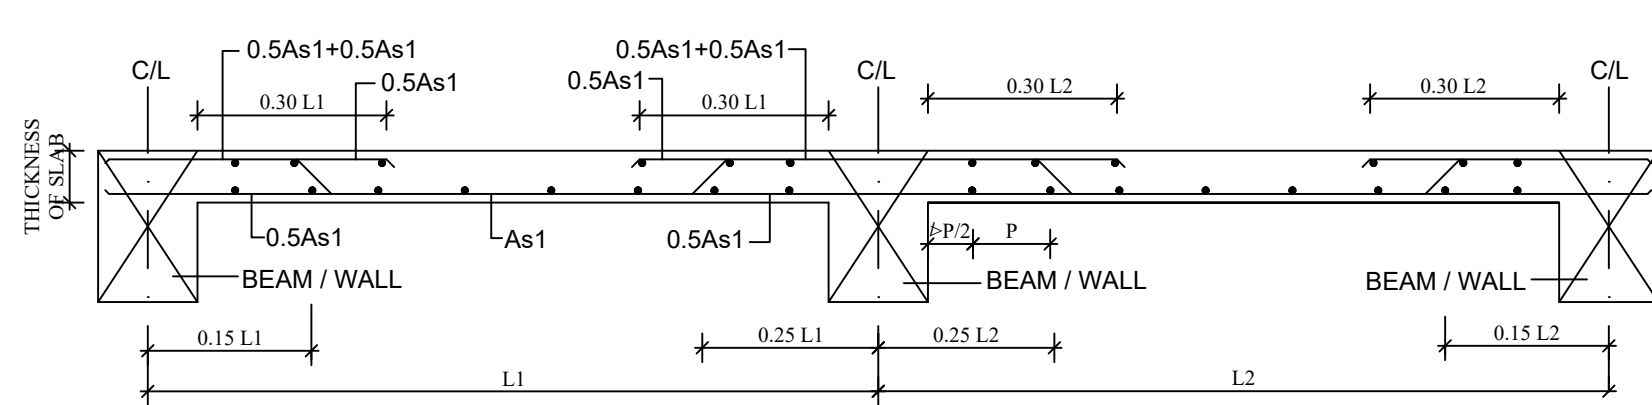

TYPICAL SECTION THROUGH SLAB

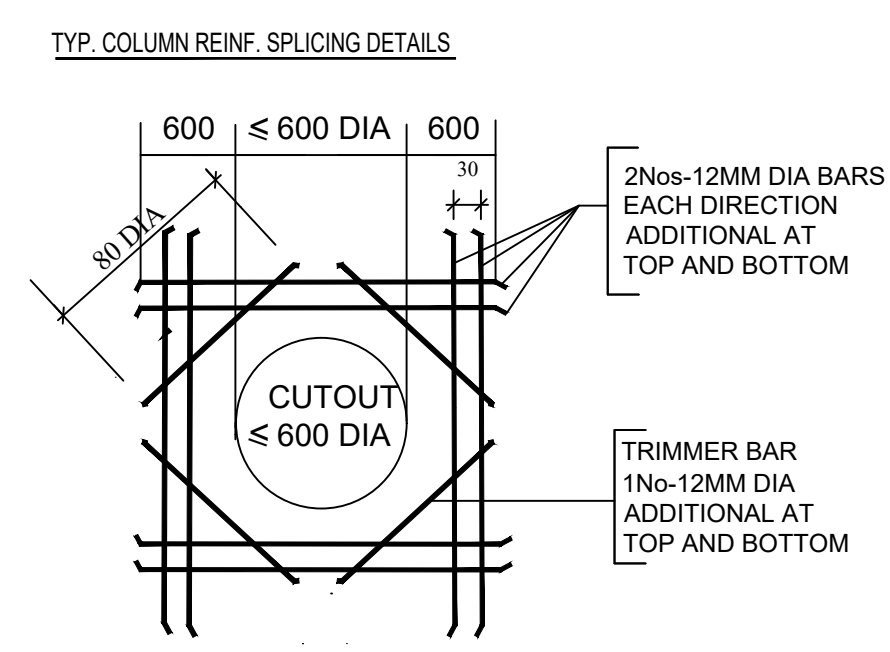

ADDITIONAL REINFORCEMENT AROUND CIRCULAR CUT-OUT (OPENING) IN SLAB

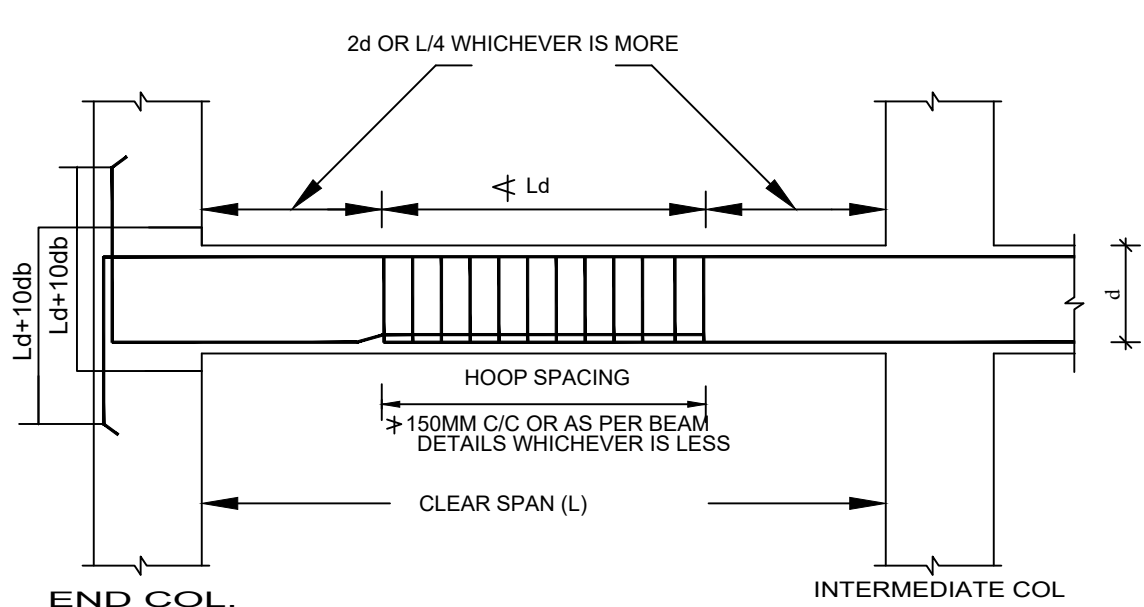

TYPICAL DETAILS OF LAP & SPLICE IN BEAM

Ld = DEVELOPMENT LENGTH
d = EFFECTIVE DEPTH OF BEAM

SUBMITTED BY:-

D.B.S.C.R
GOVT POLYTECHNIC
SAMPLA

CLIENT : THE EXECUTIVE ENGINEER
PANCHAYATI RAJ DISTRICT JIND
HARYANA

PROJECT:

DRAWING TITLE: TYPICAL DETAIL_II

☐ CONCEPTUAL DRG	☒ WORKING DRG
☐ SCHEMATIC DRG	☐ AS BUILT DRG

QUANTITY.- 1

NOTE -

DESIGN NO.-1

NOTE - DIMENSIONS HAS TO BE
CHECKED FROM SITE.

DISPATCH DATE: 17/07/2025

Scale: NTS	NORTH
Drawn By:	
Checked By:	

ISSUES AND REVISIONS		
NO.	DATE	REMARKS
1		
2		
3		

NOTE:-
*This drawing is the property of 7 Frames Designs and shall not be copied or used in any way without their prior permission.
*All dimension are as indicated unless otherwise mentioned.
*Drawing not to be scaled, dimensions to be followed.
*All discrepancies to be brought to the notice of the designer before execution and his design to be final.
*This drawing is to be read in conjunction with detail scale drawings and other relevant drawing.

TYPICAL DETAIL_II

PRINT THIS TYPE OF DRAWING ON A3 PAGE SIZE

SUBMITTED BY :-

D.B.S.C.R.
GOVT. POLYTECHNIC
SAMPLA

CLIENT : THE EXECUTIVE ENGINEER
PANCHAYATI RAJ DISTRICT JIND
HARYANA

PROJECT:

DRAWING TITLE:
FOOTING LAYOUT

☐ CONCEPTUAL DRG	☐ WORKING DRG
☐ SCHEMATIC DRG	☐ AS BUILT DRG

QUANTITY.- 1

NOTE -

NOTE - DIMENSIONS HAS TO BE
CHECKED FROM SITE.

DISPATCH DATE: 03/09/2025

Scale: NTS

NORTH

Drawn By:

Checked By:

ISSUES AND REVISIONS

NO.	DATE	REMARKS
1		
2		
3		

NOTE:-


*This drawing is the property of 7 Frames Designs and shall not be copied or used in any way without their prior permission.

*All dimension are as indicated unless otherwise mentioned.

*Drawing not to be scaled, dimensions to be followed.

*All discrepancies to be brought to the notice of the designer before execution and his design to be final.

*This drawing is to be read in conjunction with detail scale drawings and other relevant drawing.

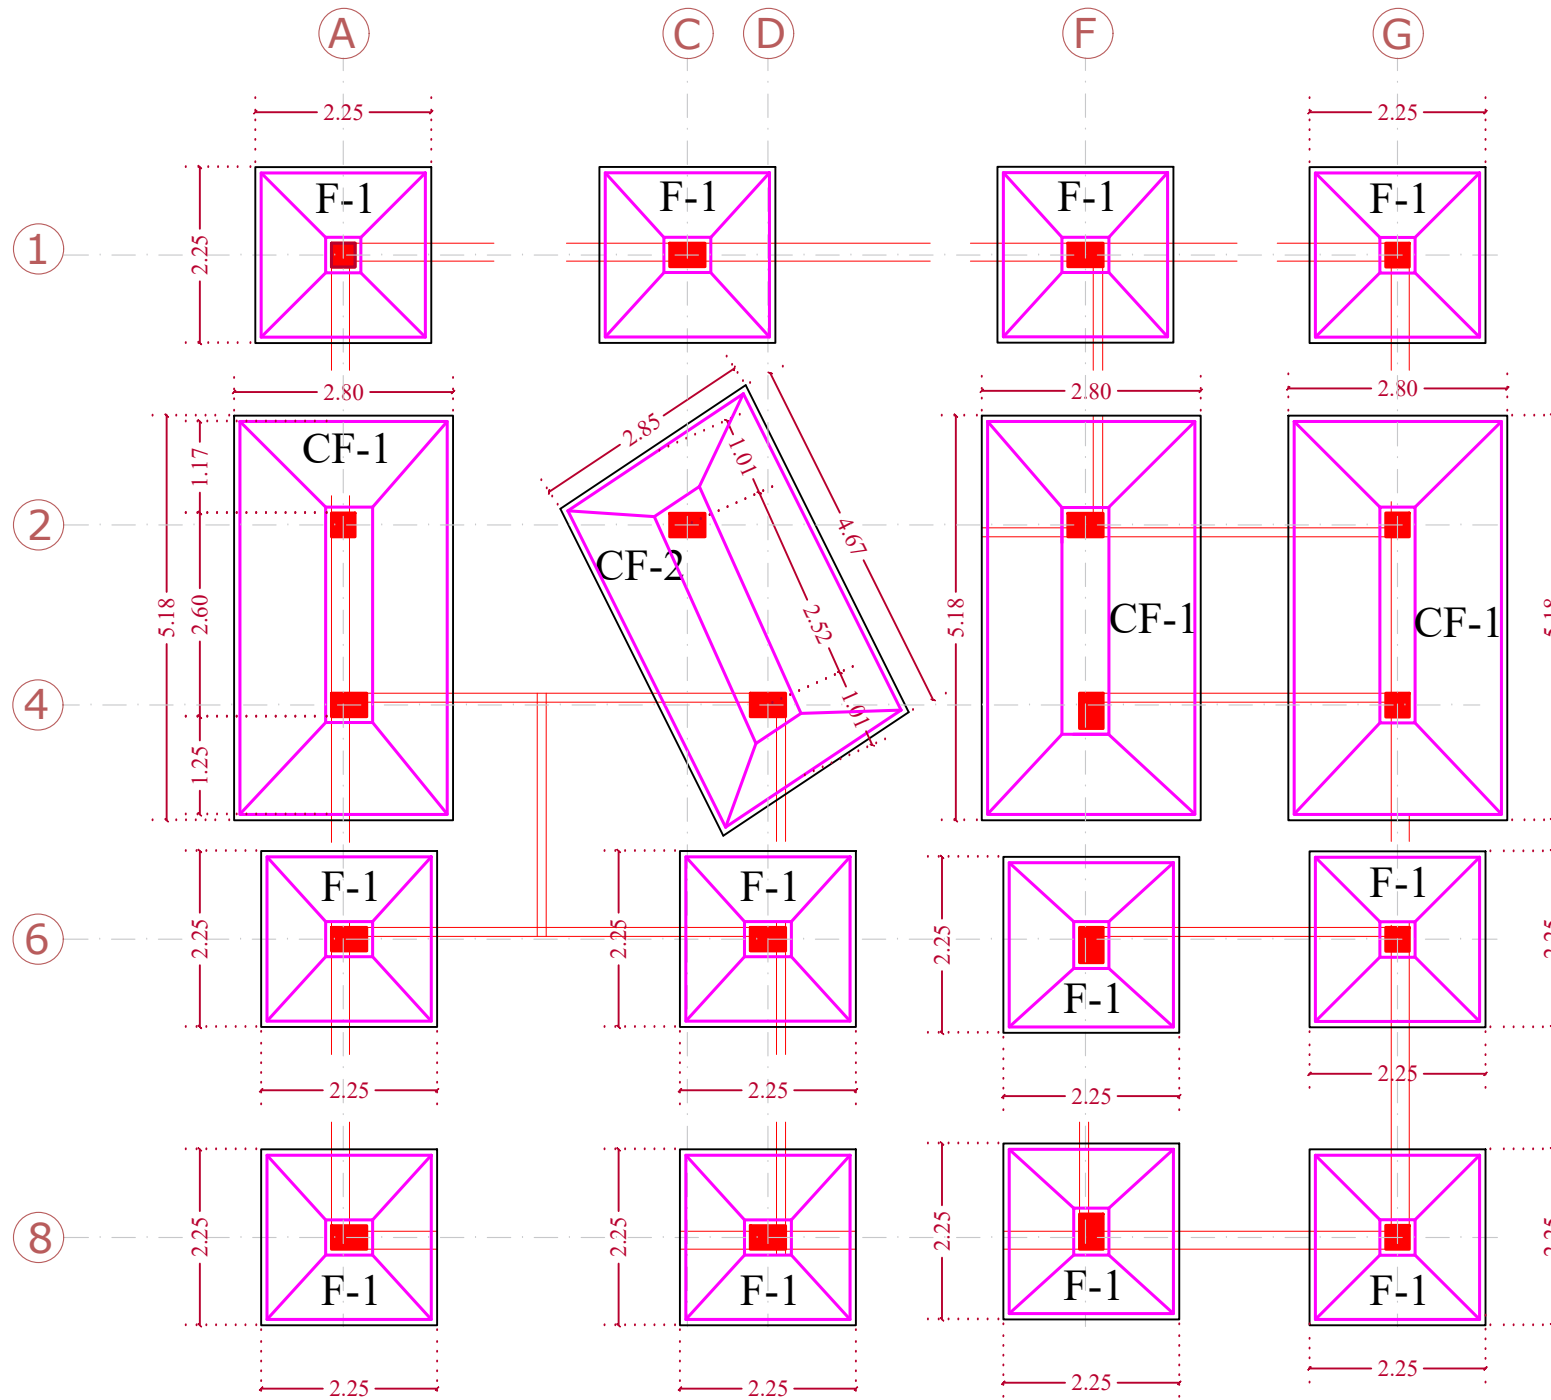


NOTE:-

1. CHECK ALL DIMENSIONS AND LEVELS WITH ARCHITECTURAL DRAWING.
2. THERE WILL BE NO FUTURE EXPANSION ABOVE GROUND FLOOR.


FOOTING LAYOUT

SCHEDULE FOR DETAIL OF COLUMN FOOTING

COLUMN FOOTING P.C.C SIZE			COLUMN FOOTING R.C.C SIZE		THIKNESS OF FOOTING			REINFORCEMENT FOR FOOTING		PEDESTAL DIMENSION		
L1		B1	L	B	H1	H2		R	S	P1	P2	P
F1	2.25	2.25	2.10	2.10	300	600		12MMØ @150mmC/C	12MMØ @150mmC/C	600	450	300
CF-1	5.18	2.80	5.02	2.65	300	600		12MMØ @150mmC/C	12MMØ @150mmC/C	450	450	300
CF-2	4.67	2.85	4.52	2.70	300	600		12MMØ @150mmC/C	12MMØ @150mmC/C	450	450	300

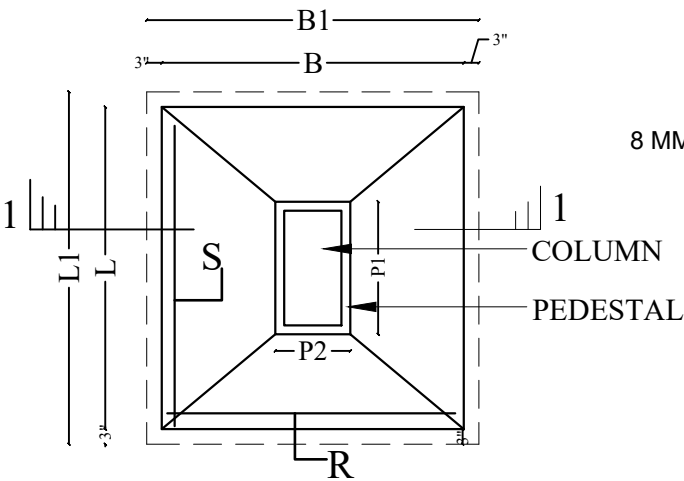

TYPICAL PLAN OF COLUMN FOOTING

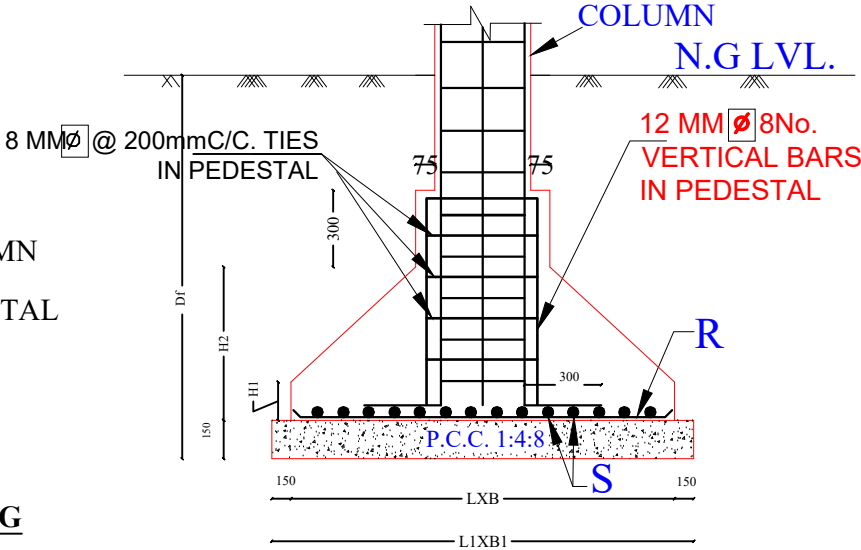


FOOTING DETAIL

SECTION AT 1-1

PRINT THIS TYPE OF DRAWING ON A3 PAGE SIZE

NOTE:- *This drawing is the property of 7 Frames Designs and shall not be copied or used in any way without their prior permission. *All dimension are as indicated unless otherwise mentioned. *Drawing not to be scaled, dimensions to be followed. *All discrepancies to be brought to the notice of the designer before execution and his design to be final. *This drawing is to be read in conjunction with detail scale drawings and other relevant drawing.	NOTE - DIMENSIONS HAS TO BE CHECKED FROM SITE.		NOTE :-	CLIENT : THE EXECUTIVE ENGINEER PANCHAYATI RAJ DISTRICT JIND HARYANA		SUBMITTED BY :- D.B.S.C.R. GOVT. POLYTECHNIC SAMPLA		
	DISPATCH DATE: 03/09/2025			PROJECT:				
	Scale: NTS			DRAWING TITLE:				
	Drawn By:			FOOTING DETAIL				
	Checked By:			QUANTITY.- 1				
ISSUES AND REVISIONS			CONCEPTUAL DRG		WORKING DRG			
NO. DATE REMARKS			SCHEMATIC DRG		AS BUILT DRG			
1								
2								
3								

PLINTH BEAM LAYOUT

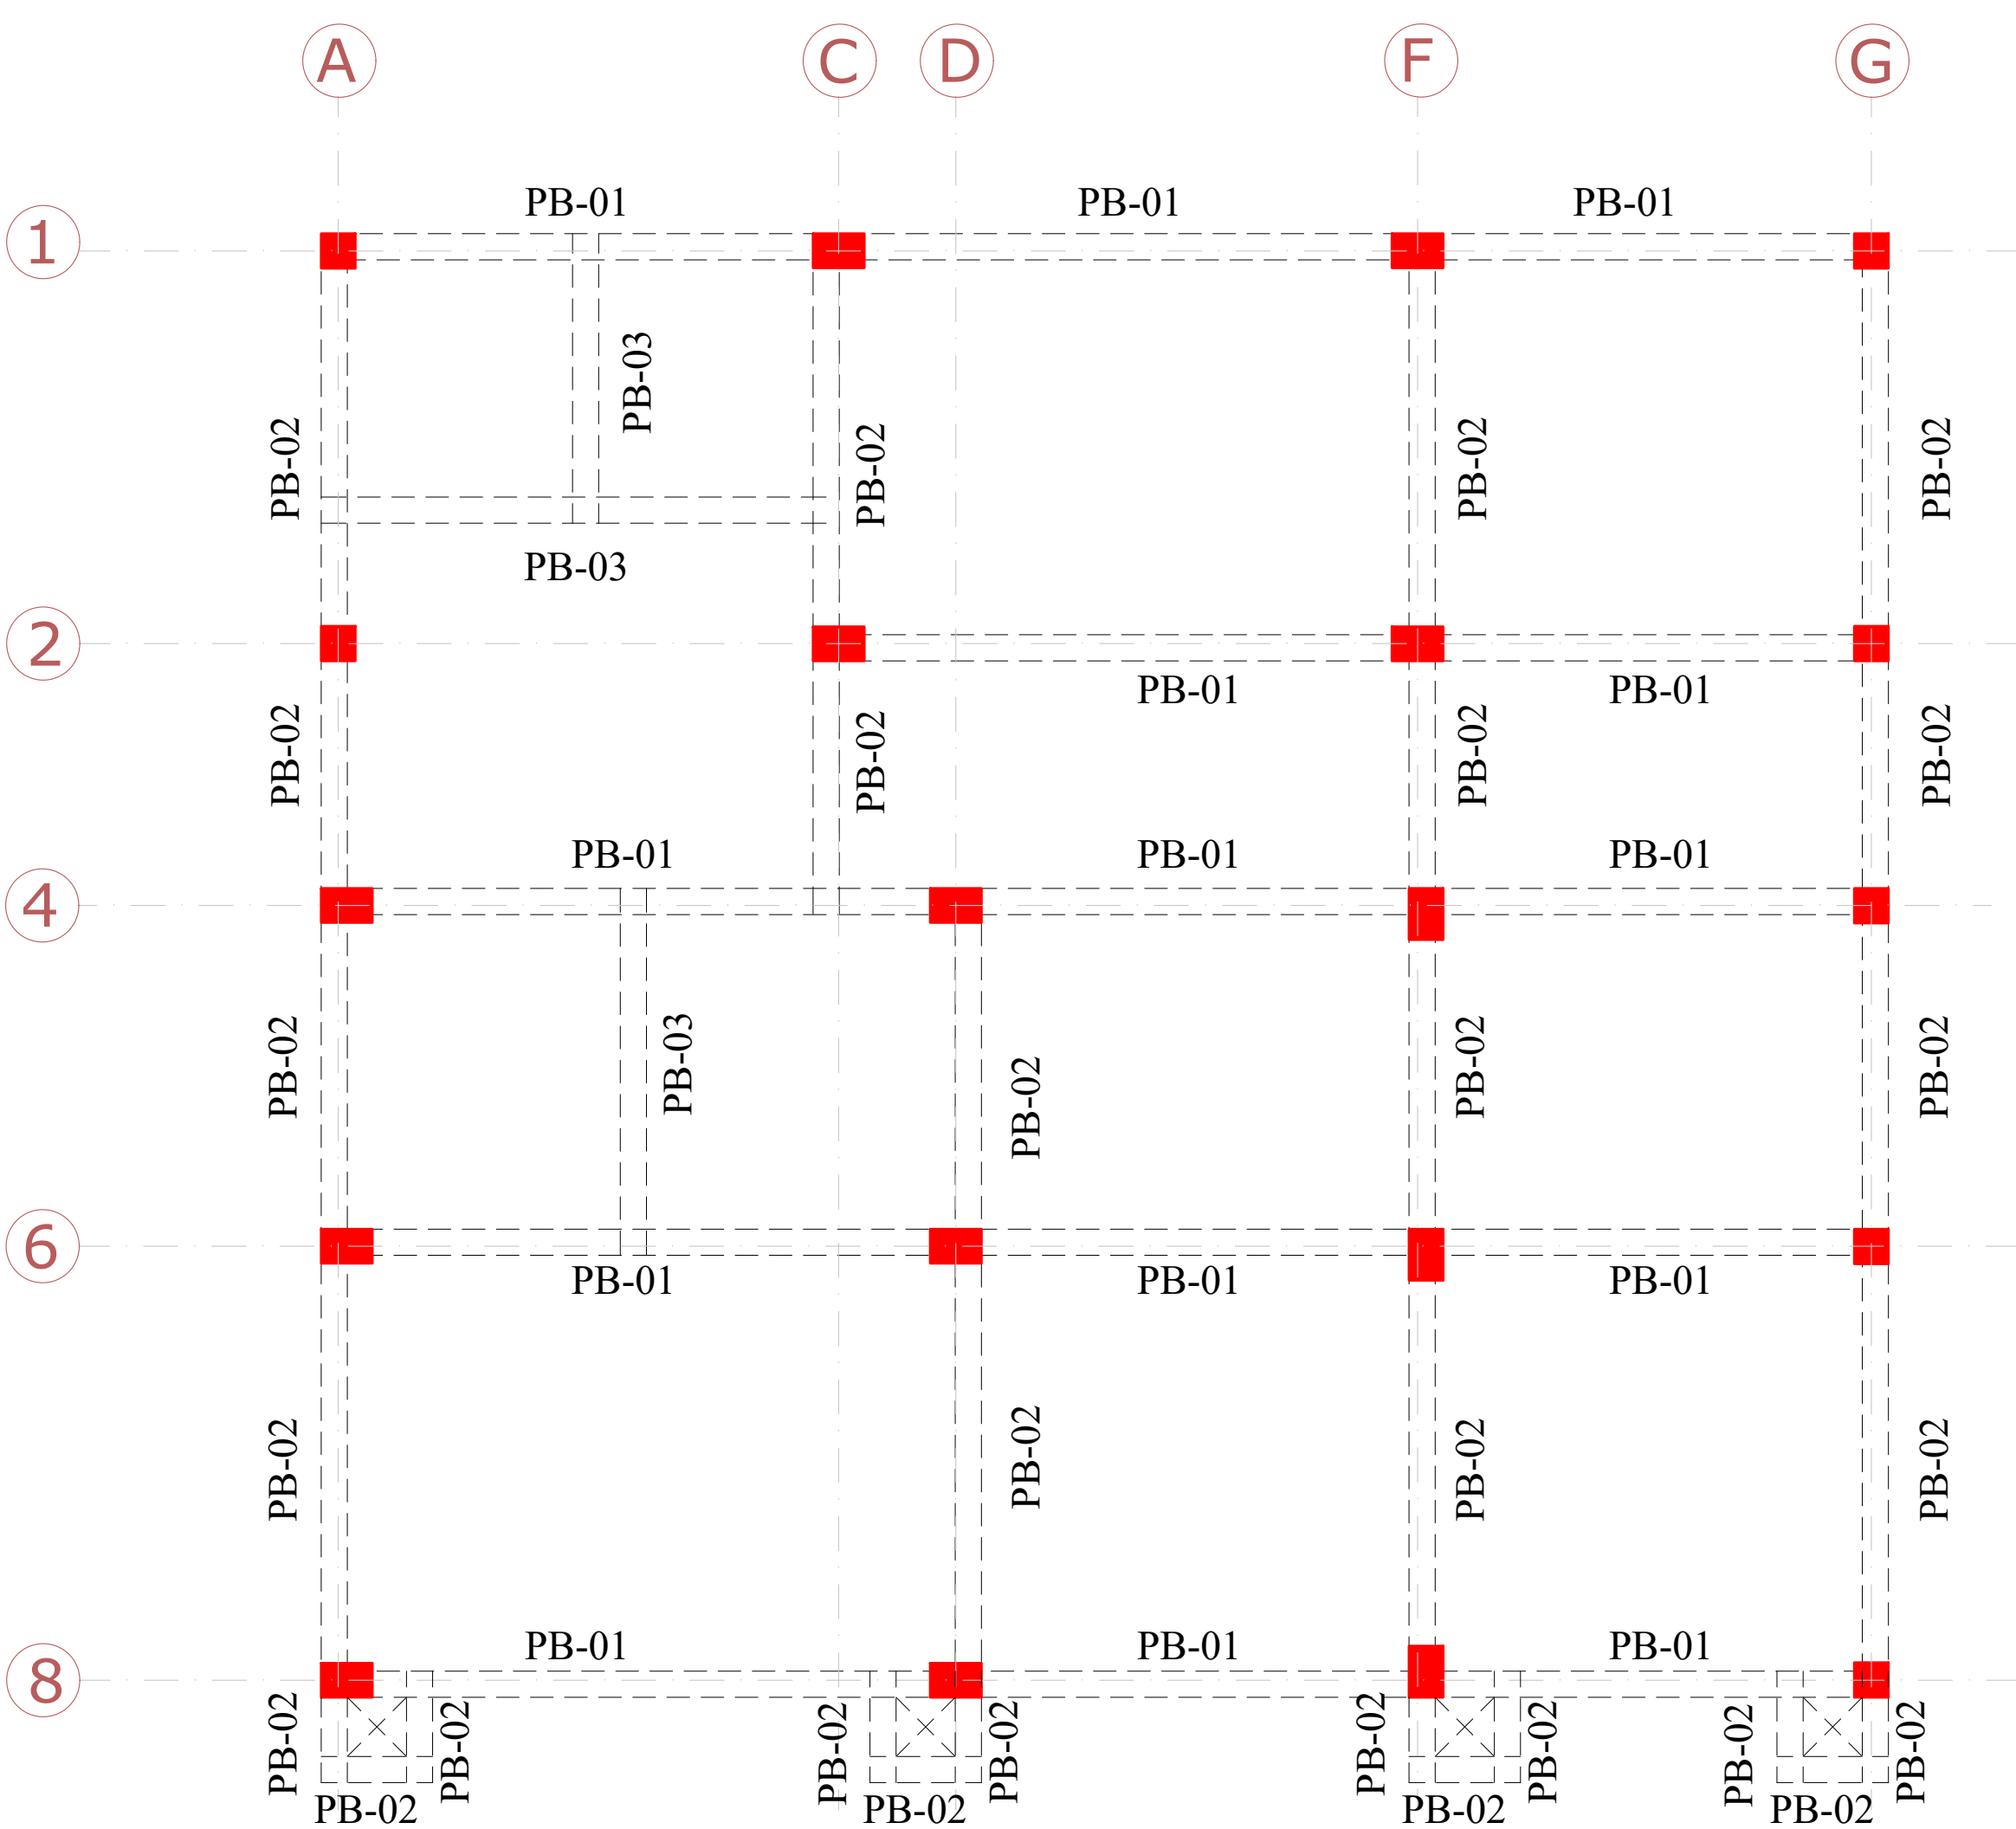

NOTE:-
1. CHECK ALL DIMENSIONS AND LEVELS WITH ARCHITECTURAL DRAWING.
2. THERE WILL BE NO FUTURE EXPANSION ABOVE GROUND FLOOR.

SUBMITTED BY :-

D.B.S.C.R.
GOVT. POLYTECHNIC
SAMPLA

CLIENT : THE EXECUTIVE ENGINEER
PANCHAYATI RAJ DISTRICT JIND
HARYANA

PROJECT:

DRAWING TITLE:
PLINTH BEAM LAYOUT

☐ CONCEPTUAL DRG	☐ WORKING DRG
☐ SCHEMATIC DRG	☐ AS BUILT DRG

QUANTITY.- 1

NOTE -



NOTE - DIMENSIONS HAS TO BE
CHECKED FROM SITE.

DISPATCH DATE: 03/09/2025




Scale: NTS	NORTH
Drawn By:	
Checked By:	

ISSUES AND REVISIONS		
NO.	DATE	REMARKS
1		
2		
3		

NOTE:-
*This drawing is the property of 7 Frames Designs and shall not be copied or used in any way without their prior permission.
*All dimension are as indicated unless otherwise mentioned.
*Drawing not to be scaled, dimensions to be followed.
*All discrepancies to be brought to the notice of the designer before execution and his design to be final.
*This drawing is to be read in conjunction with detail scale drawings and other relevant drawing.

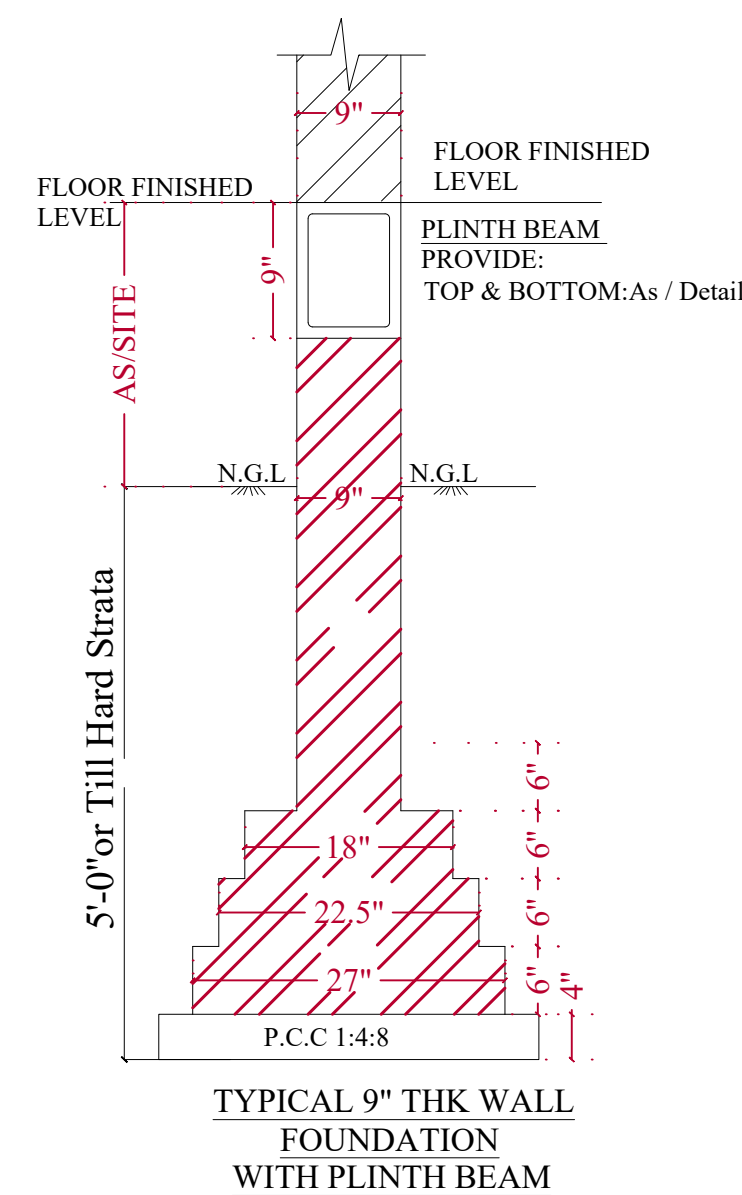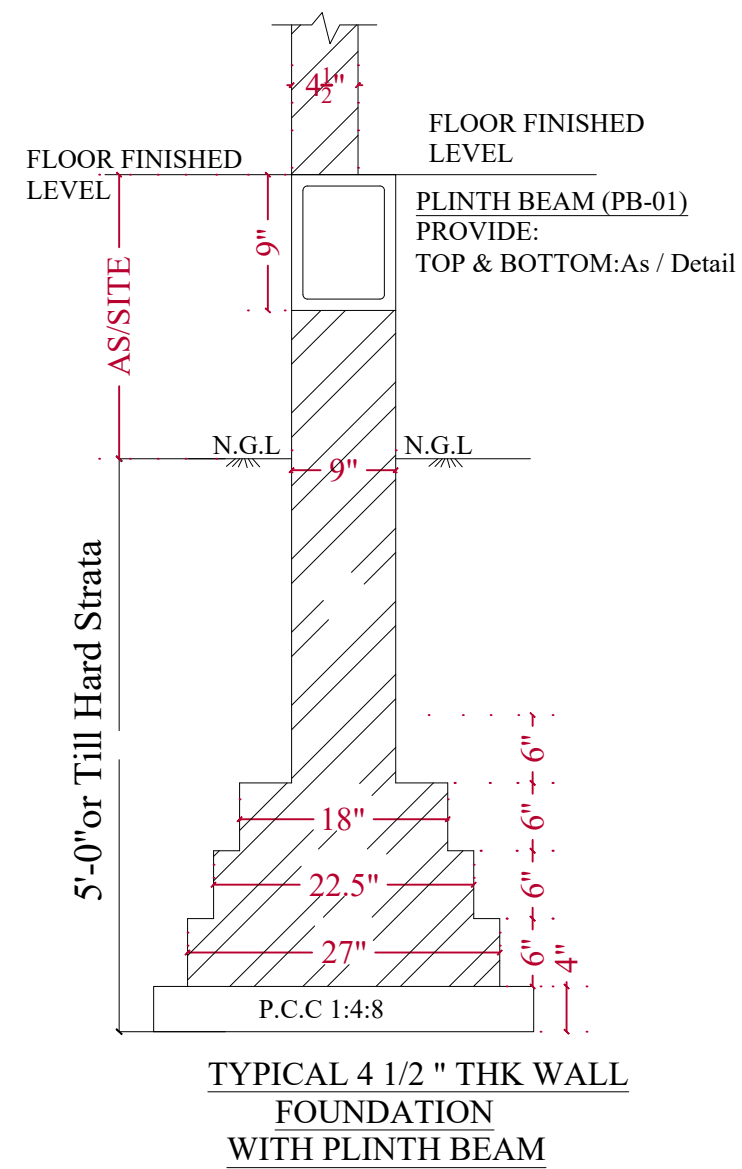

PLINTH BEAM DETAIL

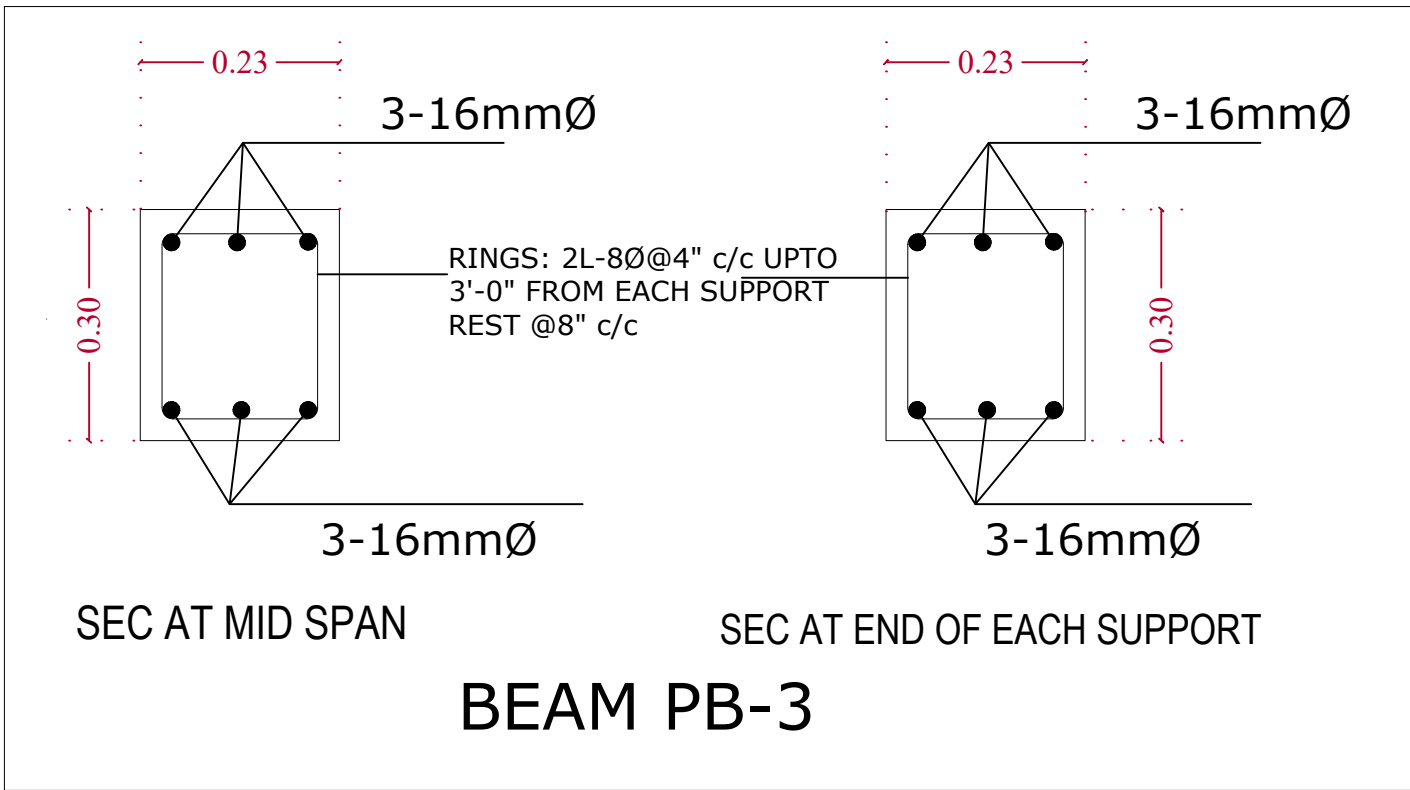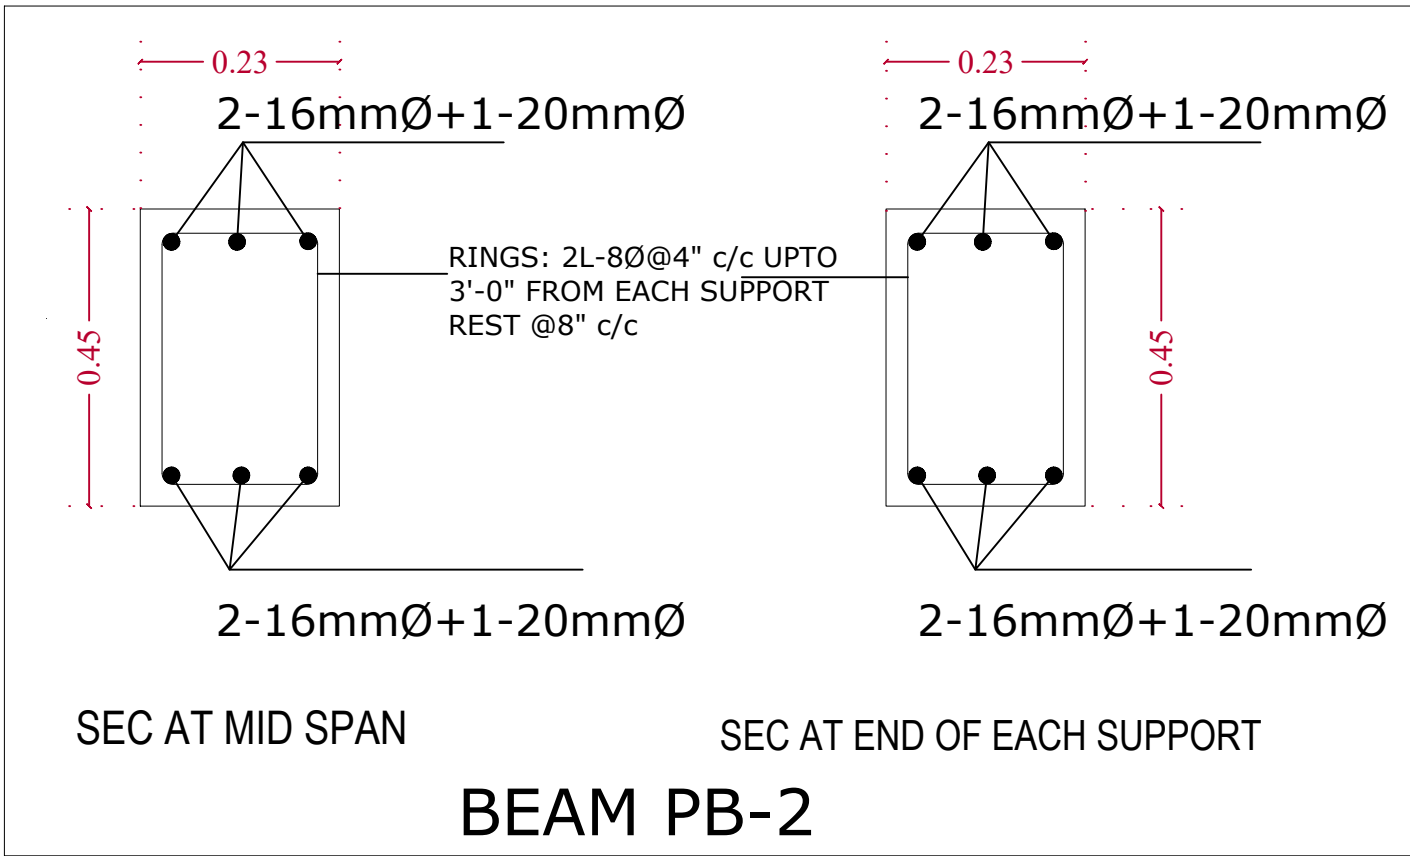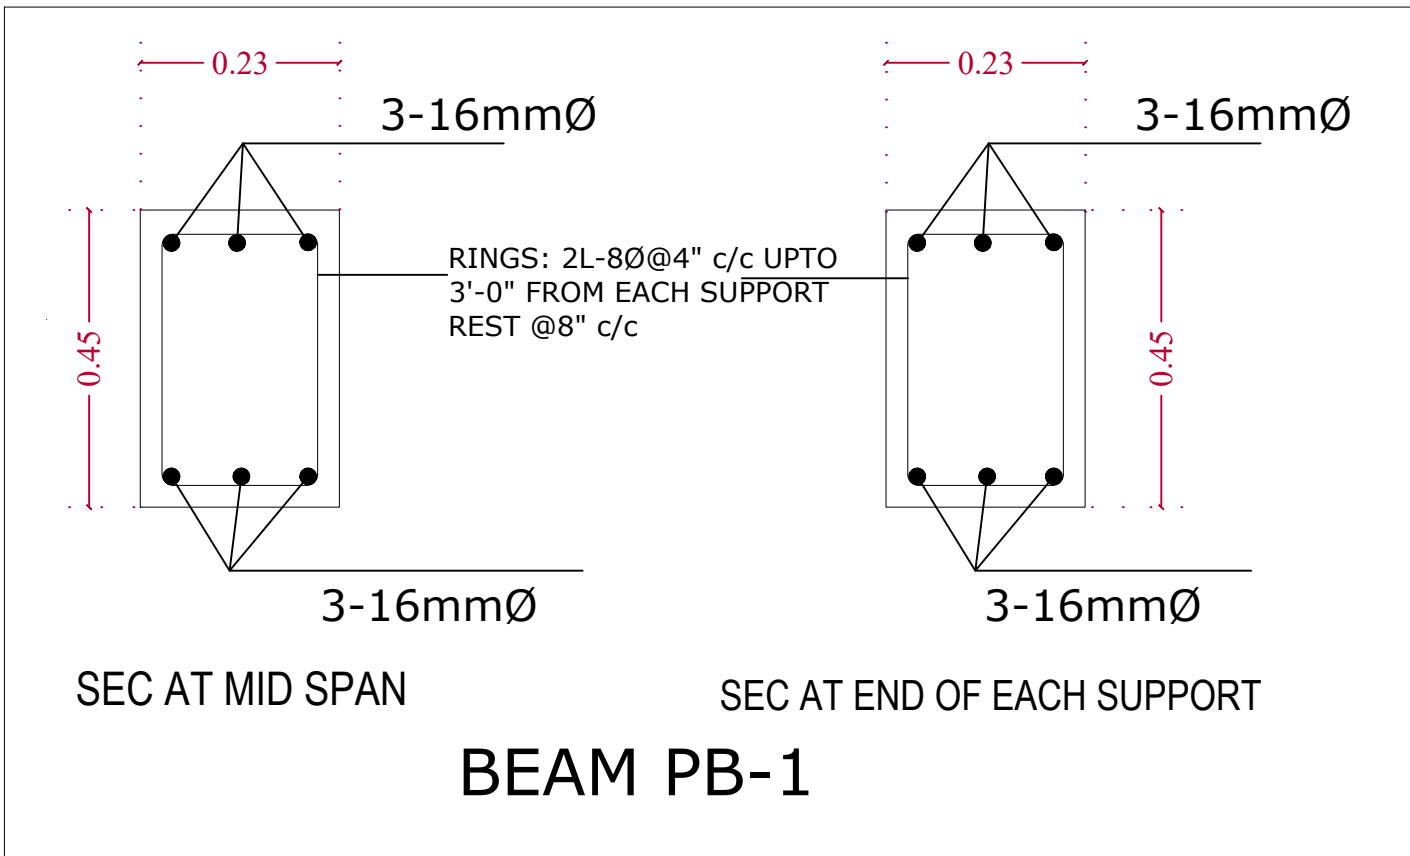

PLINTH BEAM DETAIL

PRINT THIS TYPE OF DRAWING ON A3 PAGE SIZE

NOTE:-
*This drawing is the property of 7 Frames Designs and shall not be copied or used in any way without their prior permission.
*All dimension are as indicated unless otherwise mentioned.
*Drawing not to be scaled, dimensions to be followed.
*All discrepancies to be brought to the notice of the designer before execution and his design to be final.
*This drawing is to be read in conjunction with detail scale drawings and other relevant drawing.

NOTE - DIMENSIONS HAS TO BE CHECKED FROM SITE.		
DISPATCH DATE: 17/07/2025		
Scale: NTS		NORTH
Drawn By:		
Checked By:		
ISSUES AND REVISIONS		
NO.	DATE	REMARKS
1		
2		
3		

NOTE :-

CLIENT : THE EXECUTIVE ENGINEER
PANCHAYATI RAJ DISTRICT JIND HARYANA

PROJECT:

DRAWING TITLE:
PLINTH BEAM DETAIL


☐ CONCEPTUAL DRG ☐ WORKING DRG
☐ SCHEMATIC DRG ☐ AS BUILT DRG

QUANTITY.- 1

SUBMITTED BY :-

D.B.S.C.R.
GOVT. POLYTECHNIC
SAMPLA

G.F ROOF BEAM LAYOUT

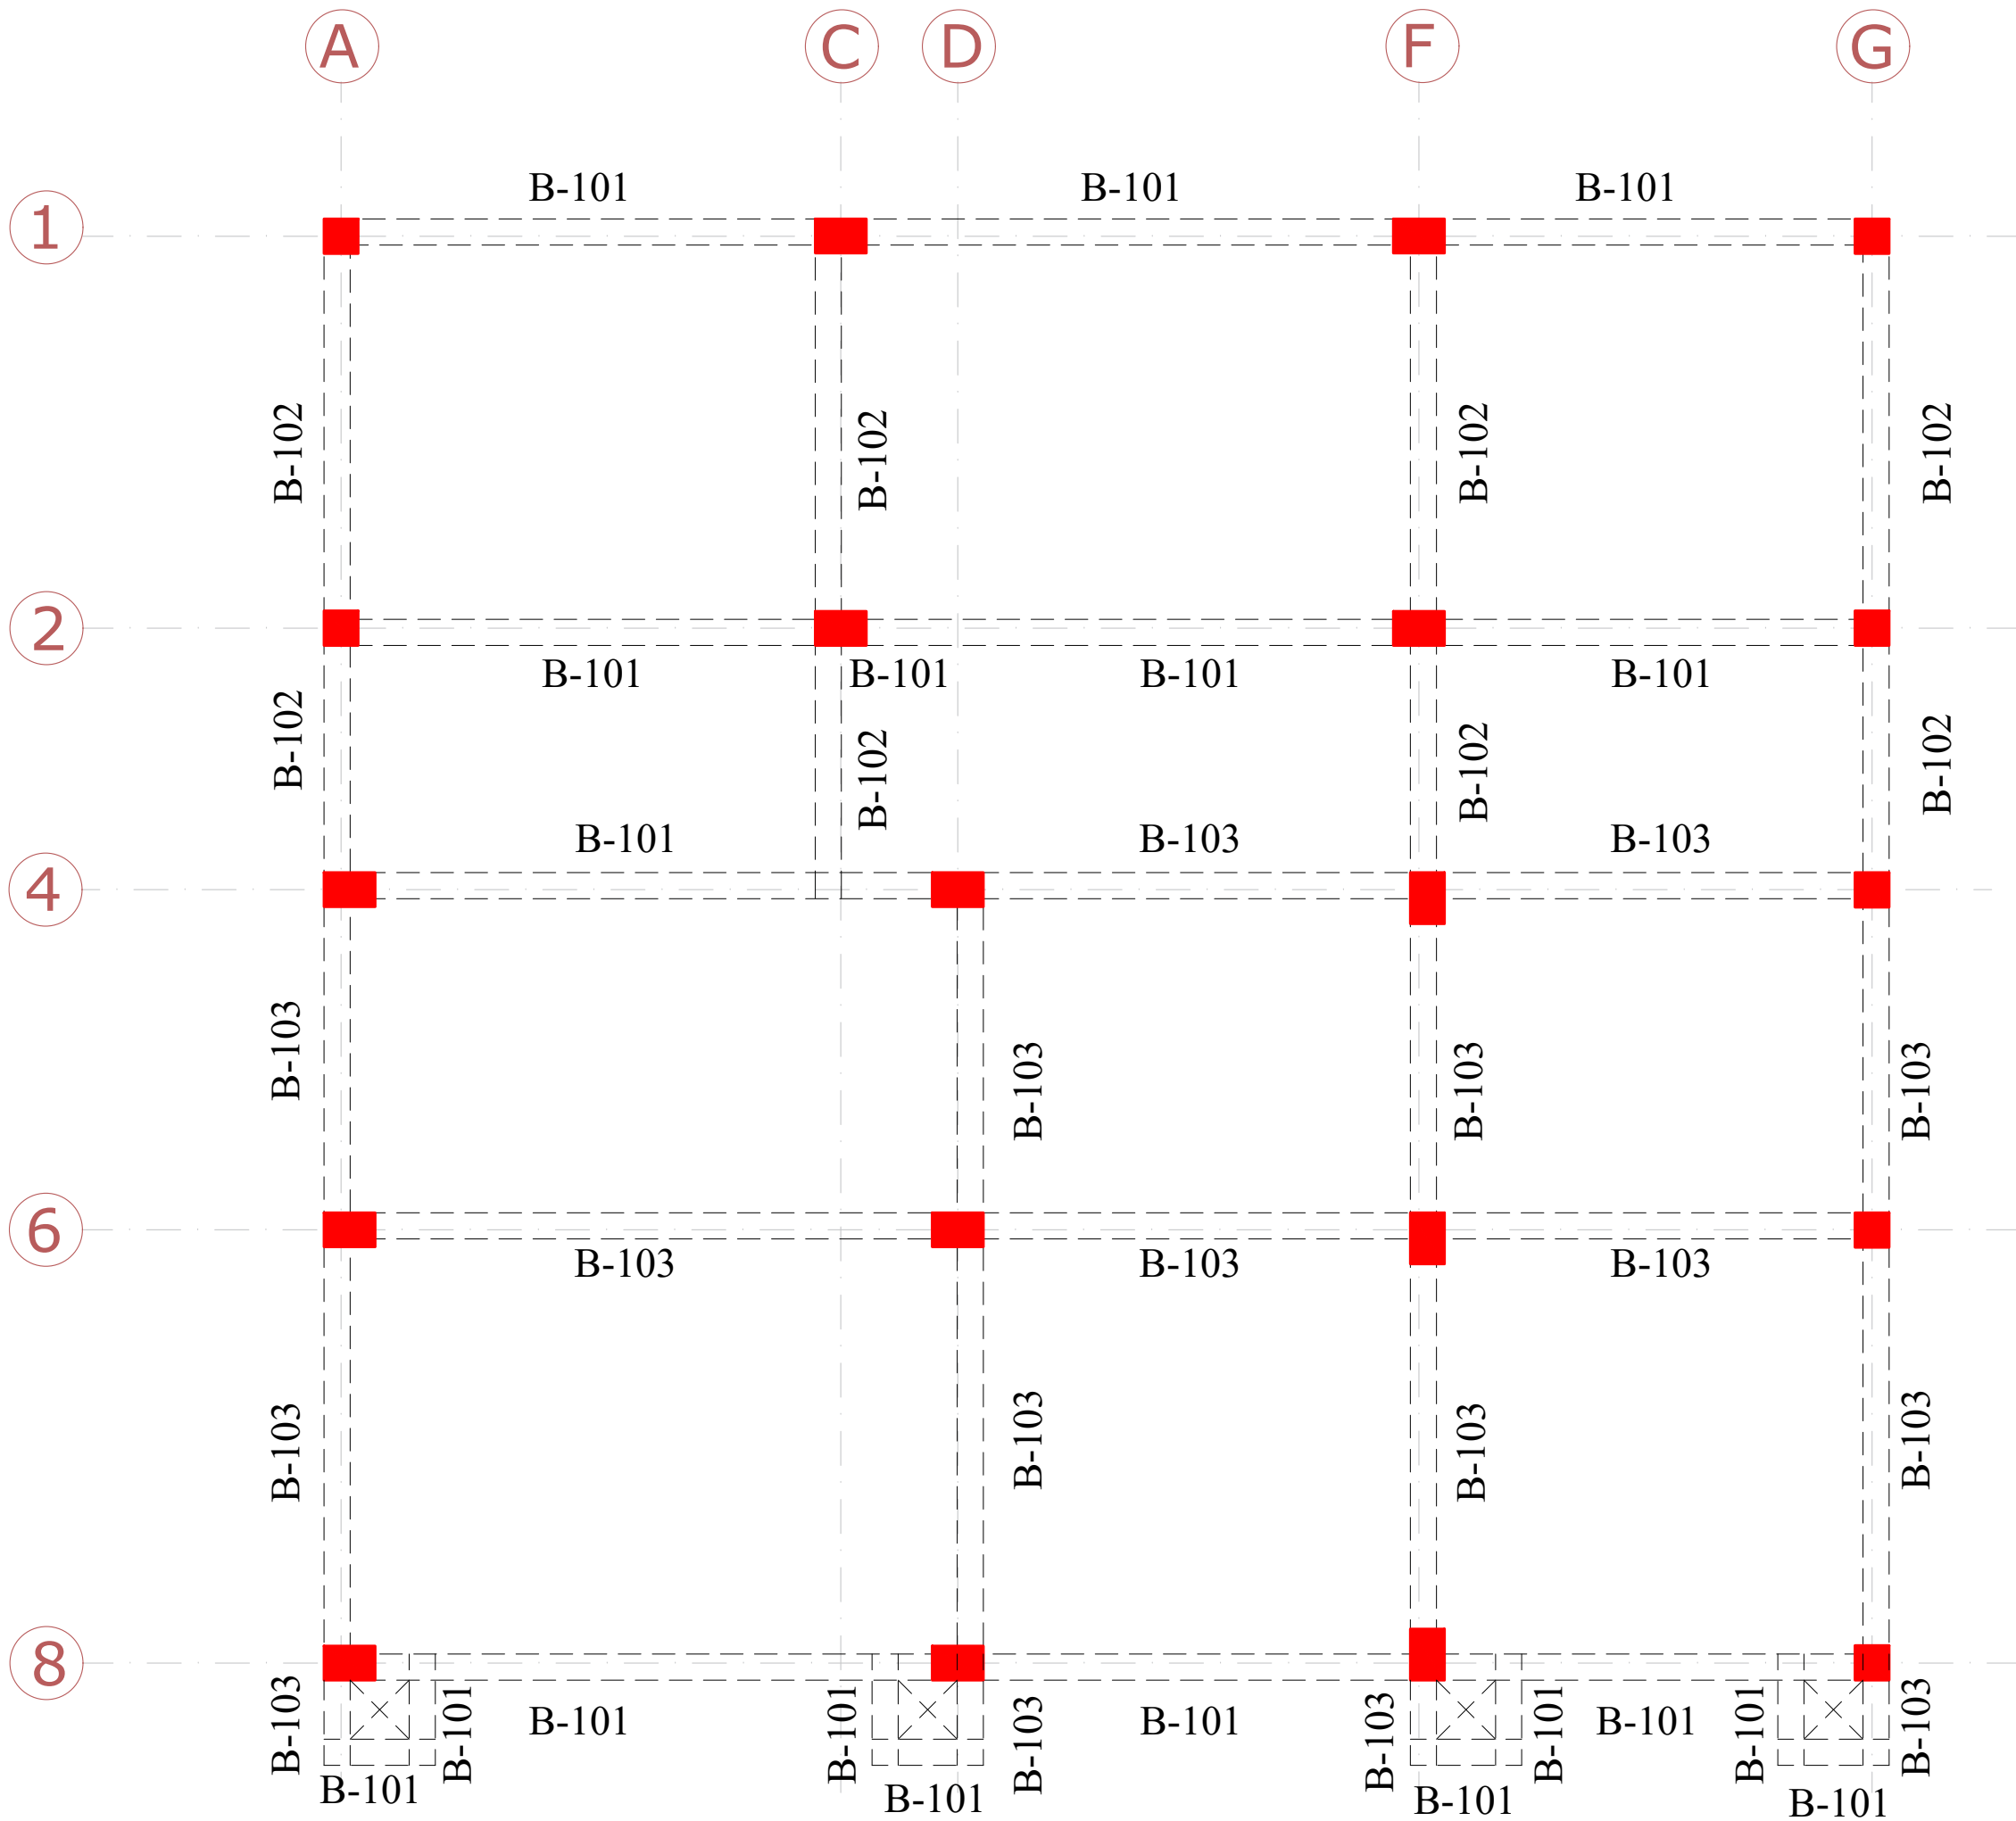

- NOTE:-
- CHECK ALL DIMENSIONS AND LEVELS WITH ARCHITECTURAL DRAWING.
 - THERE WILL BE NO FUTURE EXPANSION ABOVE GROUND FLOOR.

SUBMITTED BY :-

D.B.S.C.R.
GOVT. POLYTECHNIC
SAMPLA

CLIENT : THE EXECUTIVE ENGINEER
PANCHAYATI RAJ DISTRICT JIND
HARYANA

PROJECT:

DRAWING TITLE:
G.F ROOF BEAM LAYOUT

☐ CONCEPTUAL DRG ☐ WORKING DRG

☐ SCHEMATIC DRG ☐ AS BUILT DRG

QUANTITY.- 1

NOTE -

NOTE - DIMENSIONS HAS TO BE
CHECKED FROM SITE.




DISPATCH DATE: 03/09/2025

Scale: NTS NORTH
Drawn By:
Checked By:

ISSUES AND REVISIONS

NO.	DATE	REMARKS
1		
2		
3		

NOTE:-
*This drawing is the property of 7 Frames Designs and shall not be copied or used in any way without their prior permission.
*All dimension are as indicated unless otherwise mentioned.
*Drawing not to be scaled, dimensions to be followed.
*All discrepancies to be brought to the notice of the designer before execution and his design to be final.
*This drawing is to be read in conjunction with detail scale drawings and other relevant drawing.

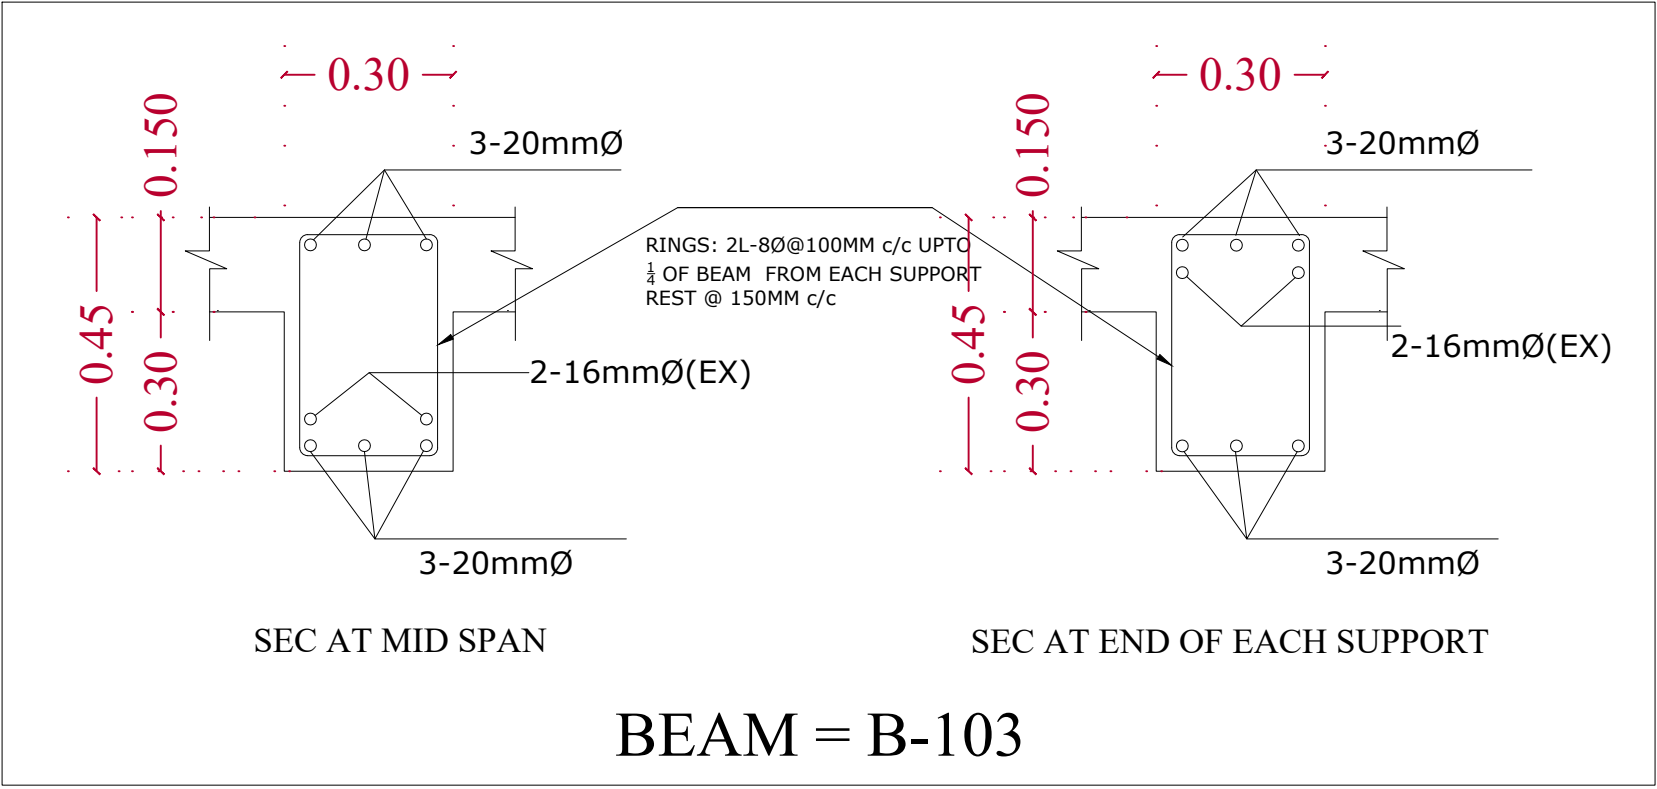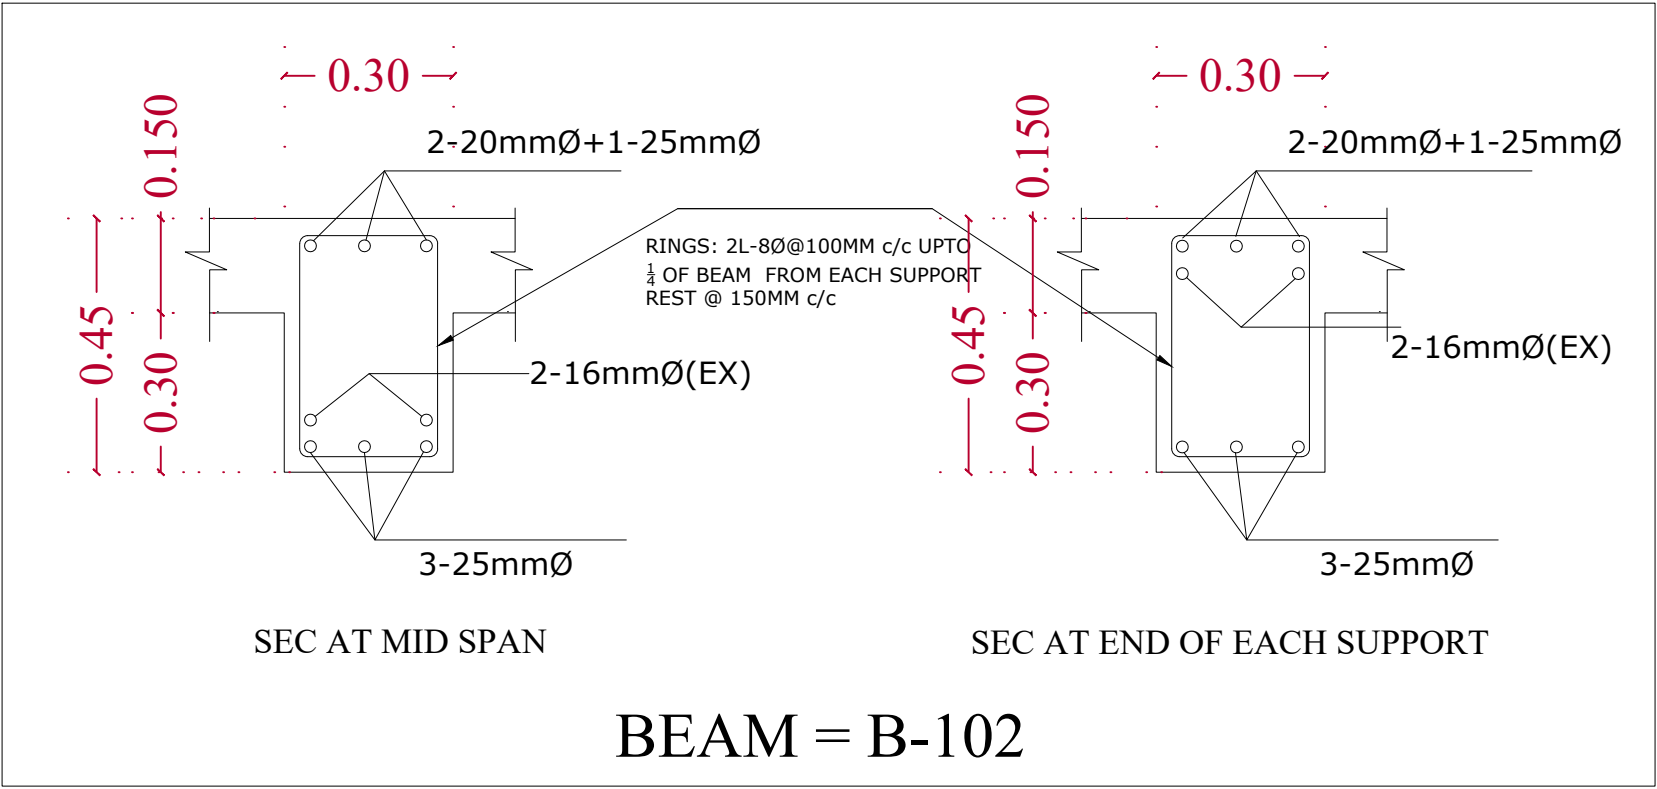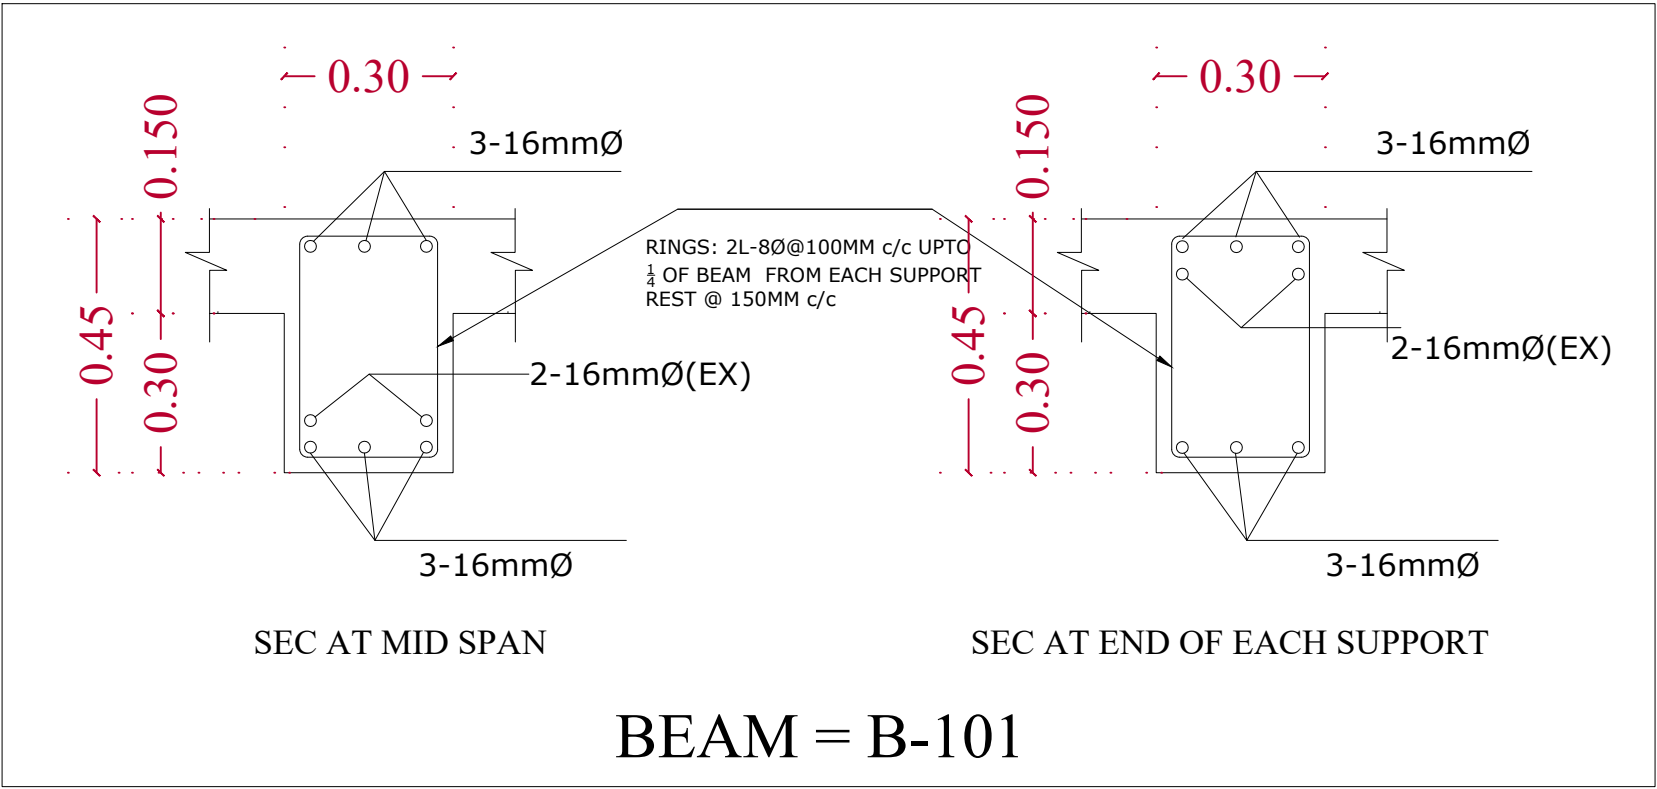

G.F ROOF BEAM DETAIL

PRINT THIS TYPE OF DRAWING ON A3 PAGE SIZE

NOTE:-

- *This drawing is the property of 7 Frames Designs and shall not be copied or used in any way without their prior permission.
- *All dimension are as indicated unless otherwise mentioned.
- *Drawing not to be scaled, dimensions to be followed.
- *All discrepancies to be brought to the notice of the designer before execution and his design to be final.
- *This drawing is to be read in conjunction with detail scale drawings and other relevant drawing.

NOTE - DIMENSIONS HAS TO BE CHECKED FROM SITE.

DISPATCH DATE: 17/07/2025

Scale: NTS NORTH

Drawn By:

Checked By:


ISSUES AND REVISIONS		
NO.	DATE	REMARKS
1		
2		
3		

NOTE :-

CLIENT : THE EXECUTIVE ENGINEER PANCHAYATI RAJ DISTRICT JIND HARYANA	
PROJECT:	
DRAWING TITLE: G.F ROOF BEAM DETAIL	
☐ CONCEPTUAL DRG	☐ WORKING DRG
☐ SCHEMATIC DRG	☐ AS BUILT DRG
QUANTITY.- 1	

SUBMITTED BY :-

D.B.S.C.R.
GOVT. POLYTECHNIC
SAMPLA

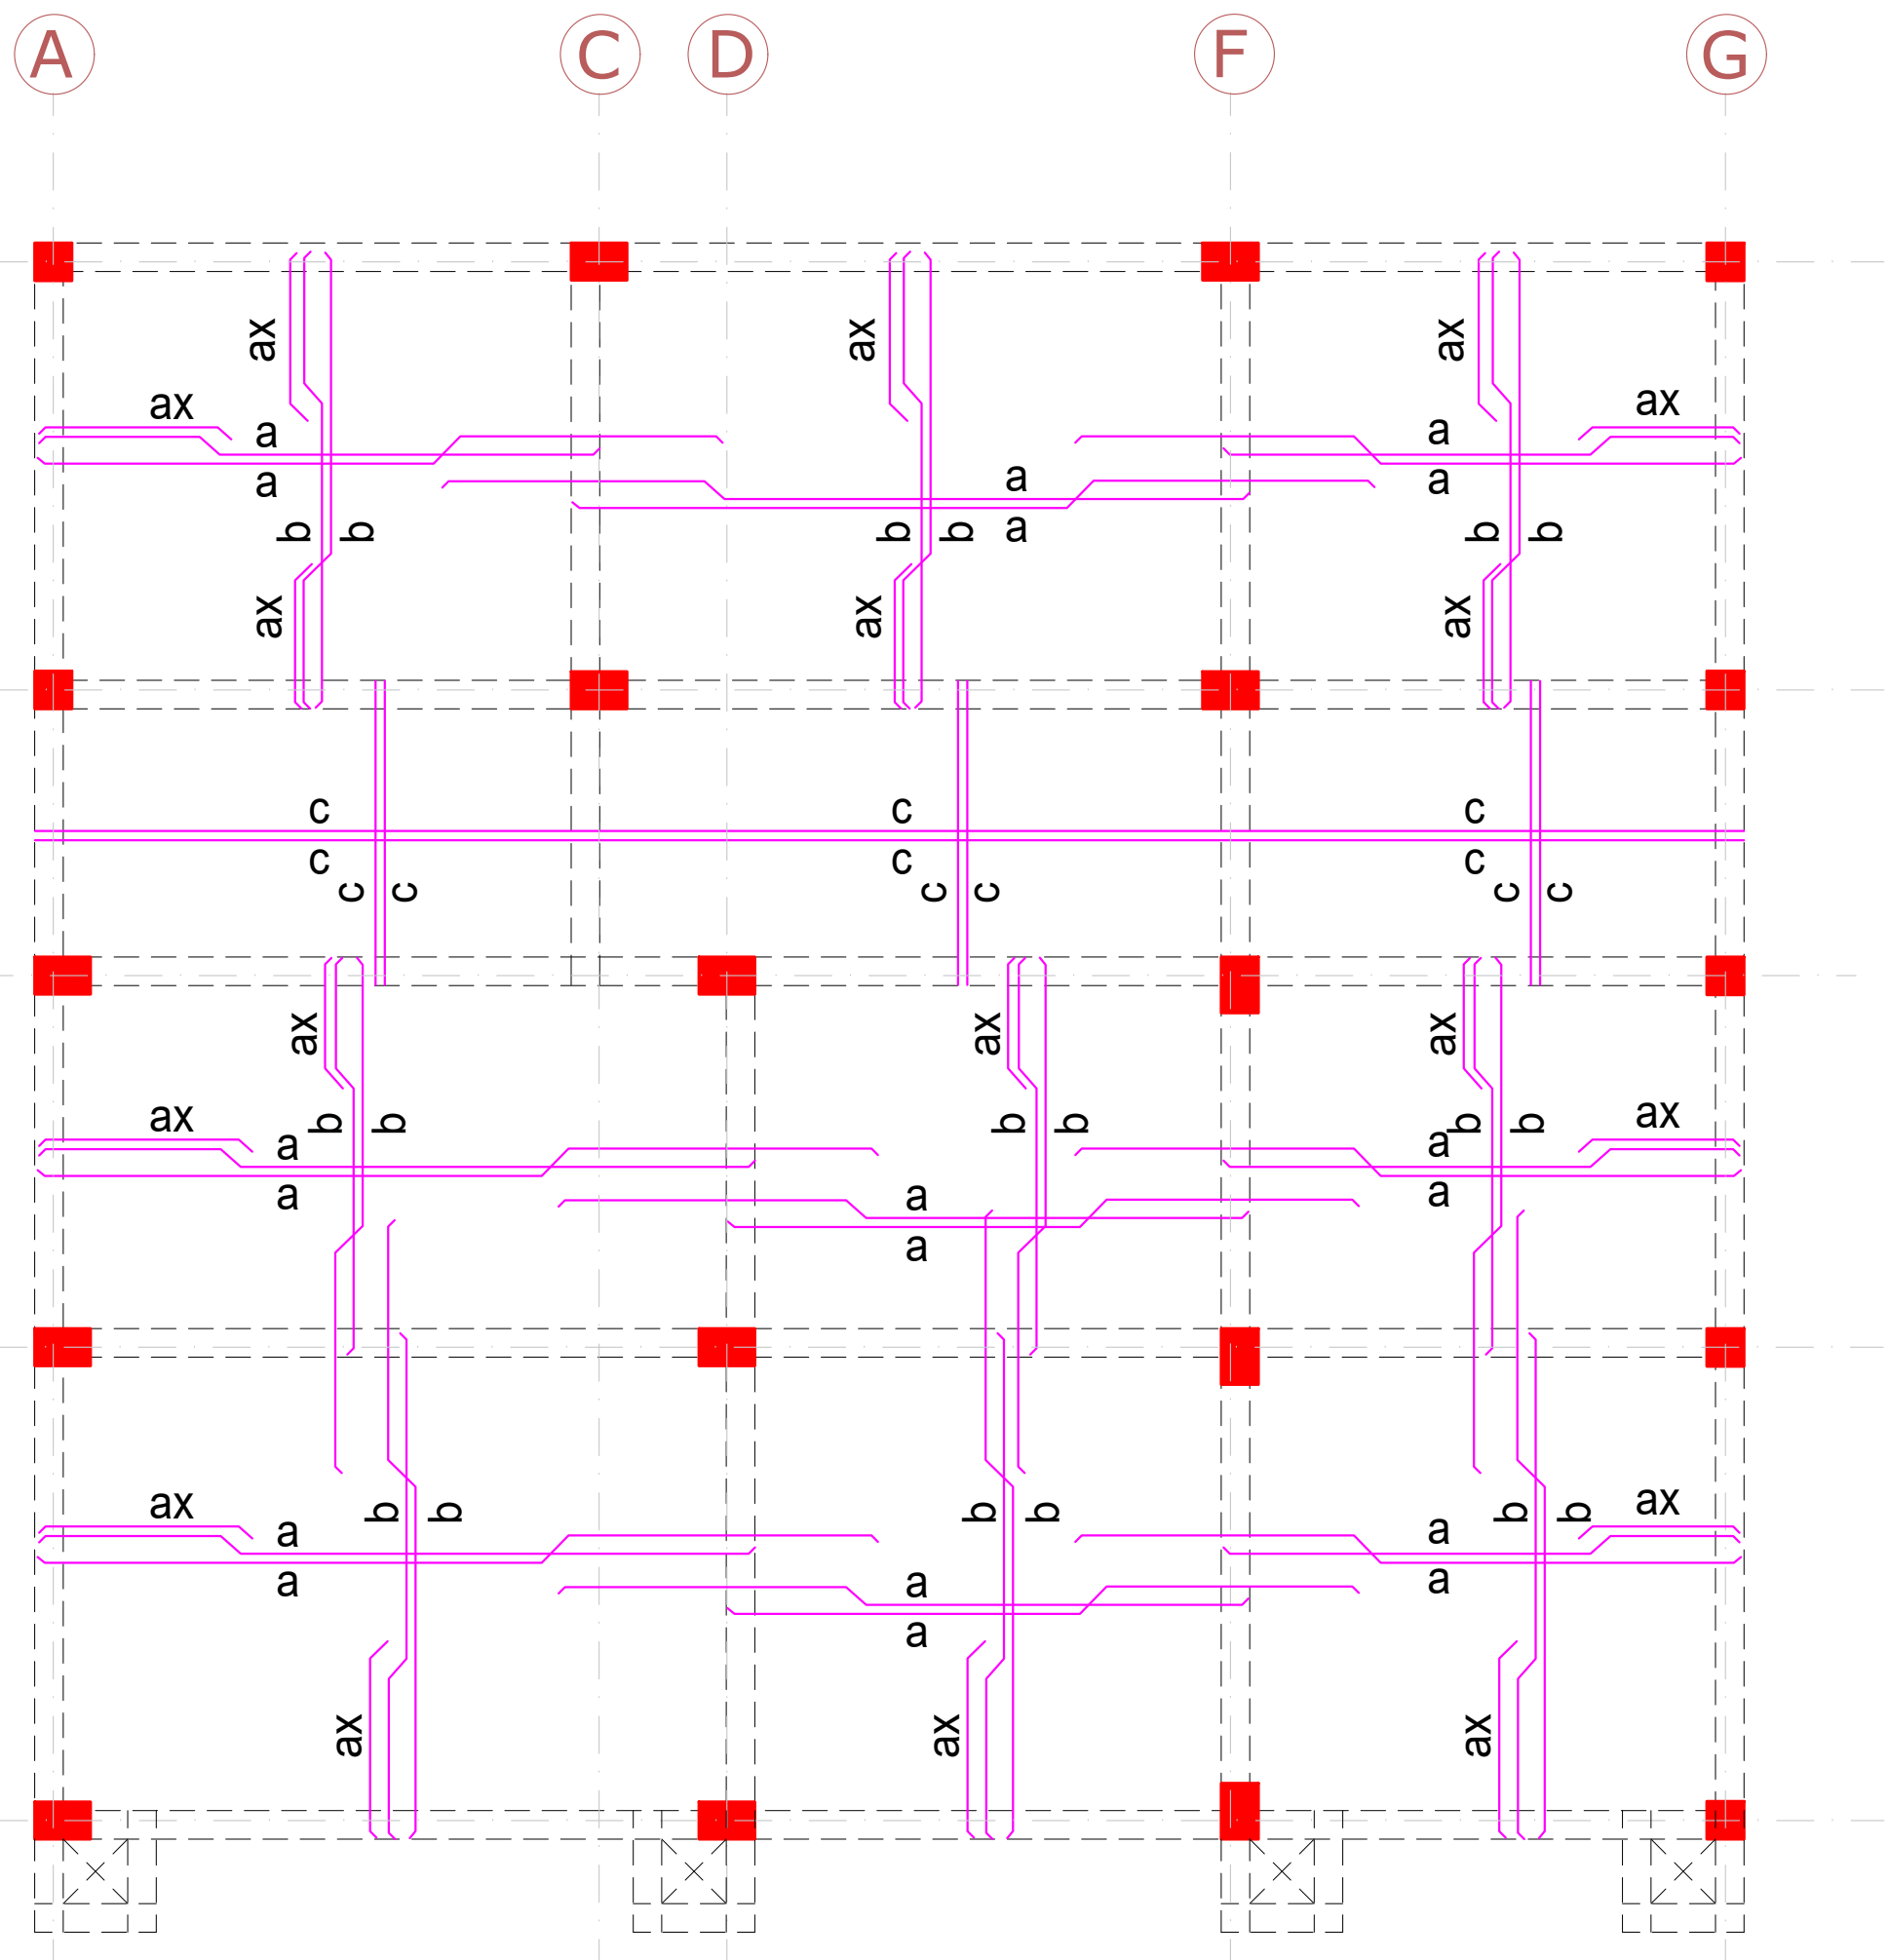

SUBMITTED BY :-

D.B.S.C.R.

GOVT. POLYTECHNIC

SAMPLA

CLIENT : THE EXECUTIVE ENGINEER
PANCHAYATI RAJ DISTRICT JIND
HARYANA

PROJECT:

DRAWING TITLE:
G.F ROOF SLAB REINF. DETAIL

☐ CONCEPTUAL DRG	☐ WORKING DRG
☐ SCHEMATIC DRG	☐ AS BUILT DRG

QUANTITY.- 1

STEEL LEGEND
a = 12mmØ@150mmc/c
ax = 12mmØ@150mmc/c(extra at top)
b = 10mmØ@150mmc/c
bx = 12mmØ@150mmc/c(extra at top)
c = 12mmØ@150mmc/c(top & bottom)
d.s= 10mmØ@150mmc/c(bottom)
e = 10mmØ@150mmc/c(bottom)

SLAB=150mm UNLESS OTHERWISE SPECIFIED.

NOTE - DIMENSIONS HAS TO BE CHECKED FROM SITE.

DISPATCH DATE: 03/09/2025

Scale: NTS	NORTH
Drawn By:	
Checked By:	

ISSUES AND REVISIONS		
NO.	DATE	REMARKS
1		
2		
3		

NOTE:-
*This drawing is the property of 7 Frames Designs and shall not be copied or used in any way without their prior permission.
*All dimension are as indicated unless otherwise mentioned.
*Drawing not to be scaled, dimensions to be followed.
*All discrepancies to be brought to the notice of the designer before execution and his design to be final.
*This drawing is to be read in conjunction with detail scale drawings and other relevant drawing.

G.F ROOF SLAB REINF. DETAIL

NOTE:-
1. CHECK ALL DIMENSIONS AND LEVELS WITH ARCHITECTURAL DRAWING.
2. THERE WILL BE NO FUTURE EXPANSION ABOVE GROUND FLOOR.