

LIST OF DRAWINGS

DRAWING NO.	DRAWING TITLE
JC/ZPHS/AMB/2649/01	COLUMN LAYOUT PLAN
JC/ZPHS/AMB/2649/02	COLUMN STEEL DETAIL
JC/ZPHS/AMB/2649/03	FOUNDATION LAYOUT PLAN
JC/ZPHS/AMB/2649/04	PLINTH BEAMS LAYOUT PLAN
JC/ZPHS/AMB/2649/05	PLINTH BEAM DETAIL
JC/ZPHS/AMB/2649/06	GROUND FLOOR ROOF BEAMS LAYOUT PLAN
JC/ZPHS/AMB/2649/07	ROOF BEAMS DETAIL
JC/ZPHS/AMB/2649/08	GROUND FLOOR ROOF SLAB LAYOUT PLAN
JC/ZPHS/AMB/2649/09	BOUNDARY WALL DETAIL

ENGINEER :-

CLIENT :-
XEN ZILA PARISAD, AMBALA

PROJECT :-

STRUCTURAL DRAWING OF HEALTH
WELLNESS CENTRE AT VILLAGE
ZAFFAR PUR DISTT. AMBALA

TITLE :-

HEALTH WELLNESS CENTRE

SUB TITLE :-

LIST OF DRAWINGS

DRG. NO. :-

JC/

SCALE :-
1 : 100

DATE :-
28-MAY-2025


DRAWN BY:-
JAYA

DSN BY:-
JASBIR

CKD. BY:-
KULBHUSHAN



JC TECHNOCRATS PVT. LTD.
(Formerly known as Jindals Consortium, Since 1990)
STRUCTURAL ENGINEERS, HIGHWAY & BRIDGE DESIGNERS, PROJECT MANAGEMENT CONSULTANTS
ROAD SAFETY AUDITORS, PROOF CONSULTANTS, SURVEYORS AND SOIL INVESTIGATORS
REGD. OFF. : S. C. P-9, VIKAS VIHAR, AMBALA CITY-134003, HARYANA. PH. 0171-255913, MOB--91-98966-70914
DELHI : # 678, GREEN VIEW APARTMENTS, SECTOR 19, POCKET-2, DWARKA, NEW DELHI. MOB--91-99964-70914
Mob- 819907006, 9896550913, e-mail: jindalstructure@gmail.com, jindals13@gmail.com, Web: www.jindalsconsortium.in

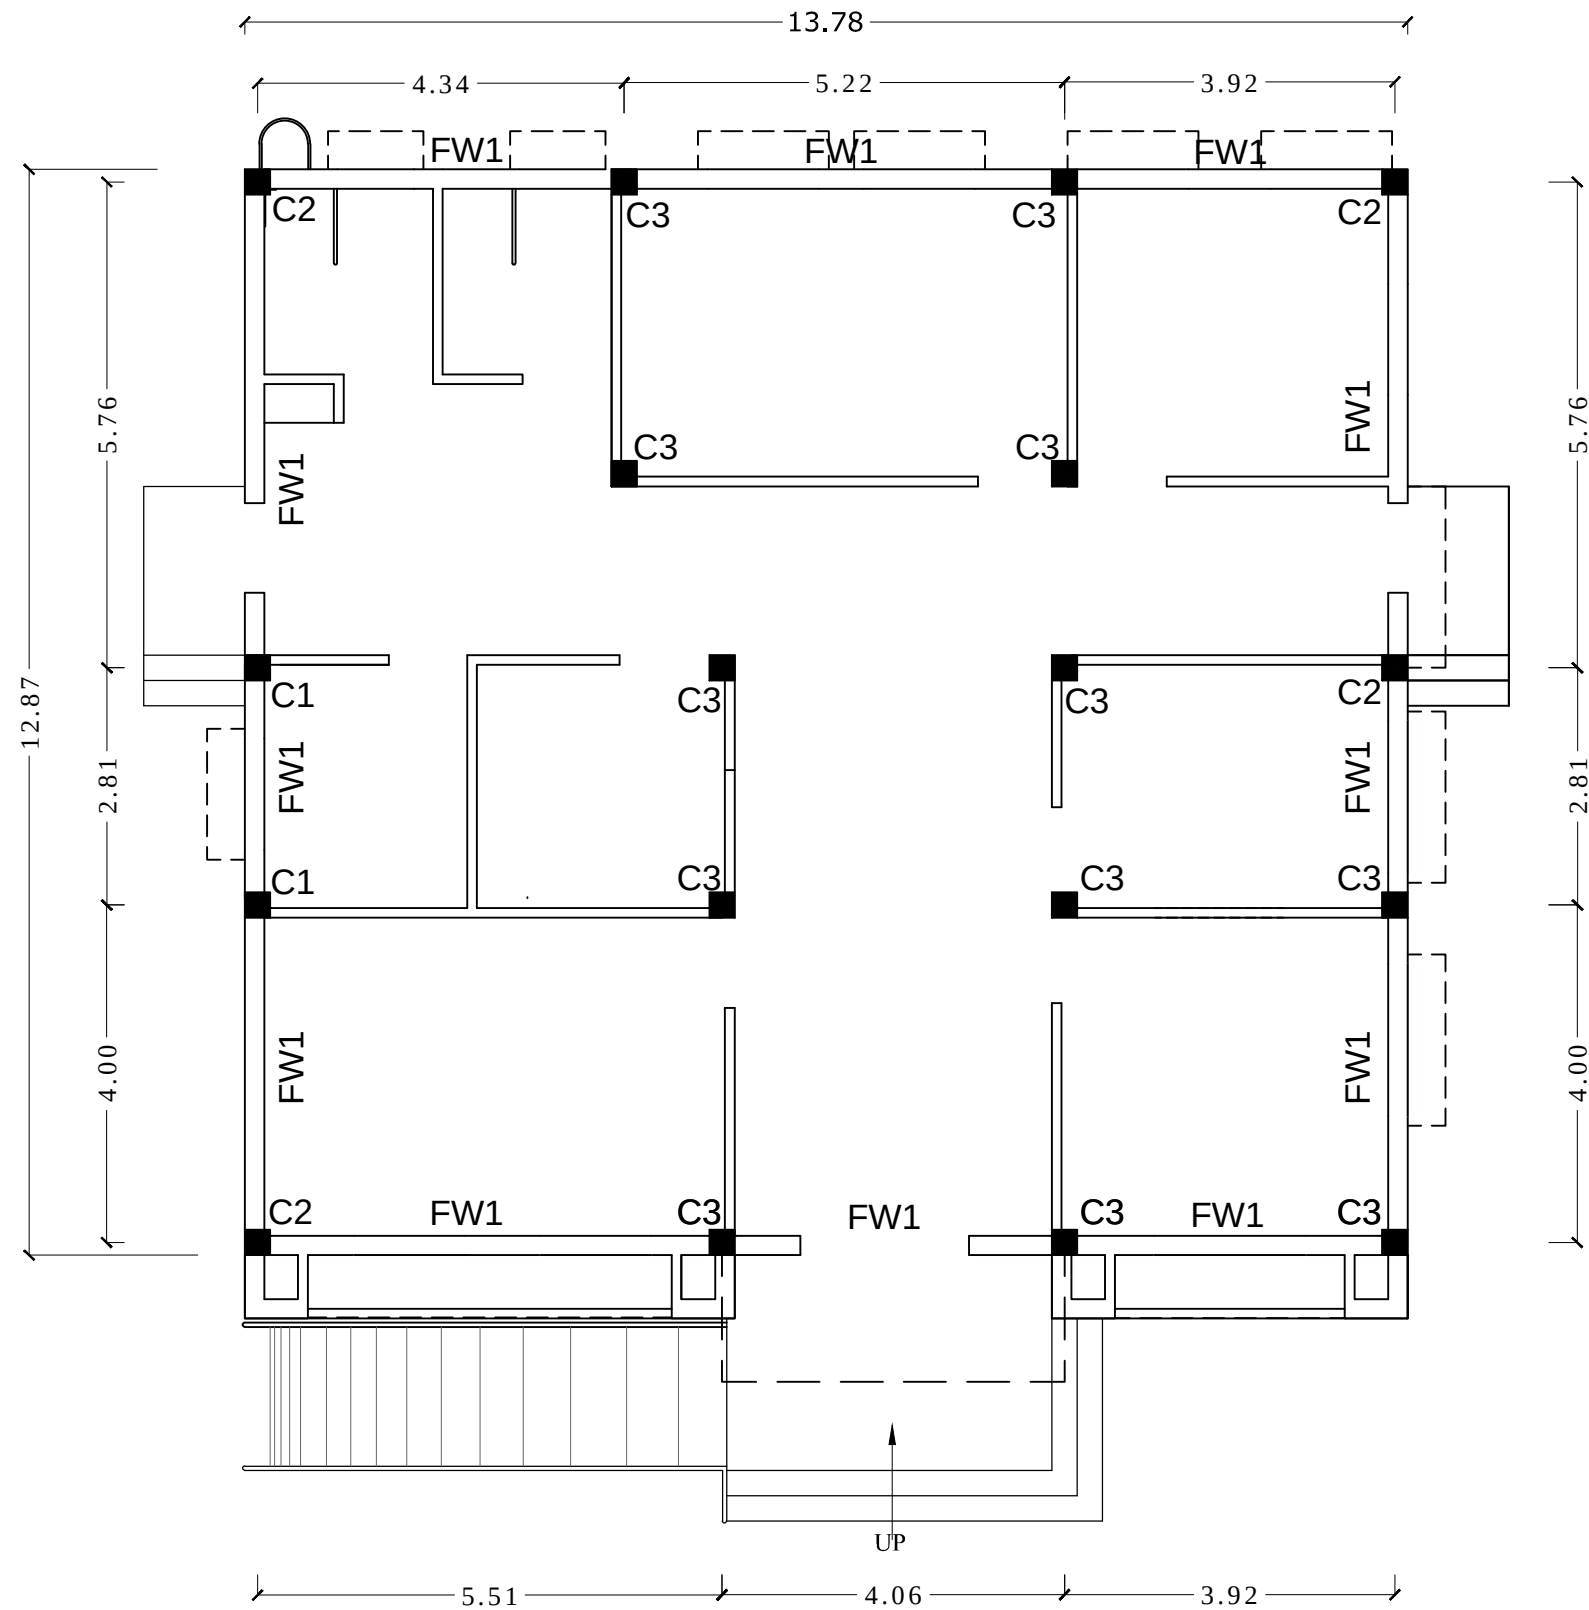

COLUMN LAYOUT PLAN

- NOTES:-
- *NET BEARING CAPACITY OF SOIL IS 7.18 T/m² .
 - *STRUCTURE IS DESIGNED AS SINGLE STOREYED BUILDING FOR SEISMIC ZONE IV.
 - *IF THERE IS ANY DISCREPANCY REGARDING DIMENSIONS, ARCHITECTURAL DRAWINGS MAY BE CONSULTED.
 - *WRITTEN DIMENSIONS SHOULD BE FOLLOWED.
 - *DRAWING IS NOT TO BE SCALED.
 - *Ø TOR MEANS DIAMETER IN MM FOR TOR STEEL BARS.
 - *STEEL SHUTTERING IS TO BE USED FOR ALL CONCRETE WORKS.
 - *STEEL OF COLUMN TO GO UP TO BOTTOM OF FOUNDATION WITH BEND OF 300MM AT BOTTOM .
 - *LEAN CONCRETE WILL BE 150MM TH. IN MIX 1:4:8.
 - *LEAN CONCRETE WILL PROJECT 75MM BEYOND THE R.C.C FOUNDATION.
 - *COVER TO REINFORCEMENT OF COLUMNS WILL BE 40MM ON ALL FACES.
 - *COVER TO REINFORCEMENT OF FOUNDATION SLAB WILL BE 75MM.
 - *DEVELOPMENT LENGTH(L_d) OF STEEL IS 57 TIMES THE DIAMETER OF THE BAR.
 - *CEMENT MORTAR RATIO IN 9"TH. BRICK WORK IS 1:6.
 - *CEMENT MORTAR RATIO IN 4½"TH.BRICK WORK IS 1:4.
 - *WHEREVER THE GAP BETWEEN TWO FOOTINGS IS LESS THAN 900MM, THE LEAN CONCRETE(P.C.C) SHALL BE LAID CONTINUOUSLY.
 - *EATH FILLING IN FOUNDATIONS SHOULD BE DONE EQUALLY ON BOTH SIDES OF FOUNDATION WALL.
 - *M-20 GRADE CONCRETE TO BE USED IN ALL CONCRETE WORKS.
 - *STEEL REINFORCEMENT IS Fe 500 D
 - *NOT MORE THAN 50%AREA OF STEEL BARS SHALL BE SPLICED AT ONE SECTION.

ENGINEER :-

CLIENT :-

XEN ZILA PARISAD, AMBALA

PROJECT :-

STRUCTURAL DRAWING OF HEALTH
WELLNESS CENTRE AT VILLAGE
ZAFFAR PUR DISTT. AMBALA

TITLE :-

HEALTH WELLNESS CENTRE

SUB TITLE :-

COLUMNS LAYOUT PLAN

DRG NO.

JC/ZPHS/AMB/2649/01

SCALE :-

1 : 100

DATE :-

28-MAY-2025

DRAWN BY:-

JAYA

DSN BY:-

JASBIR












CHKD BY:-

KULBHUSHAN



JC TECHNOCRATS PVT. LTD.
(Formerly known as Jindals Consortium, Since 1990)

STRUCTURAL ENGINEERS, HIGHWAY & BRIDGE DESIGNERS, PROJECT MANAGEMENT CONSULTANTS
ROAD SAFETY AUDITORS, PROFF. CONSULTANTS, SURVEYORS AND SOIL INVESTIGATORS
REGD.OFF. : S.C.F.-9, VIKAS VIHAR, AMBALA CITY-134003, HARYANA, PH: 0171-255013, MOB:-91-98966-70914
DELHI : # 678, GREEN VIEW APARTMENTS, SECTOR 19, POCKET-2, DWARKA, NEW DELHI. MOB:-91-98964-70914
Mob:- 8199907006, 9896550913, e-mail: jindalsstructure@gmail.com, jindals13@gmail.com, Web: www.jindalsconsortium.in

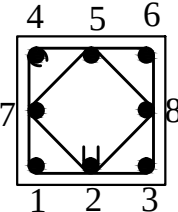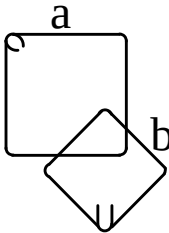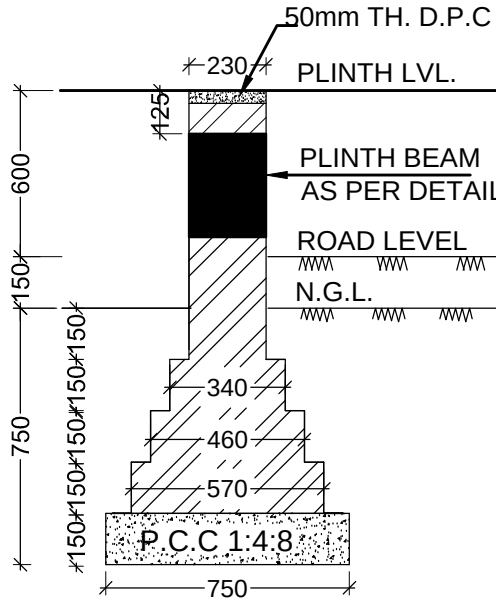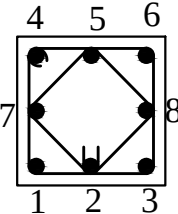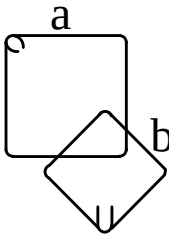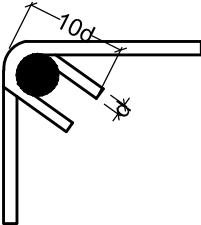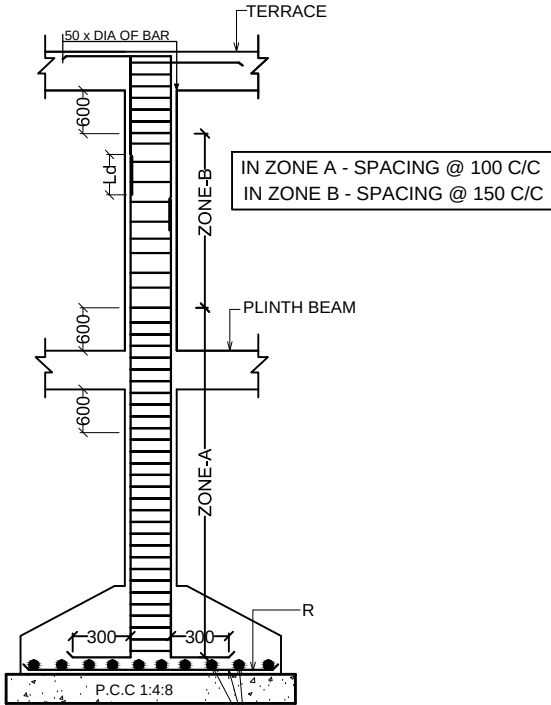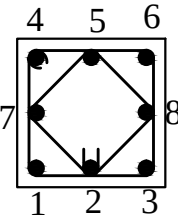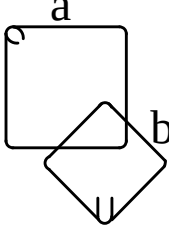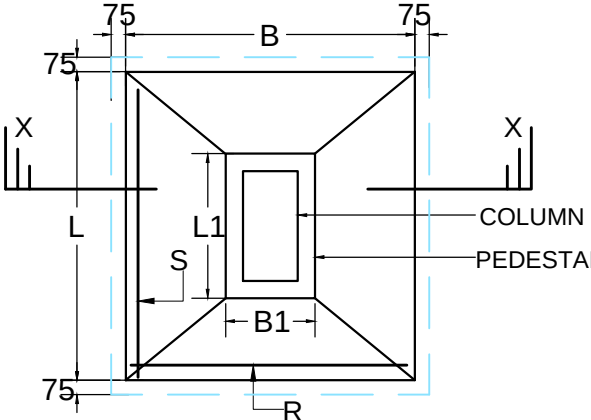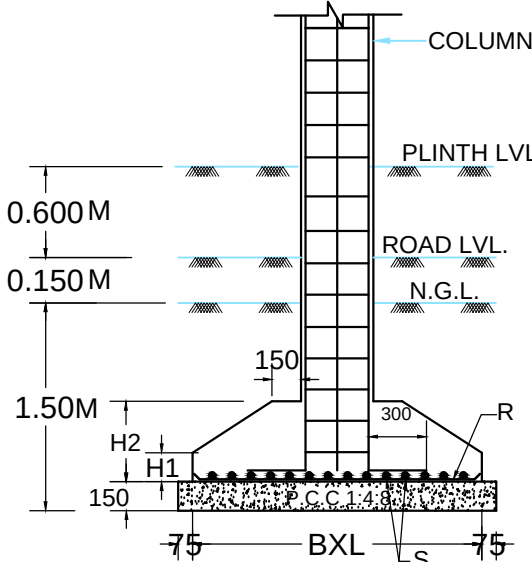COLUMN NO.	COLUMN SIZE	REINFORCEMENT DETAIL	RING DETAIL		
C1	300X300	 BAR NO. :-1 TO 8 - 20Ø TOR RINGS:-10Ø TOR @100C/C AT TOP & BOTTOM @150C/C IN MIDDLE (AS PER DUCTILITY DIAGRAM)	 (a+b)	 FOUNDATION OF 230 TH. BRICK WALL (FW1)	
C2	300X300	 BAR NO. :-1,3,4,6 - 20Ø TOR BAR NO. :-2,5,7,8 - 16Ø TOR RINGS:-10Ø TOR @100C/C AT TOP & BOTTOM @150C/C IN MIDDLE (AS PER DUCTILITY DIAGRAM)	 (a+b)	 DETAIL OF HOOK  DUCTILITY DIAGRAM AS PER IS:13920	
C3	300X300	 BAR NO. :-1 TO 8 - 16Ø TOR RINGS:-10Ø TOR @100C/C AT TOP & BOTTOM @150C/C IN MIDDLE (AS PER DUCTILITY DIAGRAM)	 (a+b)	 TYPICAL PLAN OF COLUMN FOOTING  SECTION AT X-X	

NOTES:-

*NET BEARING CAPACITY OF SOIL IS 7.18 T/m² .

*STRUCTURE IS DESIGNED AS SINGLE STOREYED BUILDING FOR SEISMIC ZONE IV.

*IF THERE IS ANY DISCREPANCY REGARDING DIMENSIONS, ARCHITECTURAL DRAWINGS MAY BE CONSULTED.

*WRITTEN DIMENSIONS SHOULD BE FOLLOWED.

*DRAWING IS NOT TO BE SCALED.

*Ø TOR MEANS DIAMETER IN MM FOR TOR STEEL BARS.

*STEEL SHUTTERING IS TO BE USED FOR ALL CONCRETE WORKS.

*STEEL OF COLUMN TO GO UP TO BOTTOM OF FOUNDATION WITH BEND OF 300MM AT BOTTOM .

*LEAN CONCRETE WILL BE 150MM TH. IN MIX 1:4:8.

*LEAN CONCRETE WILL PROJECT 75MM BEYOND THE R.C.C FOUNDATION.

*COVER TO REINFORCEMENT OF COLUMNS WILL BE 40MM ON ALL FACES.

*COVER TO REINFORCEMENT OF FOUNDATION SLAB WILL BE 75MM.

*DEVELOPMENT LENGTH(L_d) OF STEEL IS 57 TIMES THE DIAMETER OF THE BAR.

*CEMENT MORTAR RATIO IN 9"TH. BRICK WORK IS 1:6.

*CEMENT MORTAR RATIO IN 4½"TH.BRICK WORK IS 1:4.

*WHEREVER THE GAP BETWEEN TWO FOOTINGS IS LESS THAN 900MM, THE LEAN CONCRETE(P.C.C) SHALL BE LAID CONTINUOUSLY.

*EATH FILLING IN FOUNDATIONS SHOULD BE DONE EQUALLY ON BOTH SIDES OF FOUNDATION WALL.

*M-20 GRADE CONCRETE TO BE USED IN ALL CONCRETE WORKS.

*STEEL REINFORCEMENT IS Fe 500 D

*NOT MORE THAN 50%AREA OF STEEL BARS SHALL BE SPLICED AT ONE SECTION.

ENGINEER:-

CLIENT:-

XEN ZILA PARISAD, AMBALA

PROJECT:-

STRUCTURAL DRAWING OF HEALTH WELLNESS CENTRE AT VILLAGE ZAFFAR PUR DISTT. AMBALA

TITLE:-

HEALTH WELLNESS CENTRE

SUB TITLE:-

COLUMN STEEL DETAIL

DRG NO:-

JC/ZPHS/AMB/2649/02

SCALE :-

DATE :-

DRN BY:-

DSN BY:-

CKD. BY:-

1 :100

28-MAY-2025

JAYA

JASBIR

KULBHUSHAN

 JC TECHNOCRATS PVT. LTD.

(Formerly known as Jindals Consortium, Since 1990)


STRUCTURAL ENGINEERS, HIGHWAY & BRIDGE DESIGNERS, PROJECT MANAGEMENT CONSULTANTS

ROAD SAFETY AUDITORS, PROOF CONSULTANTS, SURVEYORS AND SOIL INVESTIGATORS

REGD.OFF. : S.C.P.-9, VIKAS VIHAR, AMBALA CITY-134003, HARYANA. PH: 0171-2558013, MOB:-91-99964-20914

DELHI : # 678, GREEN VIEW APARTMENTS, SECTOR 19, POCKET-2, DWARKA, NEW DELHI. MOB:-91-99964-20914

Mob:-8199907006, 9896550913, e-mail: jindalstructure@gmail.com, jindals13@gmail.com, Web: www.jindalsconsortium.in

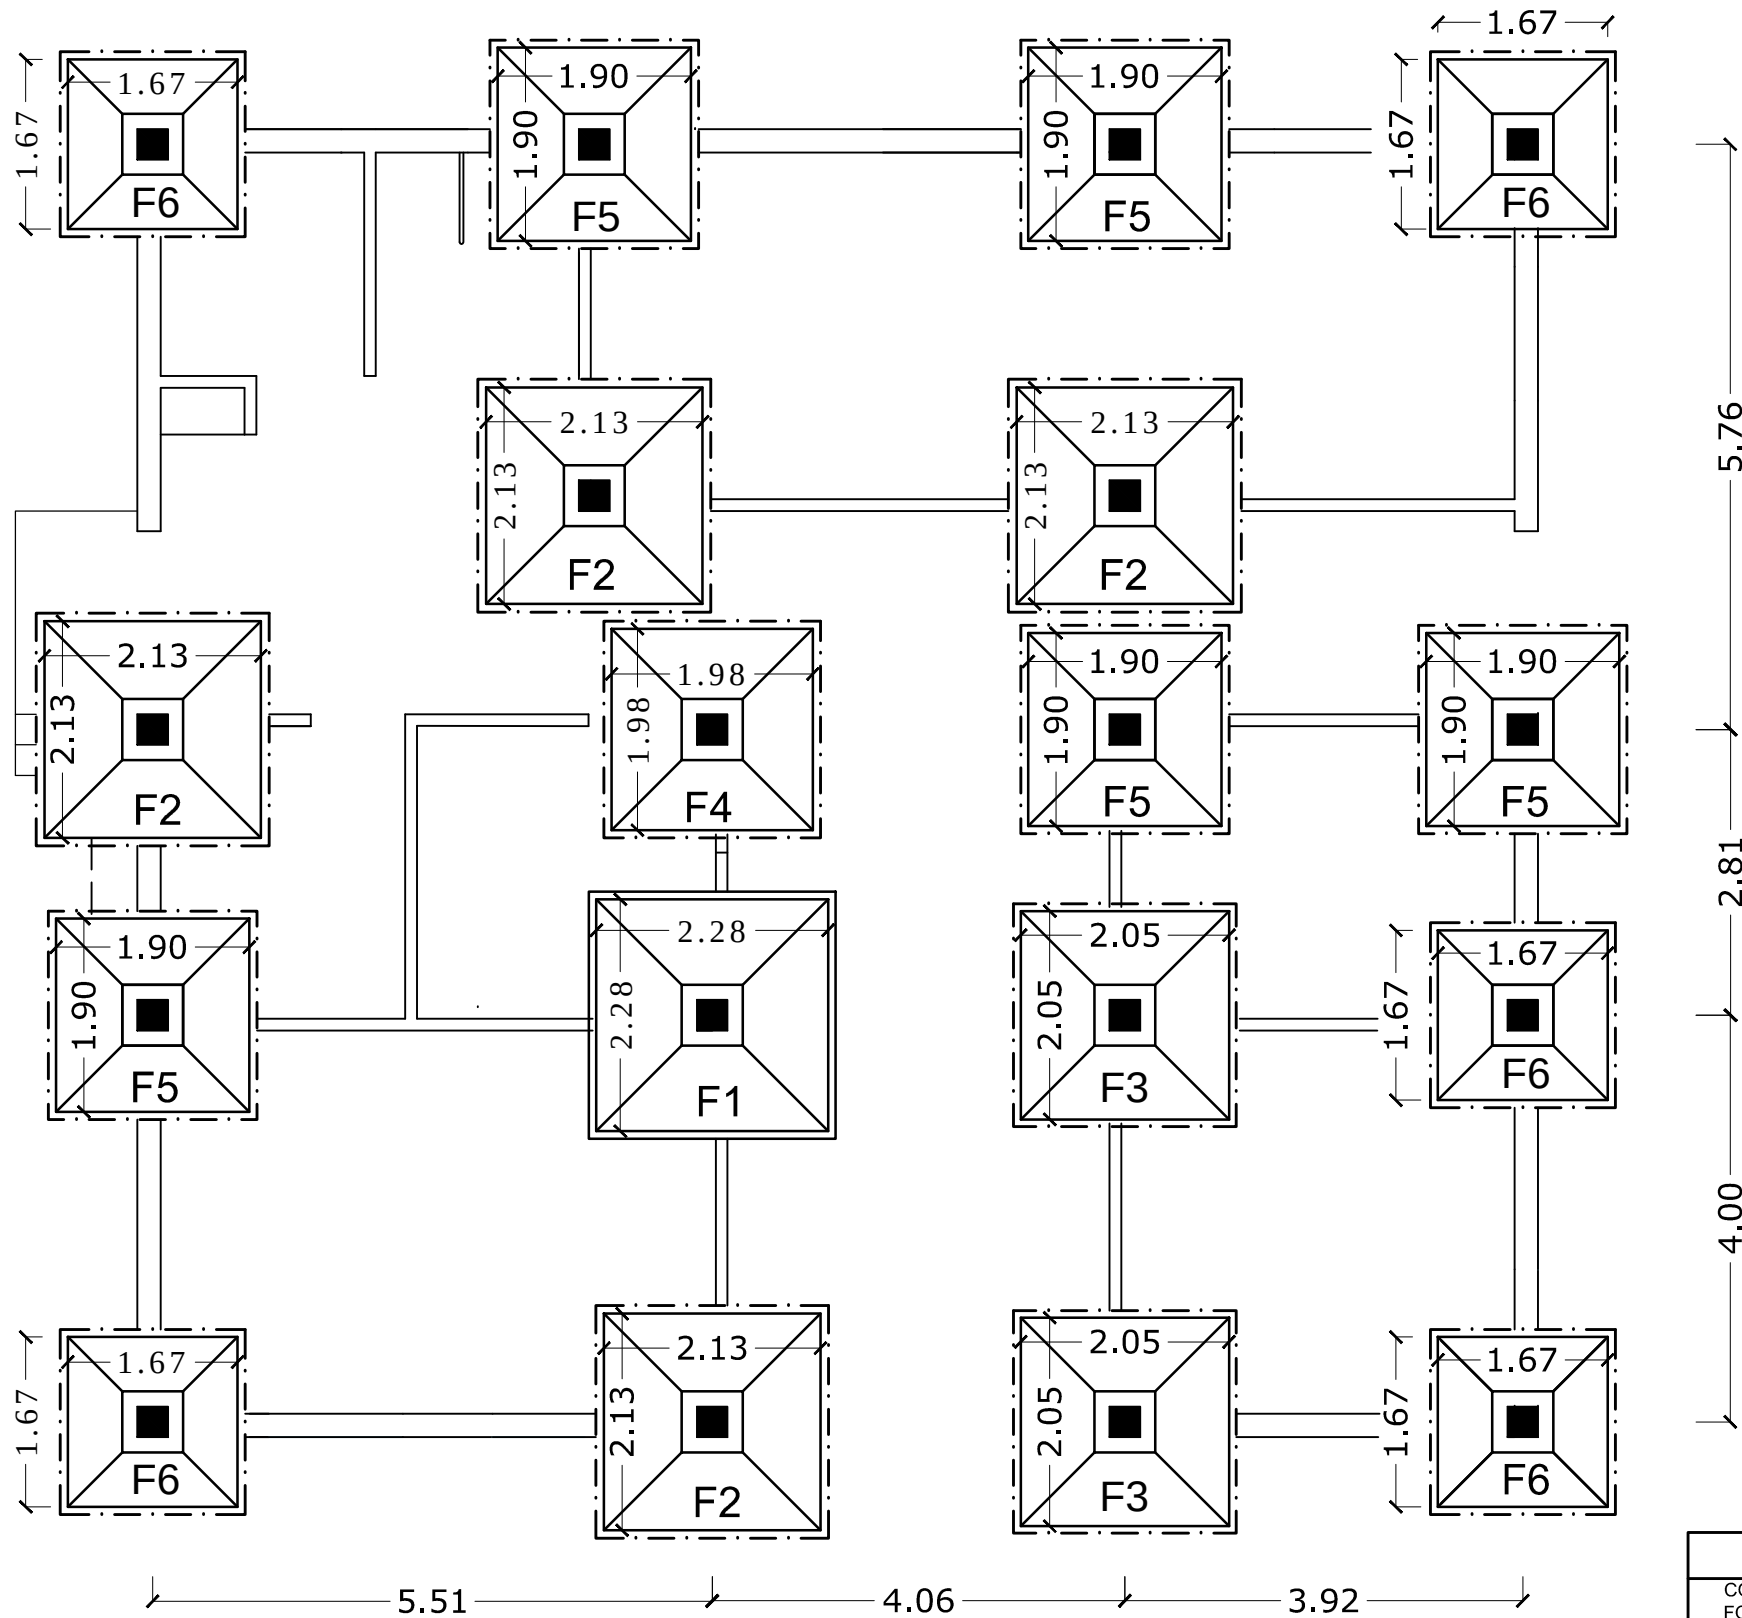

FOUNDATION LAYOUT PLAN

SCHEDULE FOR DETAIL OF COLUMN FOOTING									
COLUMN FOOTING	DIMENSION					REINFORCEMENT FOR FOOTING		PEDESTAL DIMENSION	
	L	B	H ₁	H ₁	D	R	S	L ₁	B ₁
F1	2.28	2.28	0.23	0.60	1.5	10Ø TOR @150 C/C	10Ø TOR @150 C/C	0.60	0.60
F2	2.13	2.13	0.23	0.60	1.5	10Ø TOR @150 C/C	10Ø TOR @150 C/C	0.60	0.60
F3	2.05	2.05	0.23	0.60	1.5	10Ø TOR @150 C/C	10Ø TOR @150 C/C	0.60	0.60
F4	1.98	1.98	0.23	0.60	1.5	10Ø TOR @150 C/C	10Ø TOR @150 C/C	0.60	0.60
F5	1.90	1.90	0.23	0.60	1.5	10Ø TOR @150 C/C	10Ø TOR @150 C/C	0.60	0.60
F6	1.67	1.67	0.23	0.60	1.5	10Ø TOR @150 C/C	10Ø TOR @150 C/C	0.60	0.60

- NOTES:-
- *NET BEARING CAPACITY OF SOIL IS 7.18 T/m² .
 - *STRUCTURE IS DESIGNED AS SINGLE STOREYED BUILDING FOR SEISMIC ZONE IV.
 - *IF THERE IS ANY DISCREPANCY REGARDING DIMENSIONS, ARCHITECTURAL DRAWINGS MAY BE CONSULTED.
 - *WRITTEN DIMENSIONS SHOULD BE FOLLOWED.
 - *DRAWING IS NOT TO BE SCALED.
 - *WATER FOR CONSTRUCTION PURPOSES SHALL CONFIRM TO RELEVANT CLAUSES OF IS. 456:2000.
 - *Ø TOR MEANS DIAMETER IN MM FOR TOR STEEL BARS.
 - *STEEL SHUTTERING IS TO BE USED FOR ALL CONCRETE WORKS.
 - *LEAN CONCRETE WILL BE 150 TH. IN MIX 1:4:8.
 - *LEAN CONCRETE WILL PROJECT 75MM BEYOND THE R.C.C FOUNDATION.
 - *AS PER IS:456 :2000 COVER TO REINFORCEMENT OF FOUNDATION WILL BE 60 AND COLUMN WILL BE 40.
 - *OVER LAP LENGTH OF STEEL IS 57 TIMES THE DIAMETER OF THE BAR.
 - *NOT MORE THAN 50% AREA OF STEEL BAR SHALL BE SPLICED AT ONE SECTION.
 - *THE REINFORCEMENT DETAILING SHALL BE AS PER IS :13920
 - *CEMENT MORTAR RATIO IN 230 TH. BRICK WORK IS 1:6.
 - *CEMENT MORTAR RATIO IN 115 TH.BRICK WORK IS 1:4.
 - *WHEREVER THE GAP BETWEEN TWO FOOTINGS IS LESS THAN 900,THE LEAN CONCRETE (P.C.C)SHALL BE LAID CONTINUOUSLY.
 - *MINIMUM SPACING BETWEEN TWO LAYERS OF REINFORCEMENT IN BEAMS WILL BE 25MM.
 - *STEEL BARS OF PLINTH BEAMS SHALL BE L-SHAPED OVER LAPED BY A LENGTH OF 57 TIMES THE DIAMETER OF THE BARS AT ALL CORNERS & JUNCTIONS.
 - *EARTH FILLING IN FOUNDATION SHOULD BE DONE EQUALLY ON BOTH SIDES OF FOUNDATION WALL.
 - *(M-20) GRADE CONCRETE TO BE USED IN ALL CONCRETE WORKS.
 - *STEEL REINFORCEMENT IS Fe 500 D

ENGINEER :-

CLIENT :-

XEN ZILA PARISAD, AMBALA

PROJECT :-

STRUCTURAL DRAWING OF HEALTH
WELLNESS CENTRE AT VILLAGE
ZAFFAR PUR DISTT. AMBALA

TITLE :-

HEALTH WELLNESS CENTRE

SUB TITLE :-

FOUNDATION LAYOUT PLAN

DRG NO.

JC/ZPHS/AMB/2649/03

SCALE :-

1 : 100

DATE :-

28-MAY-2025

DRAWN BY:-

JAYA

DSN BY:-

JASBIR


CHKD BY:-

KULBHUSHAN



JC TECHNOCRATS PVT. LTD.
(Formerly known as Jindals Consortium, Since 1990)


STRUCTURAL ENGINEERS, HIGHWAY & BRIDGE DESIGNERS, PROJECT MANAGEMENT CONSULTANTS
ROAD SAFETY AUDITORS, PROFF. CONSULTANTS, SURVEYORS AND SOIL INVESTIGATORS
DELHI : # 678, GREEN VIEW APARTMENTS, SECTOR 19, POCKET-2, DWARKA, NEW DELHI. MOB:-+91-99966-72914
Mob:- 8199907006, 9896550913, e-mail: jindalstructure@gmail.com, jindals13@gmail.com, Web: www.jindalsconsortium.in

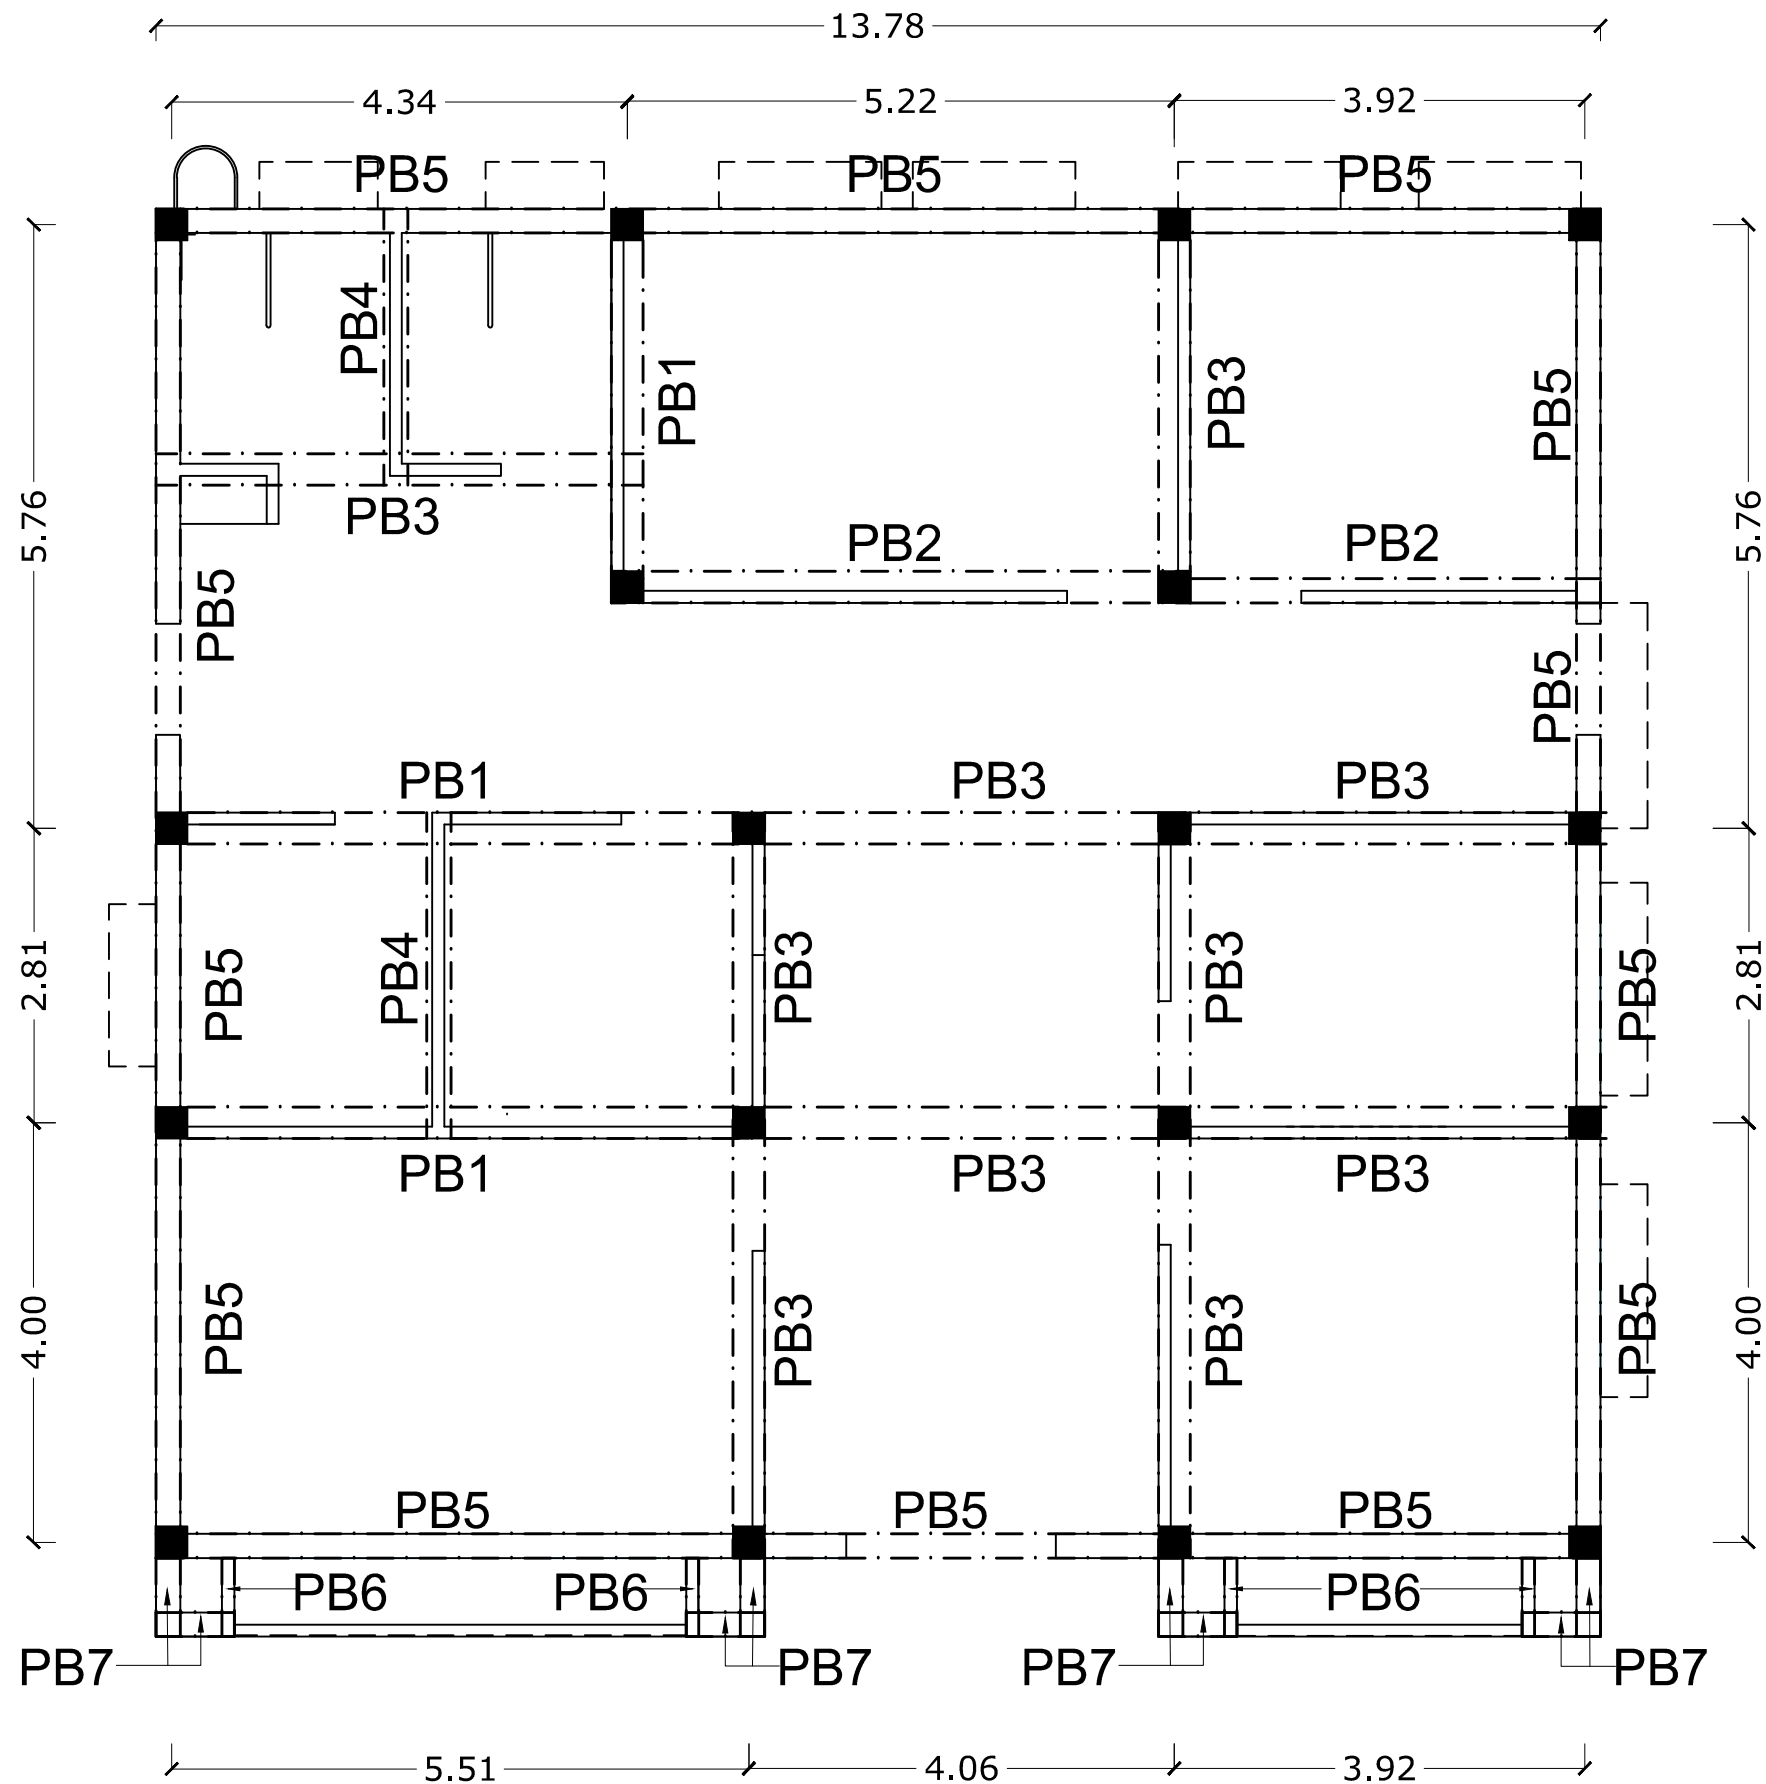


PLINTH BEAM LAYOUT PLAN

NOTES:-
* IF THERE IS ANY DISCREPANCY REGARDING DIMENSIONS, ARCHITECTURAL DRAWINGS MAY BE CONSULTED.
* WRITTEN DIMENSIONS SHOULD BE FOLLOWED.
* DRAWING IS NOT TO BE SCALED.
* M-20 (1:1½:3) GRADE CONCRETE TO BE USED IN ALL CONCRETE WORKS.
* Ø TOR MEANS DIAMETER IN MM FOR TOR STEEL BARS.
* STEEL SHUTTERING IS TO BE USED FOR ALL CONCRETE WORKS.
* LEAN CONCRETE WILL BE 100MM TH. IN MIX 1:4:8.
* LEAN CONCRETE WILL PROJECT 75MM BEYOND THE R.C.C FOUNDATION.
* COVER TO REINFORCEMENT OF COLUMNS WILL BE 40MM ON ALL FACES.
* COVER TO REINFORCEMENT OF FOUNDATION SLAB WILL BE 50MM.
* DEVELOPMENT LENGTH(L_d) OF STEEL IS 57 TIMES THE DIAMETER OF THE BAR.
* CEMENT MORTAR RATIO IN 230mm TH. BRICK WORK IS 1:6.
* CEMENT MORTAR RATIO IN 115mm TH. BRICK WORK IS 1:4.
* WHEREVER THE GAP BETWEEN TWO FOOTINGS IS LESS THAN 900mm, THE LEAN CONCRETE (P.C.C) SHALL BE LAID CONTINUOUSLY.
* EARTH FILLING IN FOUNDATIONS SHOULD BE DONE EQUALLY ON BOTH SIDES OF FOUNDATION WALL.
* WHEREVER PLINTH BEAM LIES DIRECTLY ON EARTH, P.C.C 100mm THICK (1:4:8) MAY BE LAID.
* STEEL BARS OF PLINTH BEAMS SHALL BE L-SHAPED OVER LAPED BY A LENGTH OF 57 TIMES THE DIAMETER OF THE BARS AT ALL CORNERS & JUNCTIONS.
* NOT MORE THAN 50% AREA OF STEEL BARS SHALL BE SPLICED AT ONE SECTION.


ENGINEER:-				
CLIENT:-				
XEN ZILA PARISAD, AMBALA				
PROJECT:-				
STRUCTURAL DRAWING OF HEALTH WELLNESS CENTRE AT VILLAGE ZAFFAR PUR DISTT. AMBALA				
TITLE:-				
HEALTH WELLNESS CENTRE				
SUB TITLE:-			DRG NO:-	
PLINTH BEAMS LAYOUT PLAN			JC/ZPHS/AMB/2649/04	
SCALE :-	DATE :-	DRN BY:-	DSN BY:-	CKD. BY:-
1 : 100	28-MAY-2025	JAYA	JASBIR	KULBHUSHAN
 JC TECHNOCRATS PVT. LTD. (Formerly known as Jindals Consortium, Since 1990) STRUCTURAL ENGINEERS, HIGHWAY & BRIDGE DESIGNERS, PROJECT MANAGEMENT CONSULTANTS ROAD SAFETY AUDITORS, PROFF CONSULTANTS, SURVEYORS AND SOIL INVESTIGATORS HEAD OFFICE : 3 C.T.-9, VIKAS VIHAR, AMBALA CITY-14001, HARYANA. TEL: 0171-2559013, MOB:-91-99966-70914 DELHI : # 678, GREEN VIEW APARTMENTS, SECTOR 15, POCKET-2, DWARKA, NEW DELHI. MOB:-91-99966-70914 Mob:- 9199907006, 9896550913, e-mail: jindalstructure@gmail.com, jindal13@gmail.com, Web: www.jindalconsortium.in				

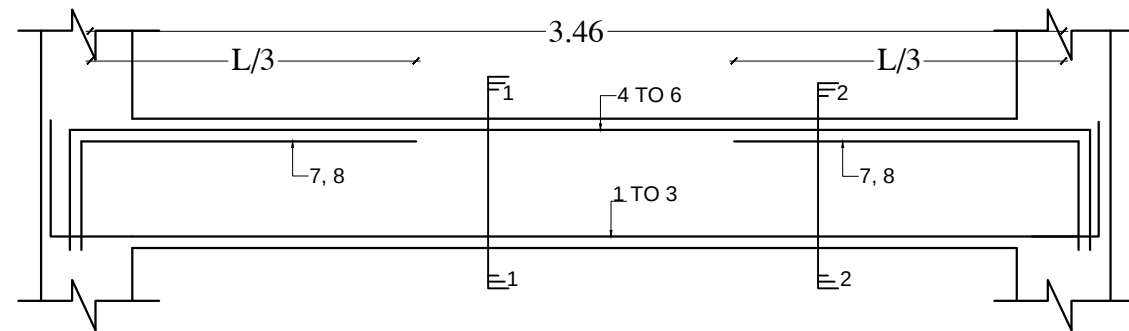

PLINTH BEAM PB-1

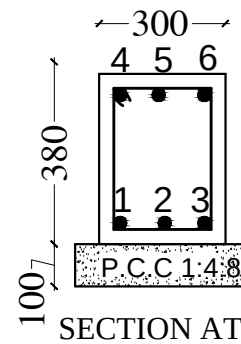


SECTION AT 1-1

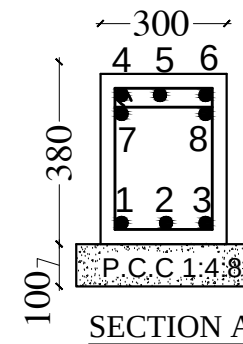

SECTION AT 2-2


BAR NO :-1 TO 6 - 16Ø TOR MAIN STEEL
 BAR NO :- 7,8 - 16Ø TOR EXTRA BAR AT TOP FACE ON SUPPORTS
 RINGS :- 8Ø TOR 2 LEGGED @ 100 C/C 8 NOS. FROM SUPPORT
 @ 150 C/C IN MIDDLE

BEAM 'PB1'

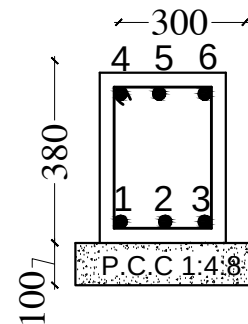


BAR NO :-1 TO 6 - 16Ø TOR MAIN STEEL
 RINGS :- 8Ø TOR 2 LEGGED @ 100 C/C 8 NOS. FROM SUPPORT
 @ 150 C/C IN MIDDLE

BEAM 'PB2'

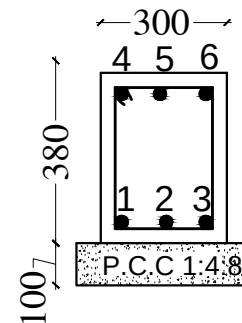


BAR NO :-1,3,4,6 - 16Ø TOR MAIN STEEL
 BAR NO :-2,5 - 12Ø TOR MAIN STEEL
 RINGS :- 8Ø TOR 2 LEGGED @ 100 C/C 8 NOS. FROM SUPPORT
 @ 150 C/C IN MIDDLE

BEAM 'PB3'

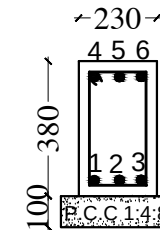


BAR NO :-1 TO 6 - 12Ø TOR MAIN STEEL
 RINGS :- 8Ø TOR 2 LEGGED @ 100 C/C 8 NOS. FROM SUPPORT
 @ 150 C/C IN MIDDLE

BEAM 'PB4'

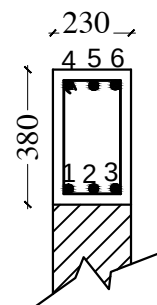


BAR NO :-1 TO 6 - 12Ø TOR MAIN STEEL
 RINGS :- 8Ø TOR 2 LEGGED @ 100 C/C 8 NOS. FROM SUPPORT
 @ 150 C/C IN MIDDLE

BEAM 'PB5'

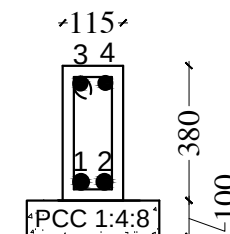


BAR NO :- 1 TO 4 - 12Ø TOR MAIN STEEL
 RINGS :- 8Ø TOR 2 LEGGED @ 150 C/C THROUGHOUT
PLINTH BEAM -PB6
(DUCT BEAM)

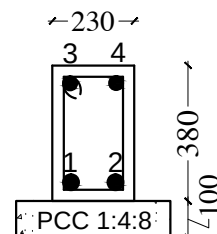

BAR NO :- 1 TO 4 - 12Ø TOR MAIN STEEL
 RINGS :- 8Ø TOR 2 LEGGED @ 150 C/C THROUGHOUT
PLINTH BEAM -PB7
(DUCT BEAM)


ENGINEER:-			
CLIENT:- XEN ZILA PARISAD, AMBALA			
PROJECT:- STRUCTURAL DRAWING OF HEALTH WELLNESS CENTRE AT VILLAGE ZAFFAR PUR DISTT. AMBALA			
TITLE:- HEALTH WELLNESS CENTRE			
SUB TITLE:- PLINTH BEAM DETAIL		DRG NO:- JC/ZPHS/AMB/2649/05	
SCALE :- 1 : 100	DATE :- 28-MAY-2025	DRN BY:- JAYA	CKD. BY:- JASBIR
KULBHUSHAN			
 JC TECHNOCRATS PVT. LTD. (Formerly known as Jindals Consortium, Since 1990) STRUCTURAL ENGINEERS, HIGHWAY & BRIDGE DESIGNERS, PROJECT MANAGEMENT CONSULTANTS ROAD SAFETY AUDITORS, PROOF CONSULTANTS, SURVEYORS AND SOIL INVESTIGATORS HEAD OFFICE : S.C.P.-9, VIKAS VIHAR, AMBALA CITY-13003, HARYANA. PH: 0171-2559013, MOB:-91-99966-70914 DELHI : # 678, GREEN VIEW APARTMENTS, SECTOR 19, POCKET-2, DWARKA, NEW DELHI. MOB:-91-99966-70914 Mob:- 8199907006, 9896550913, e-mail: jindalstructure@gmail.com, jindals13@gmail.com, Web: www.jindalsconsortium.in			

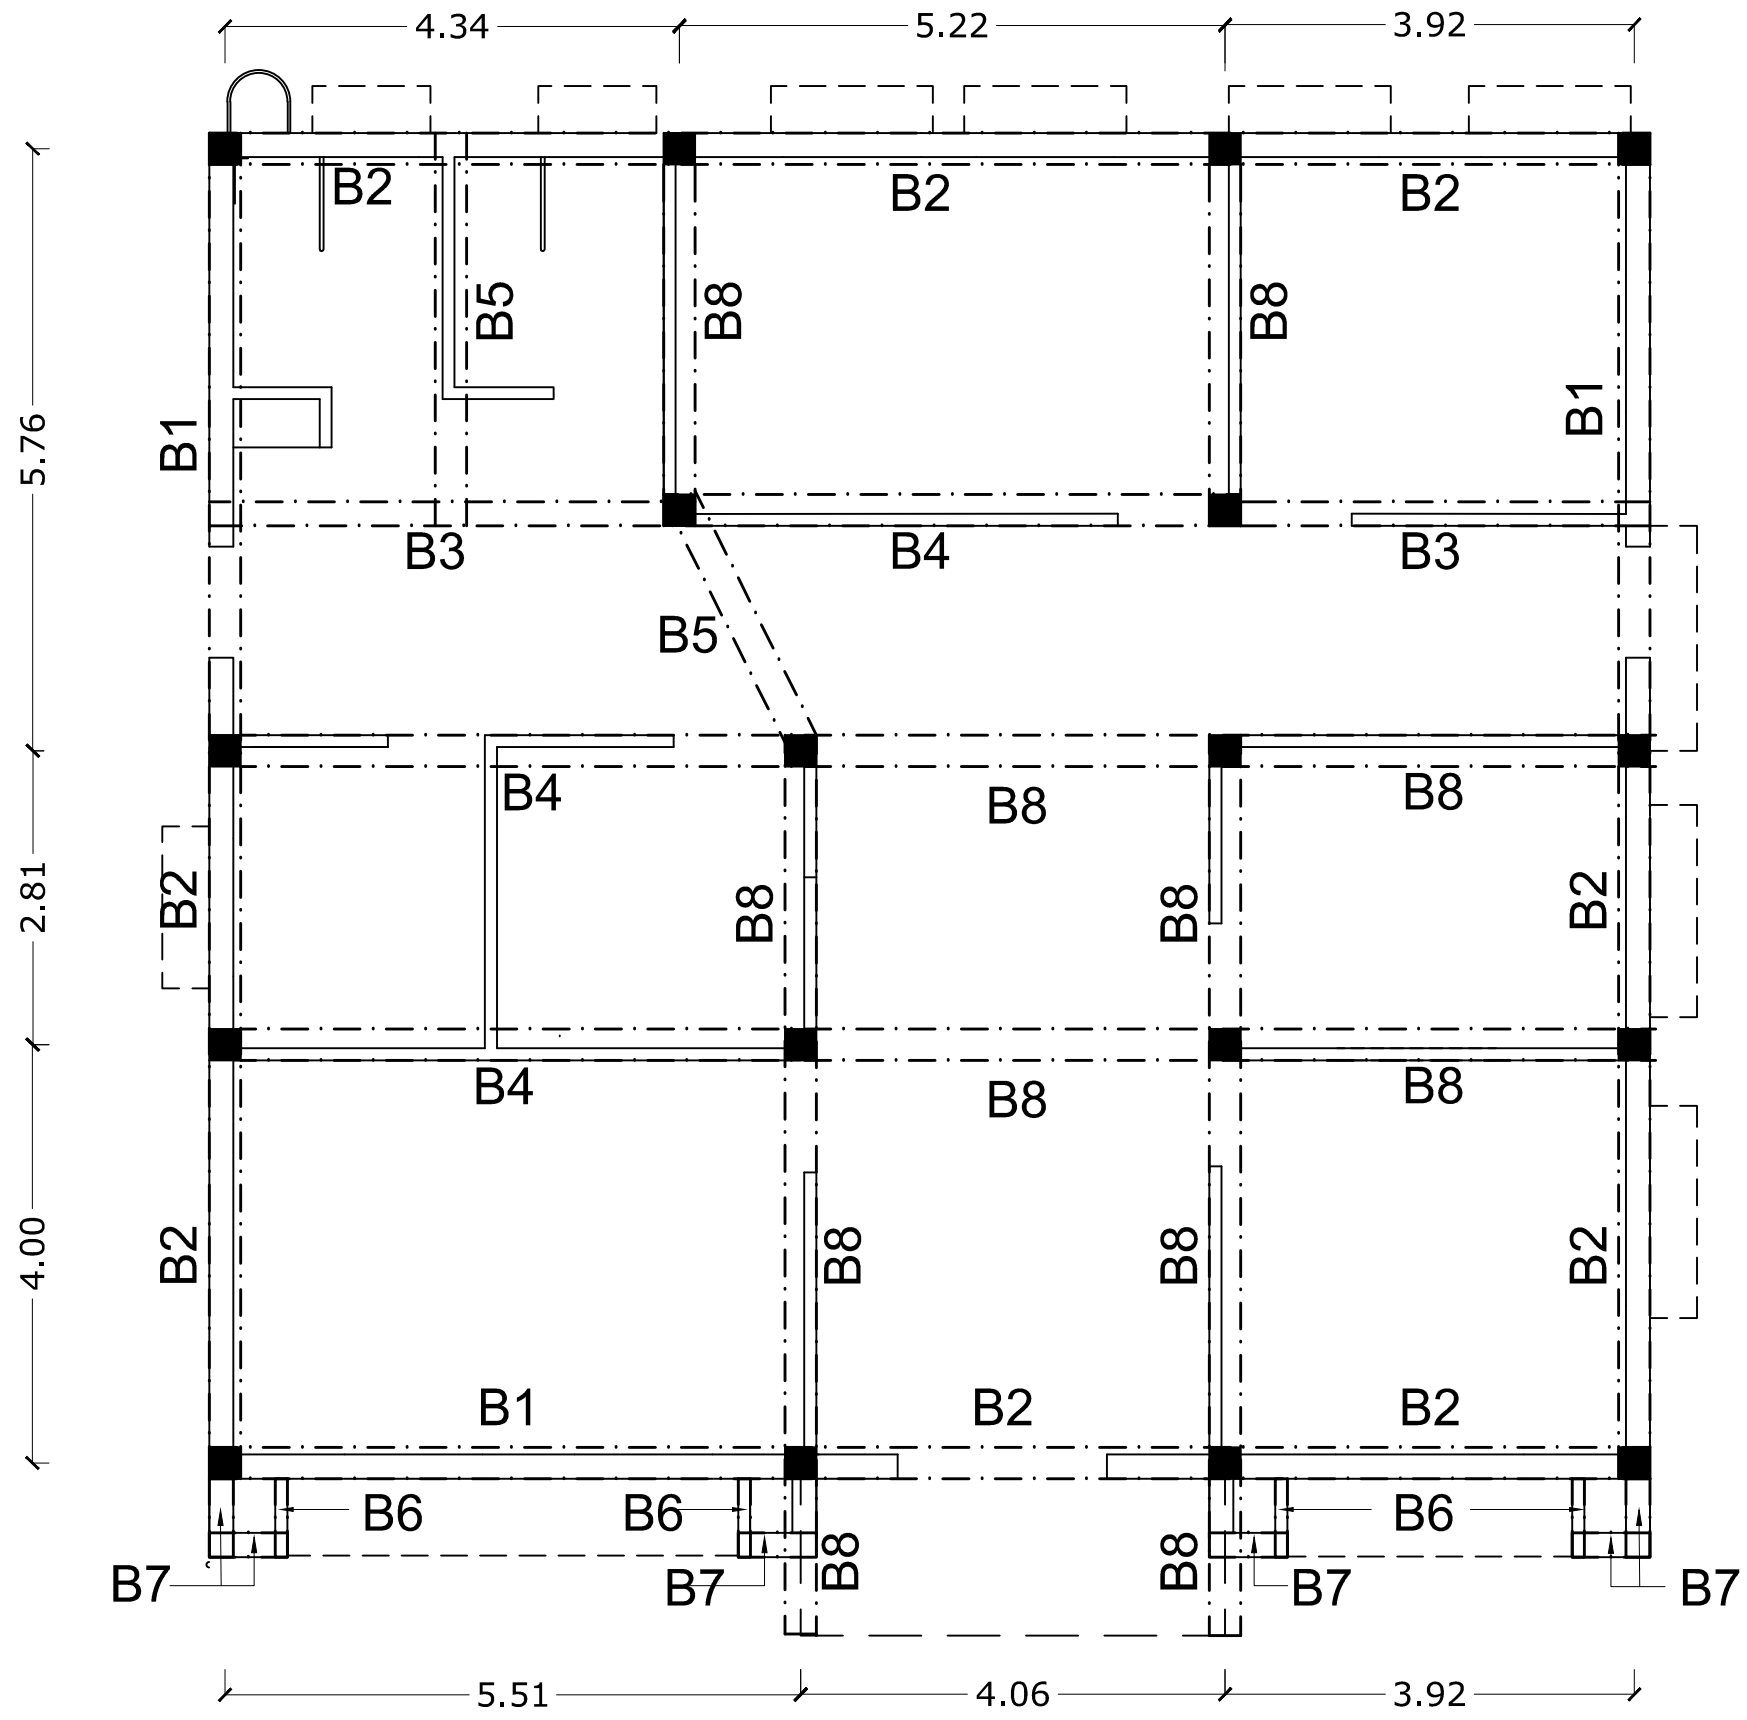


ROOF BEAM LAYOUT PLAN

- NOTES:-**
- *IF THERE IS ANY DISCREPANCY REGARDING DIMENSIONS, ARCHITECTURAL DRAWINGS MAY BE CONSULTED.
 - *WRITTEN DIMENSIONS SHOULD BE FOLLOWED
 - *MIXER & VIBRATOR ARE TO BE USED FOR ALL CONCRETE WORKS
 - *M 20 GRADE CONCRETE TO BE USED IN ALL CONCRETE WORKS.
 - *R.C.C SLAB THICKNESS IS 125mm.
 - *COVER TO REINFORCEMENT IN BEAM WILL BE 25MM ON BOTH SIDES
 - *COVER TO REINFORCEMENT OF SLAB WILL BE 20MM AT BOTTOM & 12MM AT TOP
 - *CHAIRS OF 10MM TOR STEEL IS TO BE PROVIDED TO SUPPORT CRANKED/ EXTRA STEEL BARS
 - *IN CANTILEVER SLAB & BEAM, COUNTER WEIGHT STEEL WILL BE 1/4 TIMES THE LENGTH OF CANTILEVER
 - *LENGTH OF EXTRA BAR AT CONTINUOUS SUPPORT OF BEAM WILL BE L/3 ON BOTH SIDES FROM CENTER OF SUPPORT, WHERE L IS SPAN FROM C/C
 - *LENGTH OF EXTRA BAR AT CONTINUOUS SUPPORT OF SLAB WILL BE L/4 ON BOTH SIDES FROM CENTER OF SUPPORT, WHERE L IS SPAN FROM C/C
 - *DEVELOPMENT LENGTH(L_d) OF STEEL IS 57 TIMES THE DIAMETER OF THE BAR.
 - *AT SUPPORT, CRANK WILL START AT L/5 FROM CENTER OF SUPPORT, WHERE L IS SPAN FROM C/C
 - *MINIMUM SPACING BETWEEN TWO LAYERS OF REINFORCEMENT IN BEAMS WILL BE 25MM
 - *WHEN TWO BEAMS HAVE DIFFERENT STEEL AT ONE SUPPORT, MAXIMUM OF THE TWO IS TO BE PROVIDED UPTO L/3 OF NEXT SPAN.
 - *STEEL REINFORCEMENT IS Fe 500 D
 - *NOT MORE THAN 50% AREA OF STEEL BARS SHALL BE SPLICED AT ONE SECTION.


ENGINEER:-				
CLIENT:-				
XEN ZILA PARISAD, AMBALA				
PROJECT:-				
STRUCTURAL DRAWING OF HEALTH WELLNESS CENTRE AT VILLAGE ZAFFAR PUR DISTT. AMBALA				
TITLE:-				
HEALTH WELLNESS CENTRE				
SUB TITLE:-			DRG NO:-	
GROUND FLOOR ROOF BEAMS LAYOUT PLAN			JC/ZPHS/AMB/2649/06	
SCALE :-	DATE :-	DRN BY:-	DSN BY:-	CKD. BY:-
1 :100	28-MAY-2025	JAYA	JASBIR	KULBHUSHAN
 JC TECHNOCRATS PVT. LTD. (Formerly known as Jindals Consortium, Since 1990) STRUCTURAL ENGINEERS, HIGHWAY & BRIDGE DESIGNERS, PROJECT MANAGEMENT CONSULTANTS ROAD SAFETY AUDITORS, PROOF CONSULTANTS, SURVEYORS AND SOIL INVESTIGATORS REGD. OFF. : S. C. P. 4, VIKAS VIHAR, AMBALA CITY-130001, HARYANA. PHN: 0171-2559913, MOB: 9896559913 DELHI : 4 GRI, GREEN VIBRA APARTMENTS, SECTOR 19, POCKET-2, DWARKA, NEW DELHI. MOB:-91-99961-70914 Mob:- 8199920708, 9896559913, e-mail: jindalstructure@gmail.com, jindals13@gmail.com, Web: www.jindalsconsortium.in				

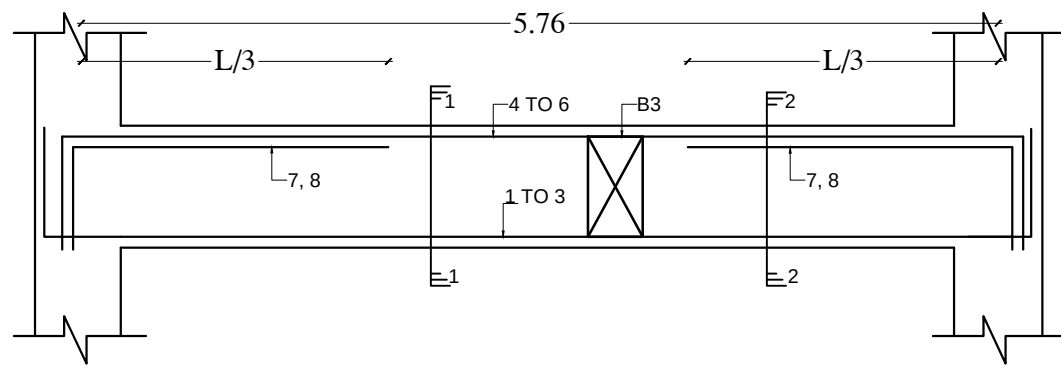


ROOF BEAM B-1

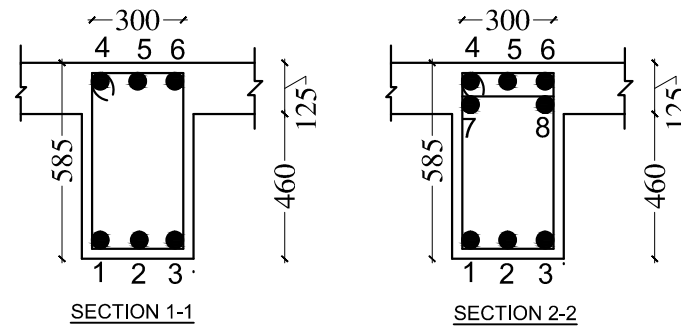


BAR NO :- 1 TO 6 - 16Ø TOR MAIN STEEL
 BAR NO :- 7, 8 - 16Ø EXTRA BAR AT TOP FACE ON SUPPORT
 RINGS :- 8Ø TOR 2 LEGGED @ 100mm C/C 12 NOS. FROM SUPPORTS
ROOF BEAM -B1 @150mm IN MIDDLE

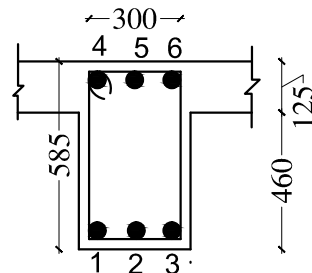


BAR NO :- 1 TO 6 -16Ø TOR MAIN STEEL.
 RINGS :- 8Ø TOR 2 LEGGED@100 C/C 12 NOS. FROM SUPPORT
ROOF BEAM -B2 @150C/C IN MIDDLE

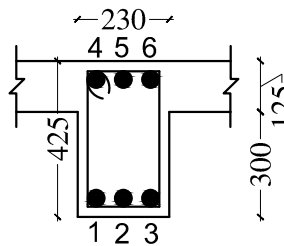


BAR NO :- 1 TO 6 -16Ø TOR MAIN STEEL.
 RINGS :- 8Ø TOR 2 LEGGED@100 C/C 9 NOS. FROM SUPPORT
ROOF BEAM -B3 @150C/C IN MIDDLE

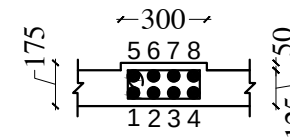


BAR NO :- 1 TO 8 - 16Ø TOR MAIN STEEL
 RINGS :- 8Ø TOR 2 LEGGED @ 150mm C/C THROUGHOUT
ROOF BEAM -B5

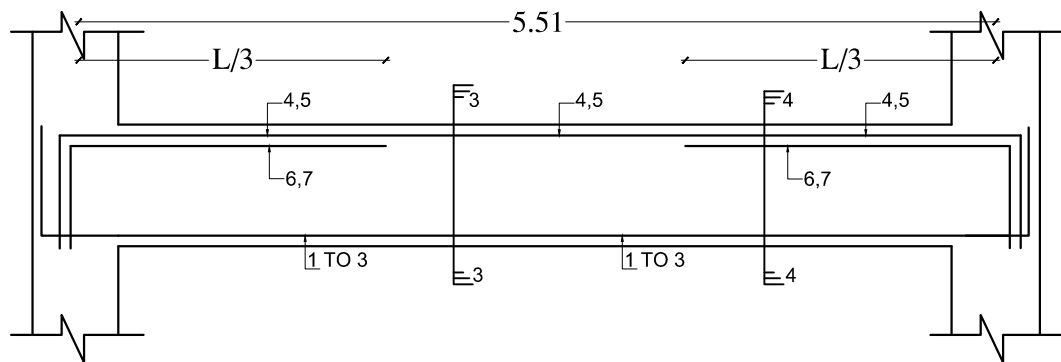

ROOF BEAM B-4

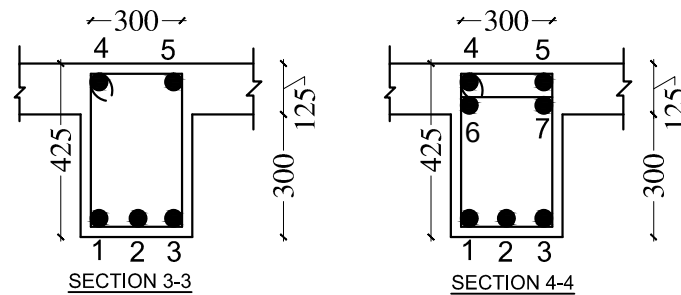


BAR NO :- 1 TO 5 - 16Ø TOR MAIN STEEL
 BAR NO :- 6, 7 - 16Ø EXTRA BAR AT TOP FACE ON SUPPORT
 RINGS :- 8Ø TOR 2 LEGGED @ 100mm C/C 11 NOS. FROM SUPPORTS
ROOF BEAM -B4 @150mm IN MIDDLE

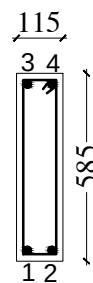


BAR NO. :- 1 TO 4 - 12ØTOR MAIN STEEL
 RING 8ØTOR 2 LEGGED @150 C/C THROUGHOUT

ROOF BEAM - B6
(DUCT BEAM)

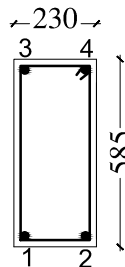


BAR NO. :- 1 TO 4 - 12ØTOR MAIN STEEL
 RING 8ØTOR 2 LEGGED @150 C/C THROUGHOUT

ROOF BEAM - B7
(DUCT BEAM)

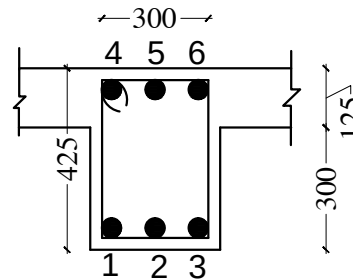


BAR NO :- 1 TO 6 -16Ø TOR MAIN STEEL.
 RINGS :- 8Ø TOR 2 LEGGED@100 C/C 9 NOS. FROM SUPPORT
ROOF BEAM -B8 @150C/C IN MIDDLE

ENGINEER :-				
CLIENT :-				
XEN ZILA PARISAD, AMBALA				
PROJECT :-				
STRUCTURAL DRAWING OF HEALTH WELLNESS CENTRE AT VILLAGE ZAFFAR PUR DISTT. AMBALA				
TITLE :-				
HEALTH WELLNESS CENTRE				
SUB TITLE :-				DRG. NO. :-
ROOF BEAMS DETAIL				JC/ZPHS/AMB/2649/07
SCALE :-	DATE :-	DRAWN BY:-	DSN BY:-	CKD. BY:-
1 :100	28-MAY-2025	JAYA	JASBIR	KULBHUSHAN
 JC TECHNOCRATS PVT. LTD. (Formerly known as Jindals Consortium, Since 1990) STRUCTURAL ENGINEERS, HIGHWAY & BRIDGE DESIGNERS, PROJECT MANAGEMENT CONSULTANTS, ROAD, SAFETY AUDITORS, PROOF CONSULTANTS, SURVEYORS AND SOIL INVESTIGATORS BRIDGE OFF. : S. C. P. -9, VIKAS VIHAR, AMBALA CITY-13403, HARYANA. PH: 0171-255013, MOB:-91-89966-70914 DELHI : # 678, GREEN VIEW APARTMENTS, SECTOR 19, POCKET-2, DWARKA, NEW DELHI. MOB:-91-89966-70914 MO:- 8199907006, 9896550913, e-mail: jindalstructure@gmail.com, jindal13@gmail.com, Web: www.jindalconsortium.in				

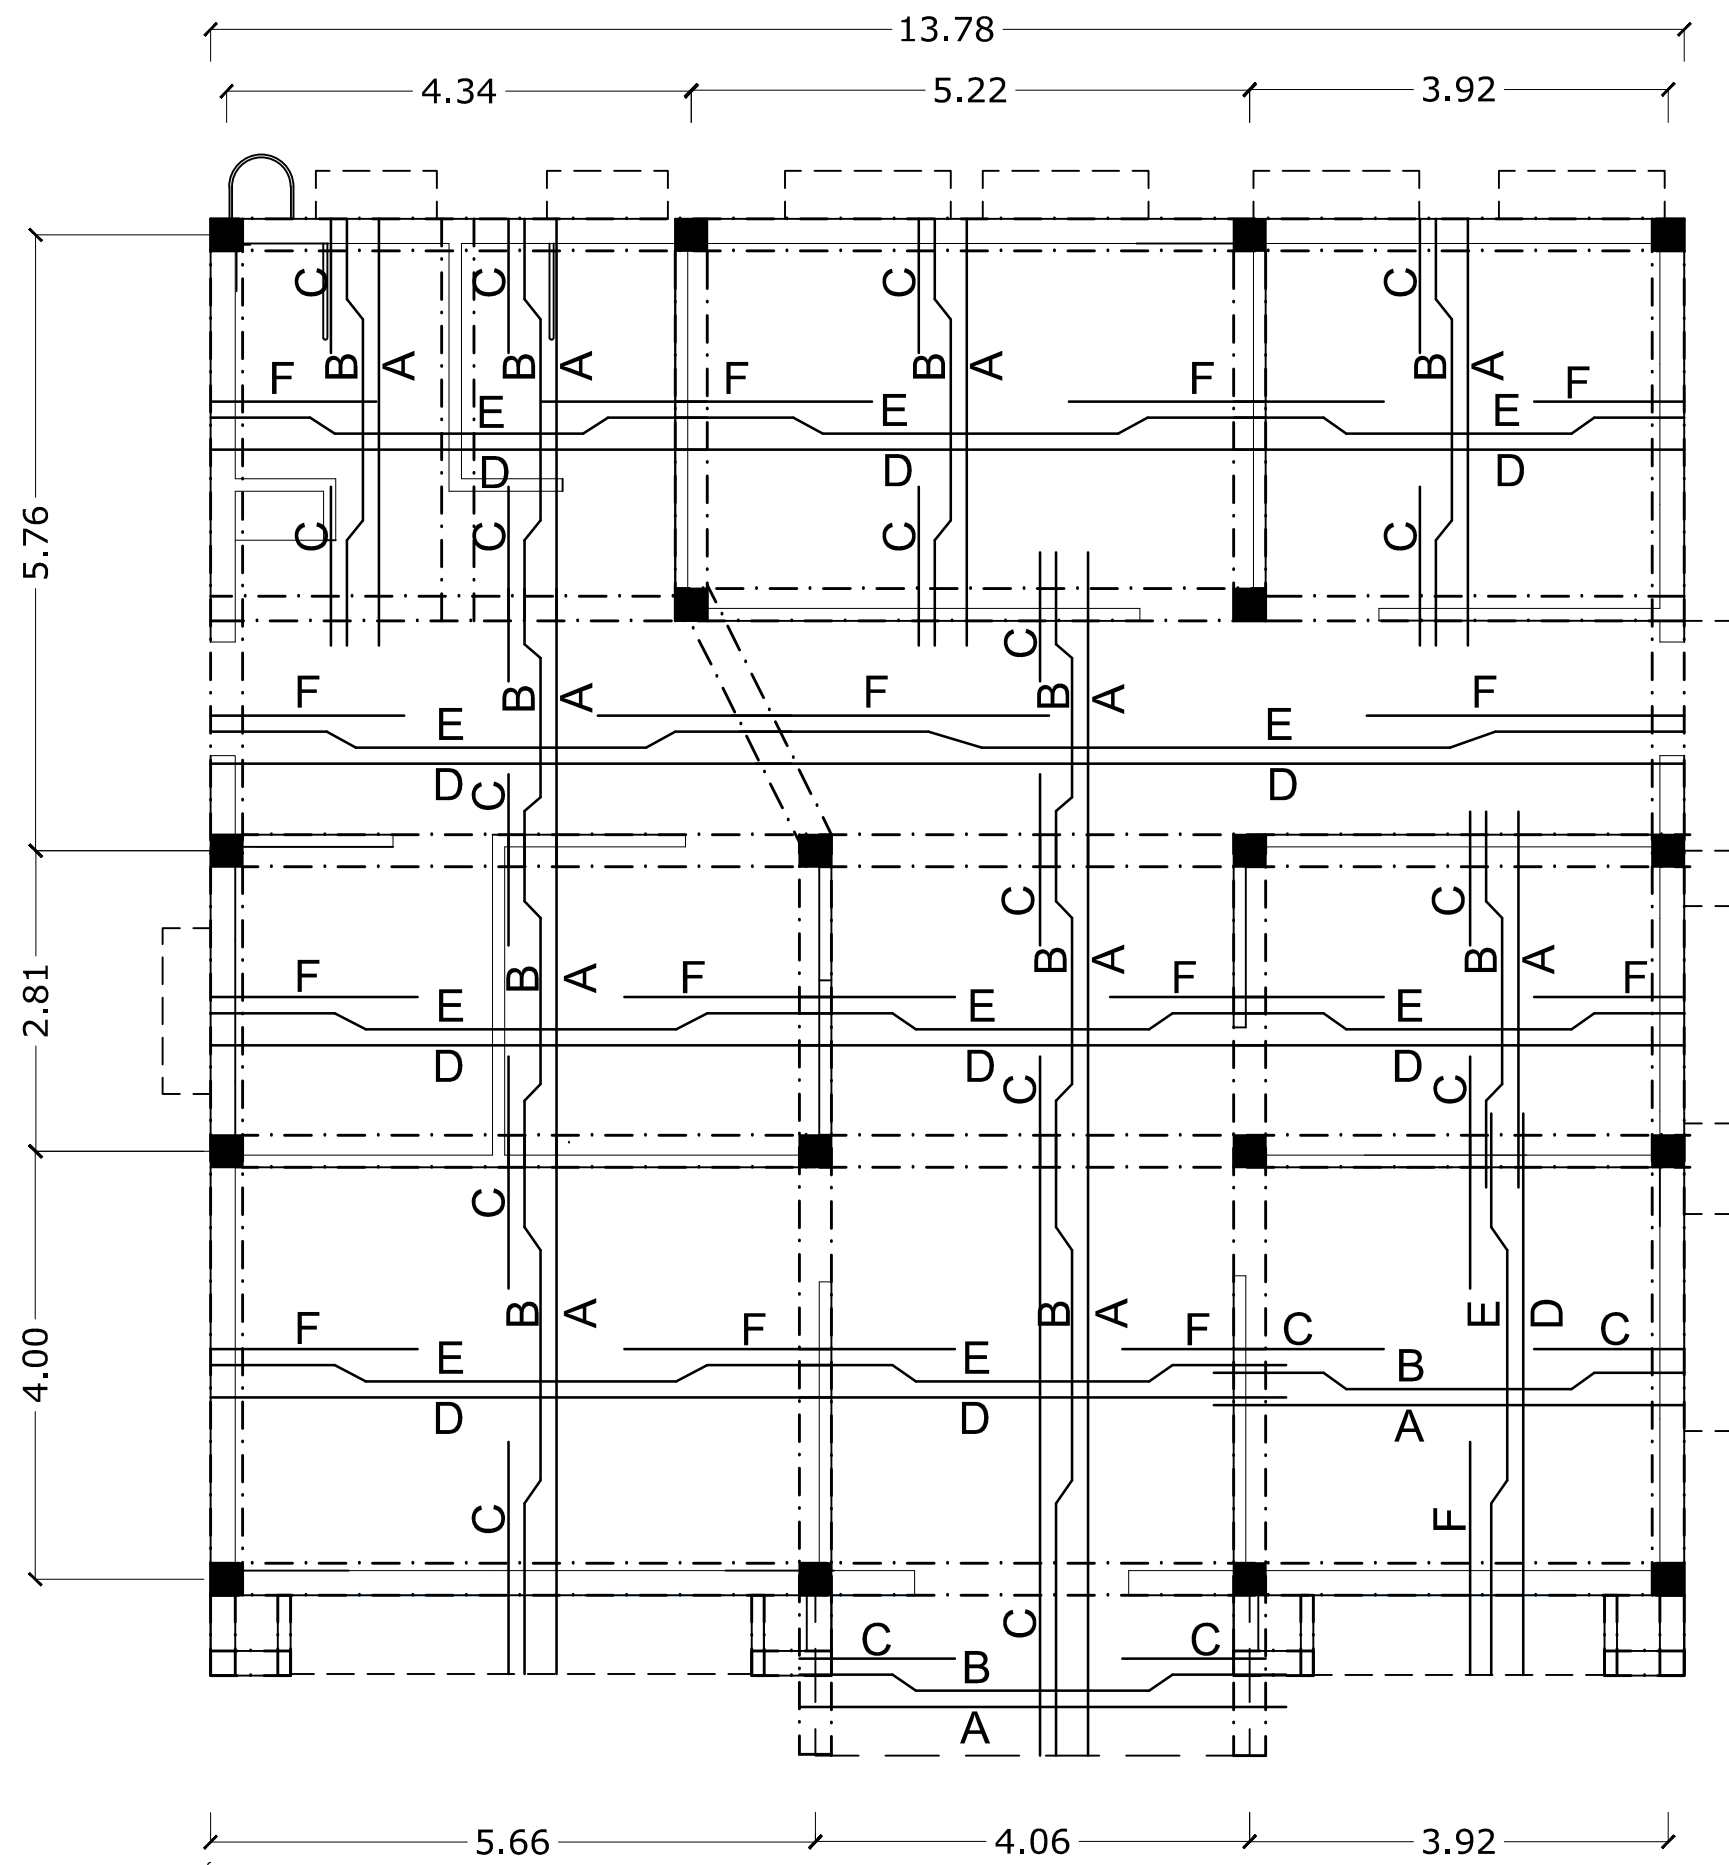


ROOF SLAB LAYOUT PLAN


SCHEDULE OF BARS				
1	A	10Ø TOR STEEL @ 300mm C/C STRAIGHT BAR AT BOTTOM FACE		
2	B	10Ø TOR STEEL @ 300mm C/C CRANKED BAR		
3	C	12Ø TOR STEEL @ 300mm EXTRA BAR AT TOP FACE		
4	D	10Ø TOR STEEL @ 380mm STRAIGHT BAR AT BOTTOM FACE		
5	E	10Ø TOR STEEL @ 380mm CRANKED BAR		
6	F	10Ø TOR STEEL @ 380mm EXTRA BAR AT TOP FACE		
7	G	10Ø TOR STEEL @ 250mm C/C DISTRIBUTION STEEL (BINDER BAR)		
NOTES:-				
*IF THERE IS ANY DISCREPANCY REGARDING DIMENSIONS, ARCHITECTURAL DRAWINGS MAY BE CONSULTED.				
*WRITTEN DIMENSIONS SHOULD BE FOLLOWED				
*MIXER & VIBRATOR ARE TO BE USED FOR ALL CONCRETE WORKS				
*M 20 GRADE CONCRETE TO BE USED IN ALL CONCRETE WORKS.				
*R.C.C SLAB THICKNESS IS 125mm.				
*COVER TO REINFORCEMENT IN BEAM WILL BE 25MM ON BOTH SIDES				
*COVER TO REINFORCEMENT OF SLAB WILL BE 20MM AT BOTTOM & 12MM AT TOP				
*CHAIRS OF 10MM TOR STEEL IS TO BE PROVIDED TO SUPPORT CRANKED/ EXTRA STEEL BARS				
*IN CANTILEVER SLAB & BEAM, COUNTER WEIGHT STEEL WILL BE 1½ TIMES THE LENGTH OF CANTILEVER				
*LENGTH OF EXTRA BAR AT CONTINOUS SUPPORT OF BEAM WILL BE L/3 ON BOTH SIDES FROM CENTER OF SUPPORT, WHERE L IS SPAN FROM C/C				
*LENGTH OF EXTRA BAR AT CONTINOUS SUPPORT OF SLAB WILL BE L/4 ON BOTH SIDES FROM CENTER OF SUPPORT, WHERE L IS SPAN FROM C/C				
*DEVELOPMENT LENGTH(L _d) OF STEEL IS 57 TIMES THE DIAMETER OF THE BAR.				
*AT SUPPORT, CRANK WILL START AT L/5 FROM CENTER OF SUPPORT, WHERE L IS SPAN FROM C/C				
*MINIMUM SPACING BETWEEN TWO LAYERS OF REINFORCEMENT IN BEAMS WILL BE 25MM				
*WHEN TWO BEAMS HAVE DIFFERENT STEEL AT ONE SUPPORT,MAXIMUM OF THE TWO IS TO BE PROVIDED UPTO L/3 OF NEXT SPAN.				
*STEEL REINFORCEMENT IS Fe 500 D				
*NOT MORE THAN 50% AREA OF STEEL BARS SHALL BE SPLICED AT ONE SECTION.				
ENGINEER:-				
CLIENT :- XEN ZILA PARISAD, AMBALA				
PROJECT:- STRUCTURAL DRAWING OF HEALTH WELLNESS CENTRE AT VILLAGE ZAFFAR PUR DISTT. AMBALA				
TITLE:- HEALTH WELLNESS CENTRE				
SUB TITLE:- GROUND FLOOR ROOF SLAB LAYOUT PLAN		DRG NO:- JC/ZPHS/AMB/2649/08		
SCALE :- 1 :100	DATE :- 28-MAY-2025	DRN BY:- JAYA	DSN BY:- JASBIR	CKD. BY:- KULBHUSHAN
 JC TECHNOCRATS PVT. LTD. (Formerly known as Jindals Consortium, Since 1990) STRUCTURAL ENGINEERS, HIGHWAY & BRIDGE DESIGNERS, PROJECT MANAGEMENT CONSULTANTS ROAD SAFETY AUDITORS, PROOF CONSULTANTS, SURVEYORS AND SOIL INVESTIGATORS REGD.OFF: S.C.F-9, VIKAS VIHAR, AMBALA CITY-134003, HARYANA. PH: 0171-2550913, MOB:-91-98966-70914 DELHI : #678, GREEN VIEW APARTMENTS, SECTOR 19, POCKET-2, DWARKA, NEW DELHI. MOB:-91-99966-70914 Mob:- 8199907006, 9896550913, e-mail: jindalstructure@gmail.com, jindals13@gmail.com, Web: www.jindalsconsortium.in				

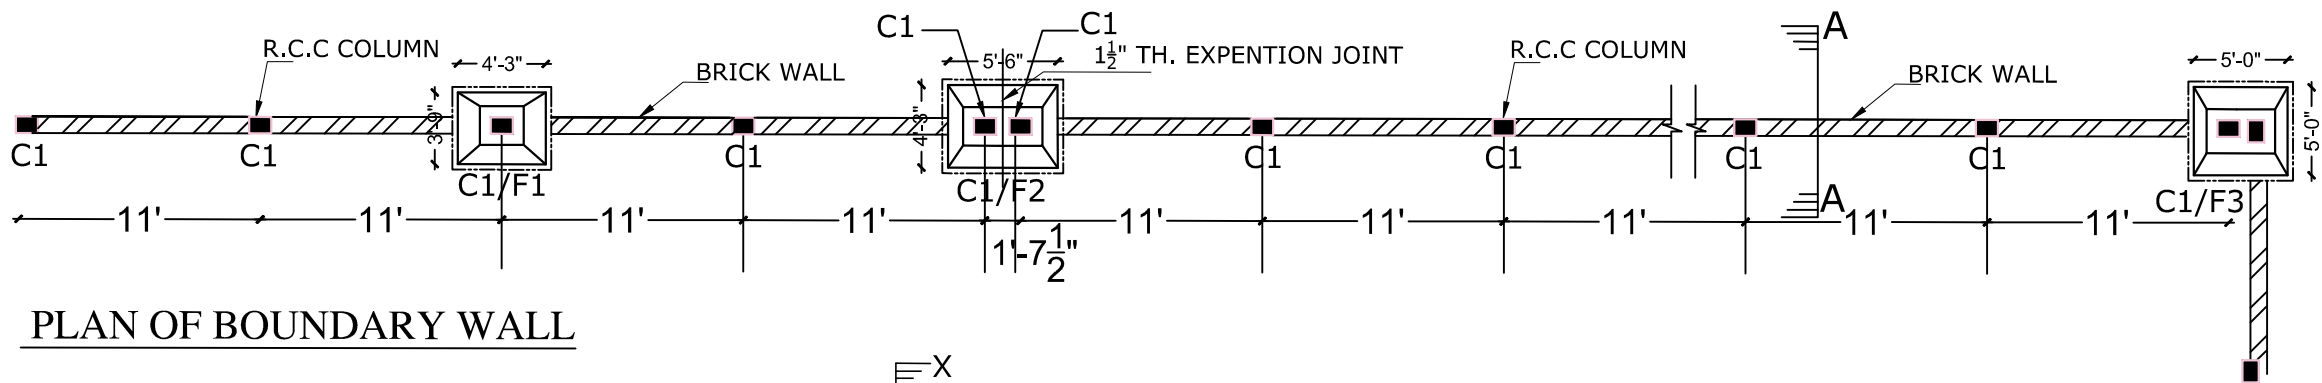


PLAN OF BOUNDARY WALL

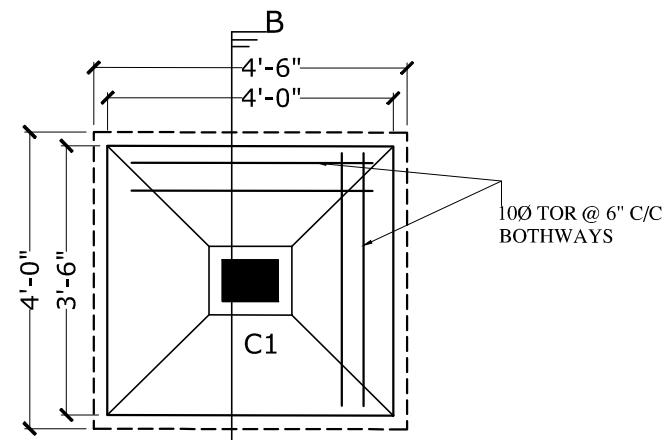



DETAIL OF FOUNDATION F1

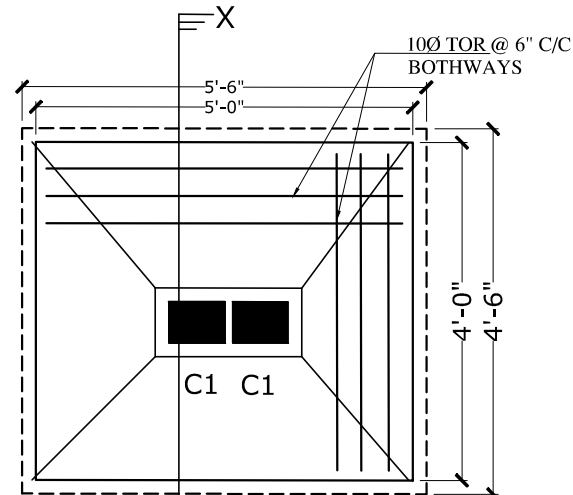


DETAIL OF FOUNDATION F2

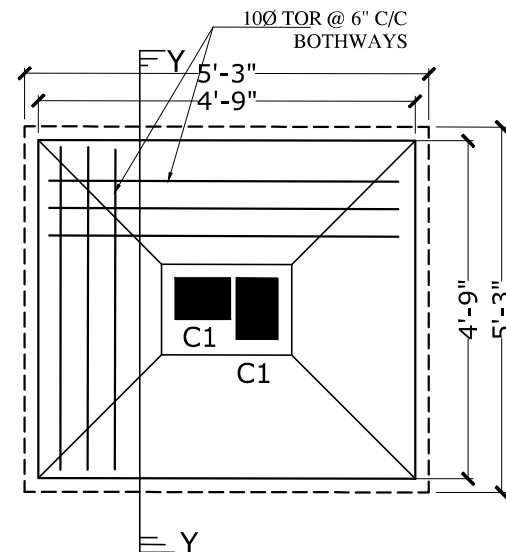


DETAIL OF FOUNDATION F3

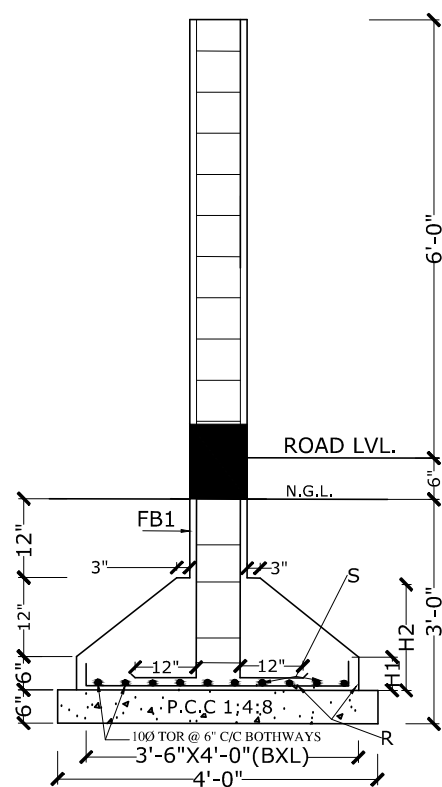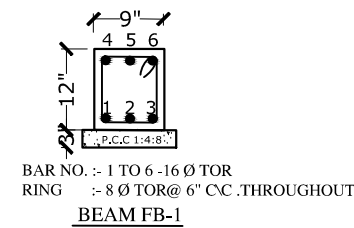


SECTION OF COLUMN AT B-B

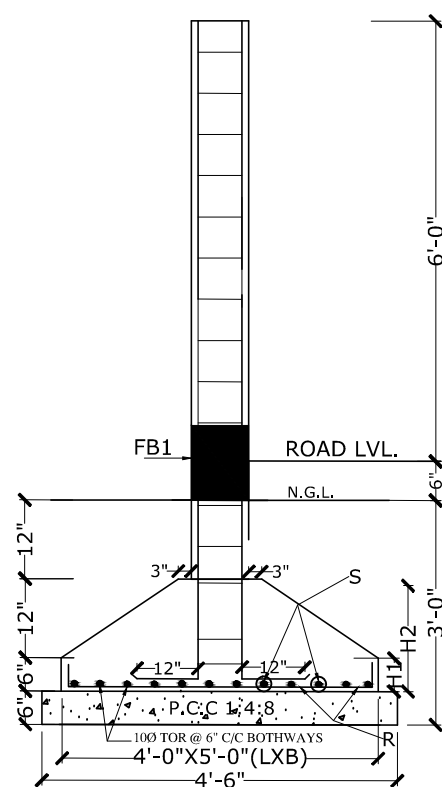

SECTION AT X-X

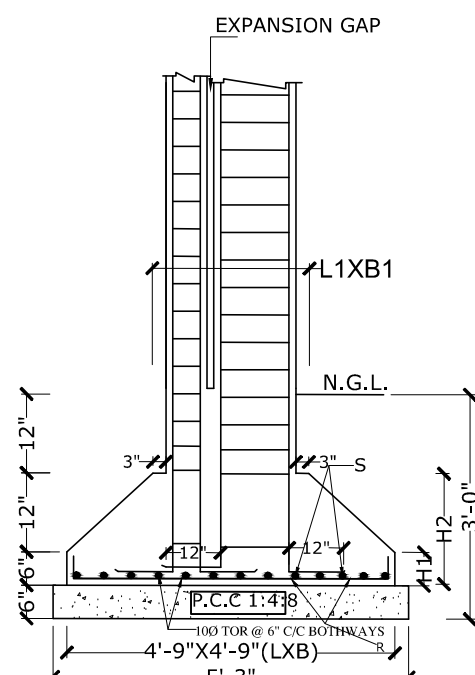

SECTION AT Y-Y

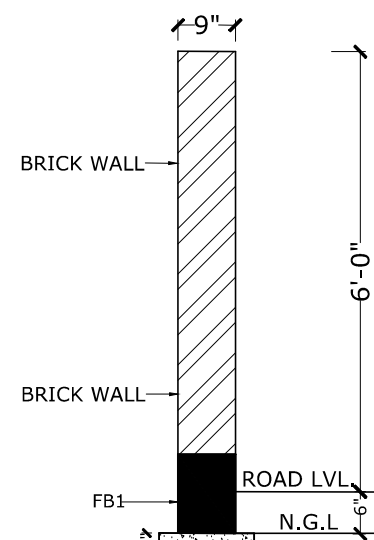

9" TH. BRICK WALL FOUNDATION.
(SECTION AT 'A-A')

COLUMN NO.	COLUMN SIZE	REINFORCEMENT DETAIL	
C1	9" X12"		
SCHEDULE FOR DETAIL OF COLUMN FOOTING			
COLUMN FOOTING	DIMENSION	REINFORCEMENT FOR FOOTING	PEDESTAL DIMENSION
	L B H1 H2 D	R S	L1 B1
F1	4'-0" 3'-6" 6" 1'-6" 3'-0"	10Ø TOR 6" C/C 10Ø TOR 6" C/C	2'-0" 1'-3"
F2	5'-0" 4'-0" 6" 1'-6" 3'-0"	10Ø TOR 6" C/C 10Ø TOR 6" C/C	3'-7 1/2" 1'-3"
F3	4'-9" 4'-9" 6" 1'-6" 3'-0"	10Ø TOR 6" C/C 10Ø TOR 6" C/C	2'-10 1/2" 1'-3"

NOTES

*IF THERE IS ANY DISCREPANCY REGARDING DIMENSIONS, ARCHITECTURAL DRAWINGS MAY BE CONSULTED.

* WRITTEN DIMENSIONS SHOULD BE FOLLOWED.

*M20 (1:1.5:3) CONCRETE TO BE USED IN ALL CONCRETE WORKS.

* Ø TOR MEANS DIAMETER IN MM FOR TOR STEEL BARS.

*STEEL SHUTTERING IS TO BE USED FOR ALL CONCRETE WORKS.

*STEEL OF COLUMN TO GO UP TO BOTTOM OF FOUNDATION WITH BEND OF 1'-0" AT BOTTOM.

*LEAN CONCRETE WILL BE 6" TH. IN MIX 1:4:8.

*LEAN CONCRETE WILL PROJECT 3" BEYOND THE R.C.C FOUNDATION.

*COVER TO REINFORCEMENT OF COLUMNS WILL BE 40 MM ON ALL FACES.

*COVER TO REINFORCEMENT OF FOUNDATION SLAB WILL BE 30 MM.

*DRAWING IS NOT TO BE SCALED.

*OVER LAP LENGTH OF STEEL IS 50 TIMES THE DIAMETER OF THE BAR.

* CEMENT MORTAR RATIO IN 9" THK. BRICK WORK IS 1:4.

*EXPANSION GAP SHOULD BE PROVIDED AFTER EVERY 100' AND AT EVERY CORNER.

ENGINEER :-	
TITLE :-	
PROJECT :-	
STRUCTURAL DRAWING OF HEALTH WELLNESS CENTRE AT VILLAGE ZAFFAR PUR DISTT. AMBALA	
TITLE :-	
BOUNDARY WALL	
SUB TITLE:-	
BOUNDARY WALL DETAIL	
DRG. NO. :-	
JC/ZPHS/AMB/2649/09	
SCALE :-	DATE :-
1:100	28-MAY-2025
DRAWN BY:-	DSN BY:-
JAYA	JASBIR
CHKD. BY:-	
KULBHUSHAN	
JC TECHNOCRATS PVT. LTD. (Formerly known as Jindals Consortium, Since 1990) STRUCTURAL ENGINEERS, HIGHWAY & BRIDGE DESIGNERS, PROJECT MANAGEMENT CONSULTANTS ROAD SAFETY AUDITORS, PROOF CONSULTANTS, SURVEYORS AND SOIL INVESTIGATORS REGD. OFF. : S. C. F. 9, VIKAS VIHAR, AMBALA CITY-134003, HARYANA, PH: 0171-2559313, MOB:-91-98966-78914 DELHI : #678, GREEN VIEW APARTMENTS, SECTOR 19, POCKET-2, DWARKA, NEW DELHI. MOB:-91-99964-78914 Mob:-919997096, 9896659913, e-mail: jindaltechnocrats@gmail.com, jindal13@gmail.com, Web: www.jindaltechnocrats.in	