

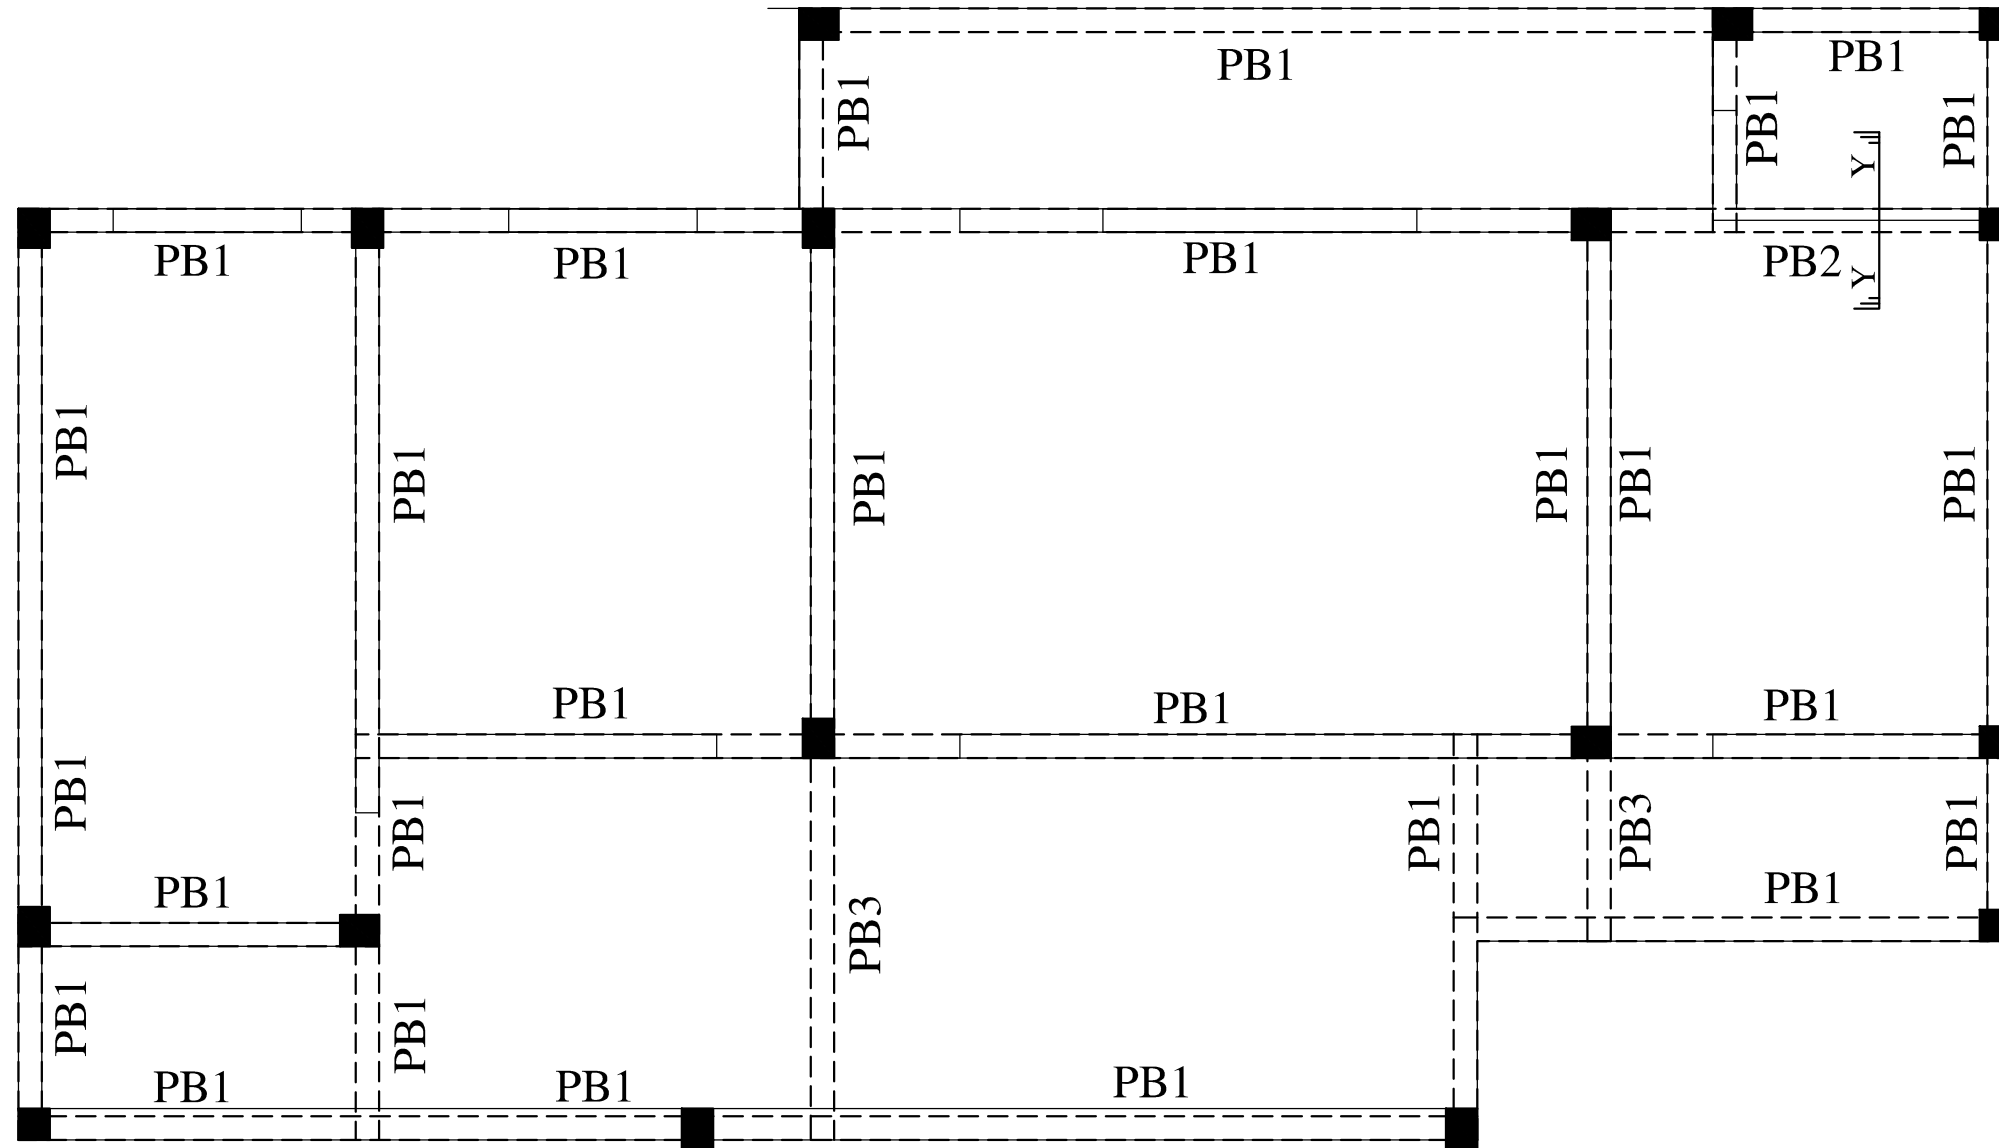



- NOTES:-
- * IF THERE IS ANY DISCREPANCY REGARDING DIMENSIONS, ARCHITECTURAL DRAWINGS MAY BE CONSULTED.
 - * WRITTEN DIMENSIONS SHOULD BE FOLLOWED.
 - * DRAWING IS NOT TO BE SCALED.
 - * M-20 (1:1½:3) GRADE CONCRETE TO BE USED IN ALL CONCRETE WORKS.
 - * Ø TOR MEANS DIAMETER IN MM FOR TOR STEEL BARS.
 - * STEEL SHUTTERING IS TO BE USED FOR ALL CONCRETE WORKS.
 - * LEAN CONCRETE WILL PROJECT 75 BEYOND THE R.C.C BEAMS
 - * DEVELOPMENT LENGTH (L_d) OF STEEL IS 57 TIMES THE DIAMETER OF THE BAR.
 - * CEMENT MORTAR RATIO IN 230 TH. BRICK WORK IS 1:6.
 - * CEMENT MORTAR RATIO IN 115 TH.BRICK WORK IS 1:4.
 - * EARTH FILLING IN FOUNDATIONS SHOULD BE DONE EQUALLY ON BOTH SIDES OF FOUNDATION WALL.
 - * WHEREVER PLINTH BEAM LIES DIRECTLY ON EARTH , P.C.C 100 THICK (1:4:8) MAY BE LAID.
 - *STEEL BARS OF PLINTH BEAMS SHALL BE L-SHAPED OVER LAPED BY A LENGTH OF 49 TIMES THE DIAMETER OF THE BARS AT ALL CORNERS & JUNCTIONS.

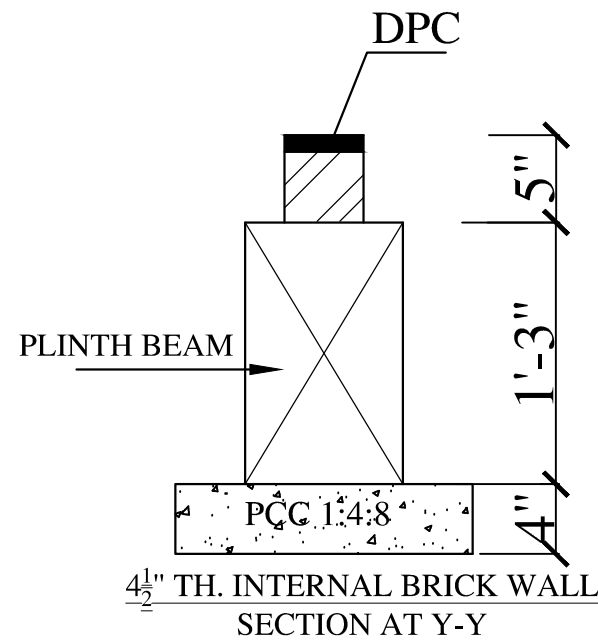


PLINTH BEAMS LAYOUT PLAN &DETAIL

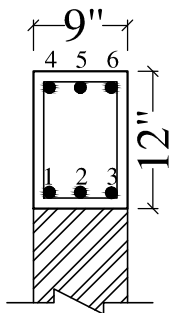

BAR NO :- 1 TO 6- 12Ø TOR MAIN STEEL
RINGS :- 8Ø TOR 2 LEGGED @ 4" C/C 7 NOS. FROM SUPPORTS
BEAM -PB1 @ 6" C/C IN MIDDLE

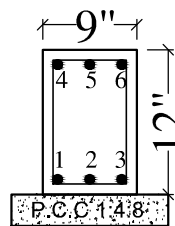

BAR NO :- 1 TO 6- 16Ø TOR MAIN STEEL
RINGS :- 8Ø TOR 2 LEGGED @ 4" C/C 7 NOS. FROM SUPPORTS
BEAM -PB2 @ 6" C/C IN MIDDLE

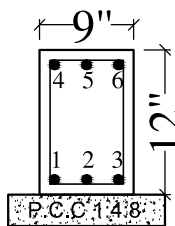

BAR NO :- 1 TO 6- 25Ø TOR MAIN STEEL
RINGS :- 8Ø TOR 2 LEGGED @ 4" C/C 7 NOS. FROM SUPPORTS
BEAM -PB3 @ 6" C/C IN MIDDLE

ENGINEER :-				
CLIENT :- XEN PANCHAYATI RAJ,NUH				
PROJECT :- STRUCTURAL DRAWINGS OF PANCHYAT GHAR AT VILLAGE GHASERA,DISTT.NUH				
TITLE :- PANCHYAT GHAR				
SUB TITLE :- PLINTH BEAM LAYOUT PLAN &DETAIL			DRG. NO. :- JC/PR/NUH/2420/3	
SCALE :- 1 : 100	DATE :- 9 July 2022	DRAWN BY:- SIMRAN	DSN BY:- JASBIR	CKD. BY:- K.B. MANOCHA
 JC TECHNOCRATS PVT. LTD (Formerly known as Jindals Consortium, Since 1990) STRUCTURAL ENGINEERS, HIGHWAY & BRIDGE DESIGNERS, PROJECT MANAGEMENT CONSULTANTS ROAD SAFETY AUDITORS, PROOF CONSULTANTS, SURVEYORS AND SOIL INVESTIGATORS REGD.OFF: S.C.F-9, VIKAS VIHAR, AMBALA CITY-134003, HARYANA. PH: 0171-2550913, MOB:-91-98966-7091 DELHI : # 678, GREEN VIEW APARTMENTS, SECTOR 19, POCKET-2, DWARKA, NEW DELHI. MOB:-91-99964-7091 Mob:- 8199907006, 9896550913, e-mail: jindalstructure@gmail.com, jindals13@gmail.com, Web: www.jindalsconsortium.com				