


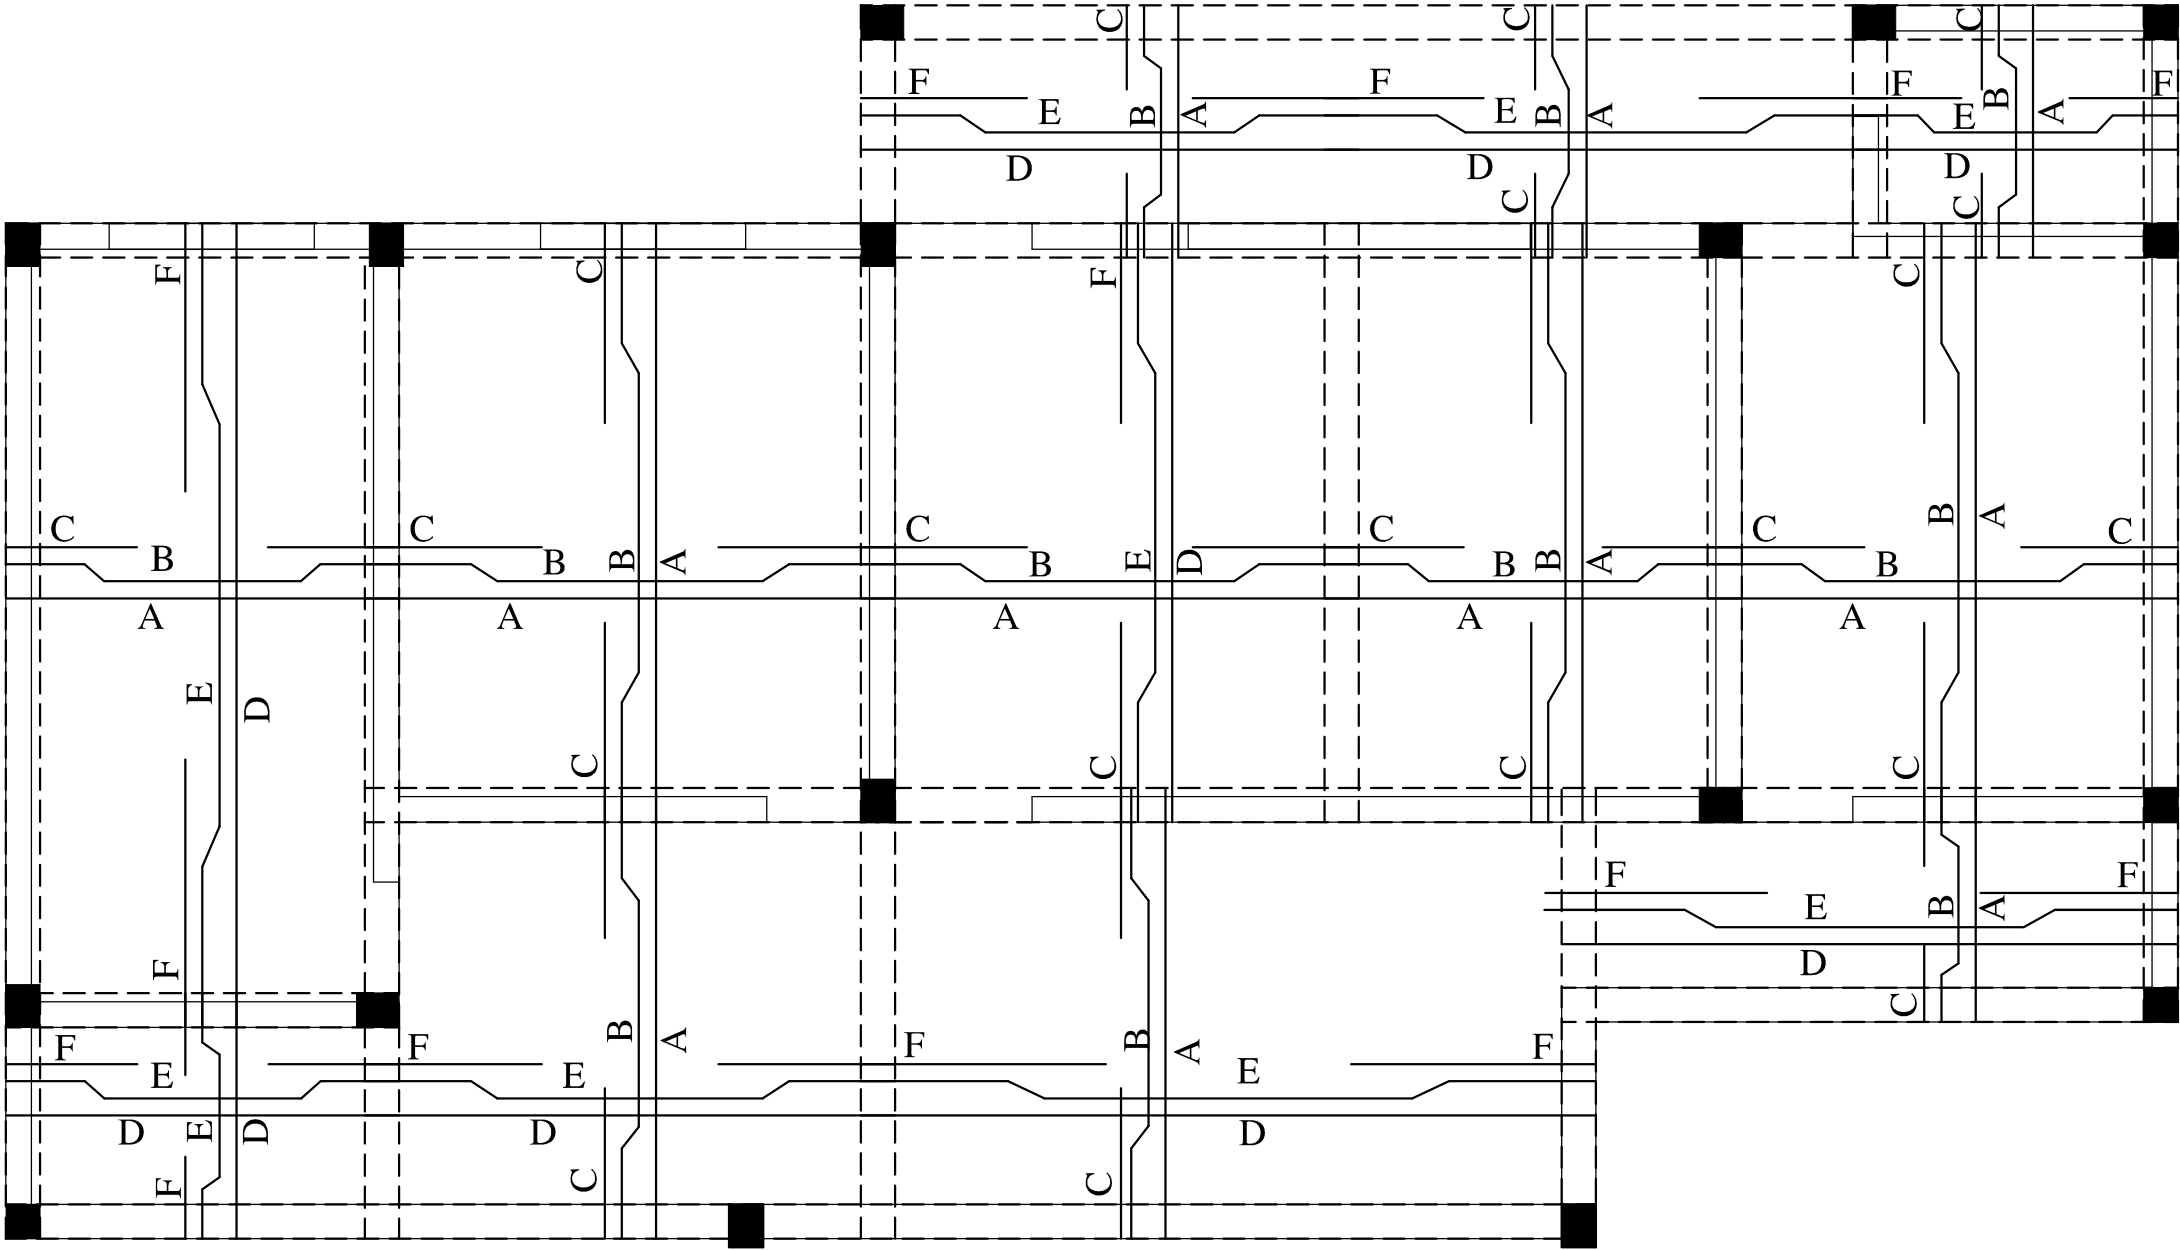

ROOF SLAB LAYOUT PLAN

SCHEDULE OF BARS				
1	A	10Ø TOR STEEL @ 12" C/C STRAIGHT BAR AT BOTTOM FACE		
2	B	10Ø TOR STEEL @ 12" C/C CRANKED BAR		
3	C	12Ø TOR STEEL @ 12" EXTRA BAR AT TOP FACE		
4	D	10Ø TOR STEEL @ 14" STRAIGHT BAR AT BOTTOM FACE		
5	E	10Ø TOR STEEL @ 14" CRANKED BAR		
6	F	10Ø TOR STEEL @ 14" EXTRA BAR AT TOP FACE		
NOTES:- * IF THERE IS ANY DISCREPANCY REGARDING DIMENSIONS, ARCHITECTURAL DRAWINGS MAY BE CONSULTED. * WRITTEN DIMENSIONS SHOULD BE FOLLOWED. * DRAWING IS NOT TO BE SCALED. * M-20 (1:1½:3) GRADE CONCRETE TO BE USED IN ALL CONCRETE WORKS. * Ø TOR MEANS DIAMETER IN MM FOR TOR STEEL BARS. * STEEL SHUTTERING IS TO BE USED FOR ALL CONCRETE WORKS. * LEAN CONCRETE WILL BE 4" TH. IN MIX 1:4:8. * LEAN CONCRETE WILL PROJECT 3" BEYOND THE R.C.C FOUNDATION. * COVER TO REINFORCEMENT OF COLUMNS WILL BE 1½" ON ALL FACES. * COVER TO REINFORCEMENT OF FOUNDATION SLAB WILL BE 2". * DEVELOPMENT LENGTH(L_d) OF STEEL IS 57 TIMES THE DIAMETER OF THE BAR. * CEMENT MORTAR RATIO IN 9" TH. BRICK WORK IS 1:6. * CEMENT MORTAR RATIO IN 4½" TH. BRICK WORK IS 1:4. * WHEREVER THE GAP BETWEEN TWO FOOTINGS IS LESS THAN 900mm,THE LEAN CONCRETE (P.C.C)SHALL BE LAID CONTINUOUSLY. * EARTH FILLING IN FOUNDATIONS SHOULD BE DONE EQUALLY ON BOTH SIDES OF FOUNDATION WALL. * WHEREVER PLINTH BEAM LIES DIRECTLY ON EARTH, P.C.C 4" THICK (1:4:8) MAY BE LAID. * STEEL BARS OF PLINTH BEAMS SHALL BE L-SHAPED OVER LAPED BY A LENGTH OF 57 TIMES THE DIAMETER OF THE BARS AT ALL CORNERS & JUNCTIONS. * NOT MORE THAN 50% BARS SHALL BE SPLICED AT ONE SECTION.				
ENGINEER :-				
CLIENT :- XEN PANCHAYATI RAJ,NUH				
PROJECT :-				
STRUCTURAL DRAWINGS OF PANCHYAT GHAR AT VILLAGE GHASERA,DISTT.NUH				
TITLE :-				
PANCHYAT GHAR				
SUB TITLE :-		DRG. NO. :-		
ROOF SLAB LAYOUT PLAN		JC/PR/NUH/2420/5		
SCALE :-	DATE :-	DRAWN BY:-	DSN BY:-	CKD. BY:-
1 : 100	9 July 2022	SIMRAN	JASBIR	K.B. MANOCHA
JC TECHNOCRATS PVT. LTD. (Formerly known as Jindals Consortium, Since 1990) STRUCTURAL ENGINEERS, HIGHWAY & BRIDGE DESIGNERS, PROJECT MANAGEMENT CONSULTANTS ROAD SAFETY AUDITORS, PROOF CONSULTANTS, SURVEYORS AND SOIL INVESTIGATORS REGD.OFF. : S. C. P-9, VIKAS VIHAR, AMBALA CITY-134003, HARYANA. PH: 0171-2550913, MOB:-+91-98966-70914 DELHI : # 678, GREEN VIEW APARTMENTS, SECTOR 19, POCKET-2, DWARKA, NEW DELHI. MOB:-91-99964-70914 Mob:- 8199907006, 9896550913, e-mail: jindalstructure@gmail.com, jindals13@gmail.com, Web: www.jindalsconsortium.in				