
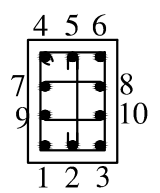
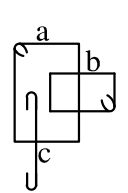
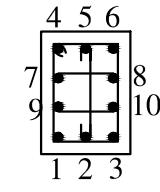
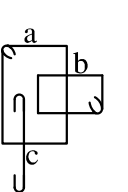
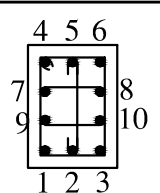
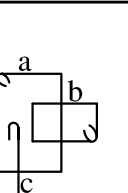
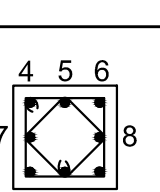
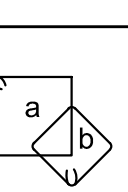
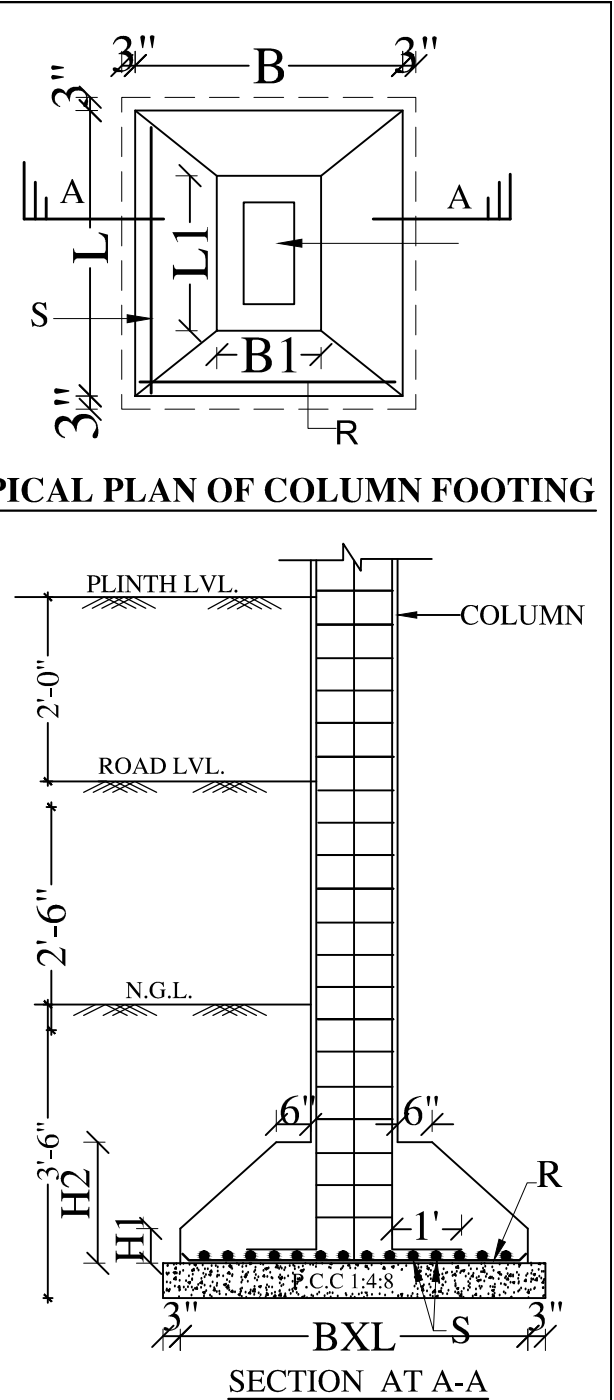
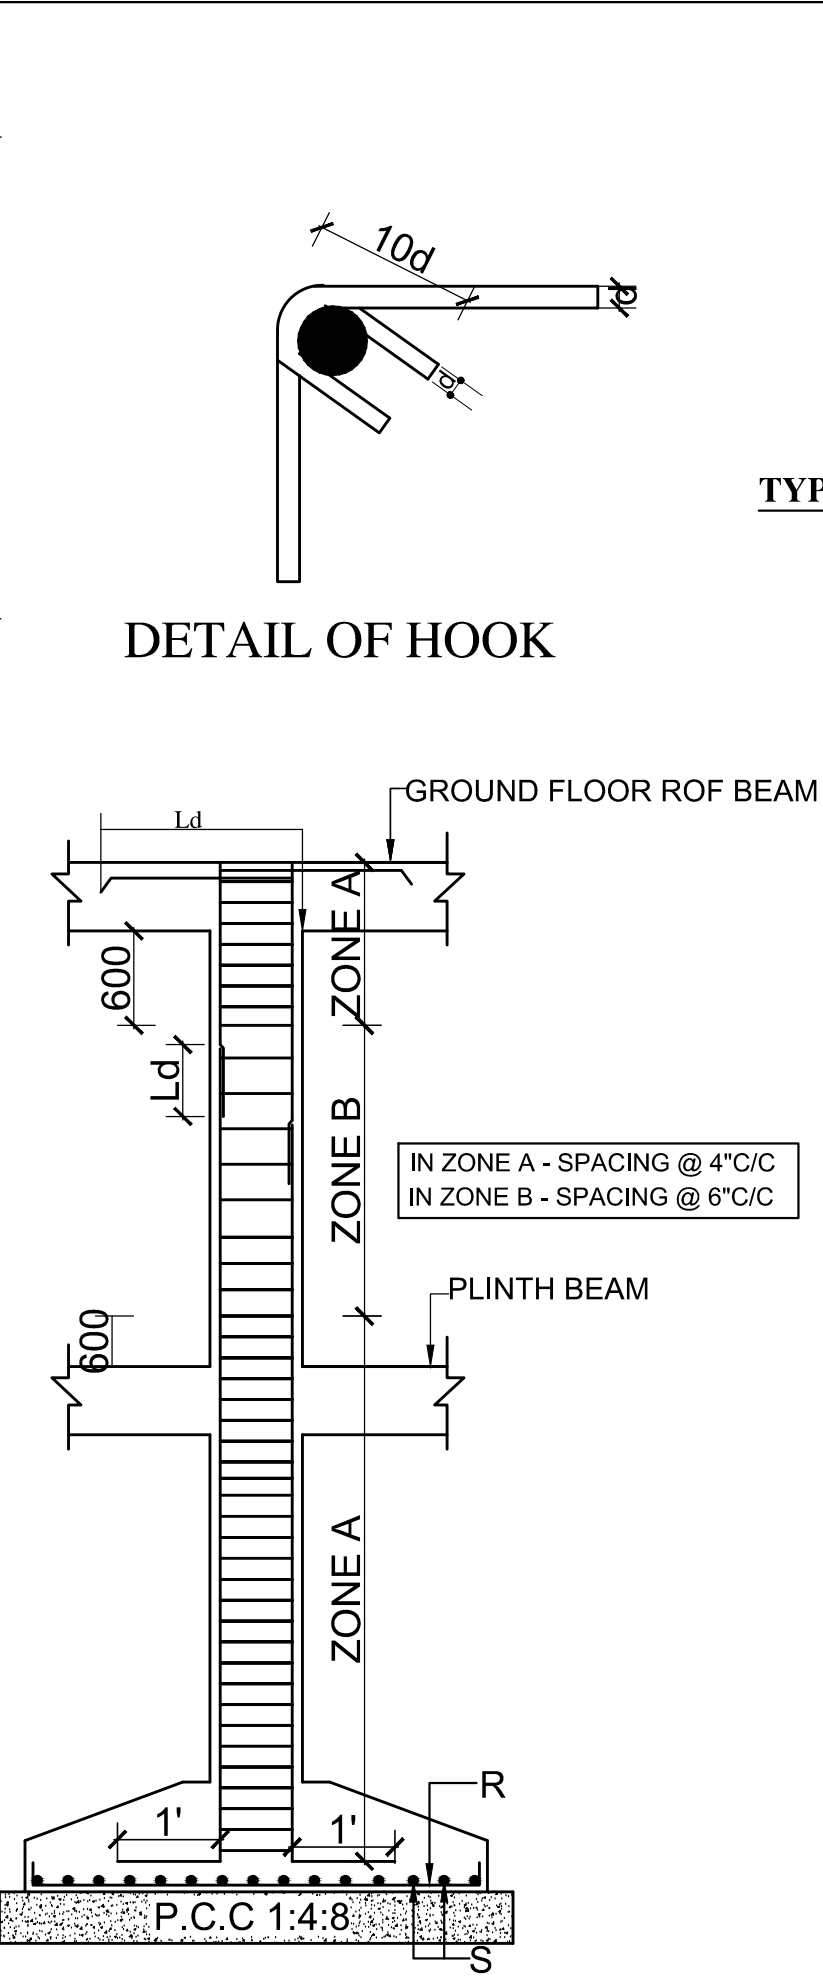
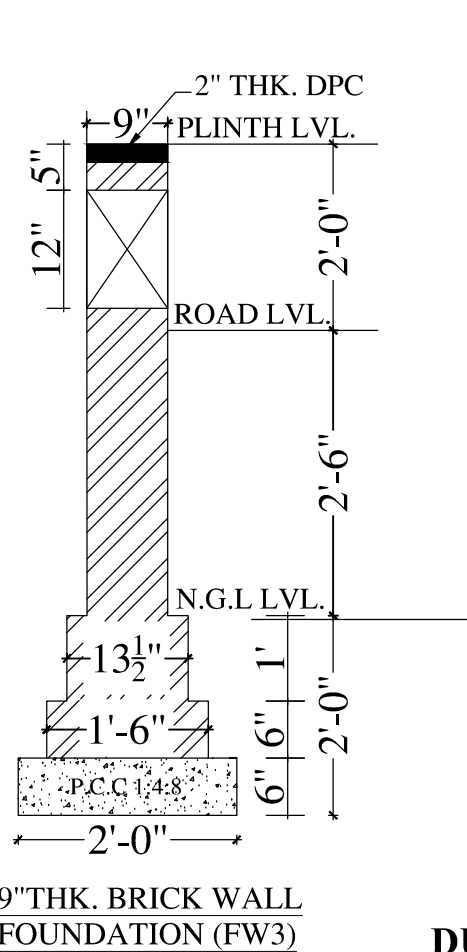


COLUMN NO.	COLUMN SIZE	REINFORCEMENT DETAIL	RING DETAIL
C1		 BAR NO. :- 1 TO 10 - 20Ø TOR RINGS:- 8Ø TOR @4" C/C AT TOP&BOTTOM @6" C/C IN MIDDLE	 (a+b+c)
C2	12"X15"	 BAR NO. :- 1 TO 6 - 20Ø TOR BAR NO. :- 7 TO 10 - 16Ø TOR RINGS:- 8Ø TOR @4" C/C AT TOP&BOTTOM @6" C/C IN MIDDLE	 (a+b+c)
C3	12"X15"	 BAR NO. :- 1 TO 10 - 16Ø TOR RINGS:- 8Ø TOR @4" C/C AT TOP&BOTTOM @6" C/C IN MIDDLE	 (a+b+c)
C4	12"X12"	 BAR NO. :- 1 TO 8 - 16Ø TOR RINGS:- 8Ø TOR @4" C/C AT TOP&BOTTOM @6" C/C IN MIDDLE	 (a+b)

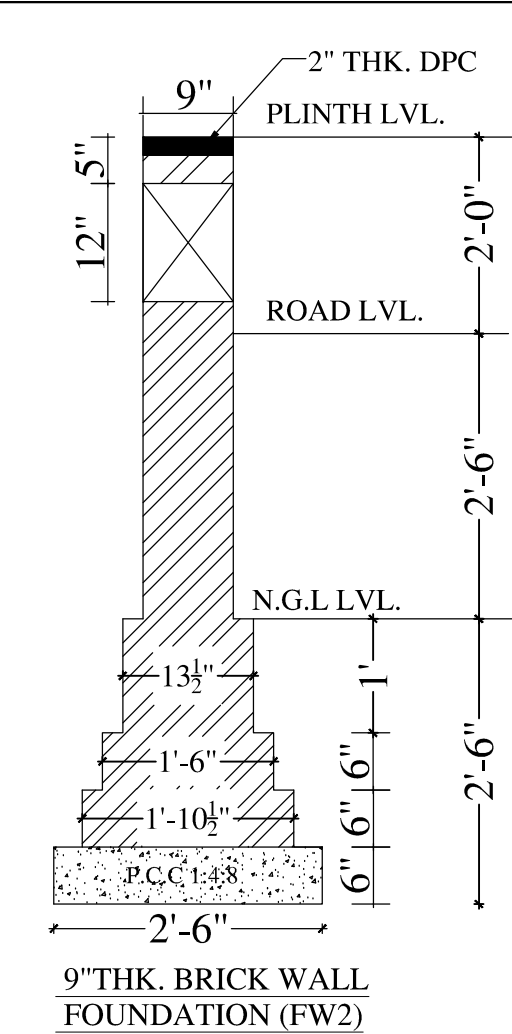

ENGINEER :-				
CLIENT :- XEN PANCHAYATI RAJ,NUH				
PROJECT :- STRUCTURAL DRAWINGS OF PANCHYAT GHAR AT VILLAGE GHASERA,DISTT.NUH				
TITLE :- PANCHYAT GHAR				
SUB TITLE :- COLUMN STEEL DETAIL			DRG. NO. :- JC/PR/NUH/2420/2	
SCALE :- 1:100	DATE :- 9 July 2022	DRAWN BY:- SIMRAN	DSN BY:- JASBIR	CKD. BY:- K.B. MANOCHA
 JC TECHNOCRATS PVT. LTD. (Formerly known as Jindals Consortium, Since 1990) STRUCTURAL ENGINEERS, HIGHWAY & BRIDGE DESIGNERS, PROJECT MANAGEMENT CONSULTANTS ROAD SUPPLY AUDITORS, PROOF CONSULTANTS, SURVEYORS AND SOIL INVESTIGATORS REGD OFF. : S.C.F-9, VIKAS VIHAR, AMBALA CITY-15003, HARYANA. PH: 0171-2550913, MOB:-91-8866-70914 DELHI : #678, GREEN VIEW APARTMENTS, SECTOR 19, POCKET-2, DWARKA, NEW DELHI. MOB:-91-8866-70914 Mob:- 819907006, 8896550913, e-mail: jindalstructure@gmail.com, jindals13@gmail.com, Web: www.jindalconsortium.in				