



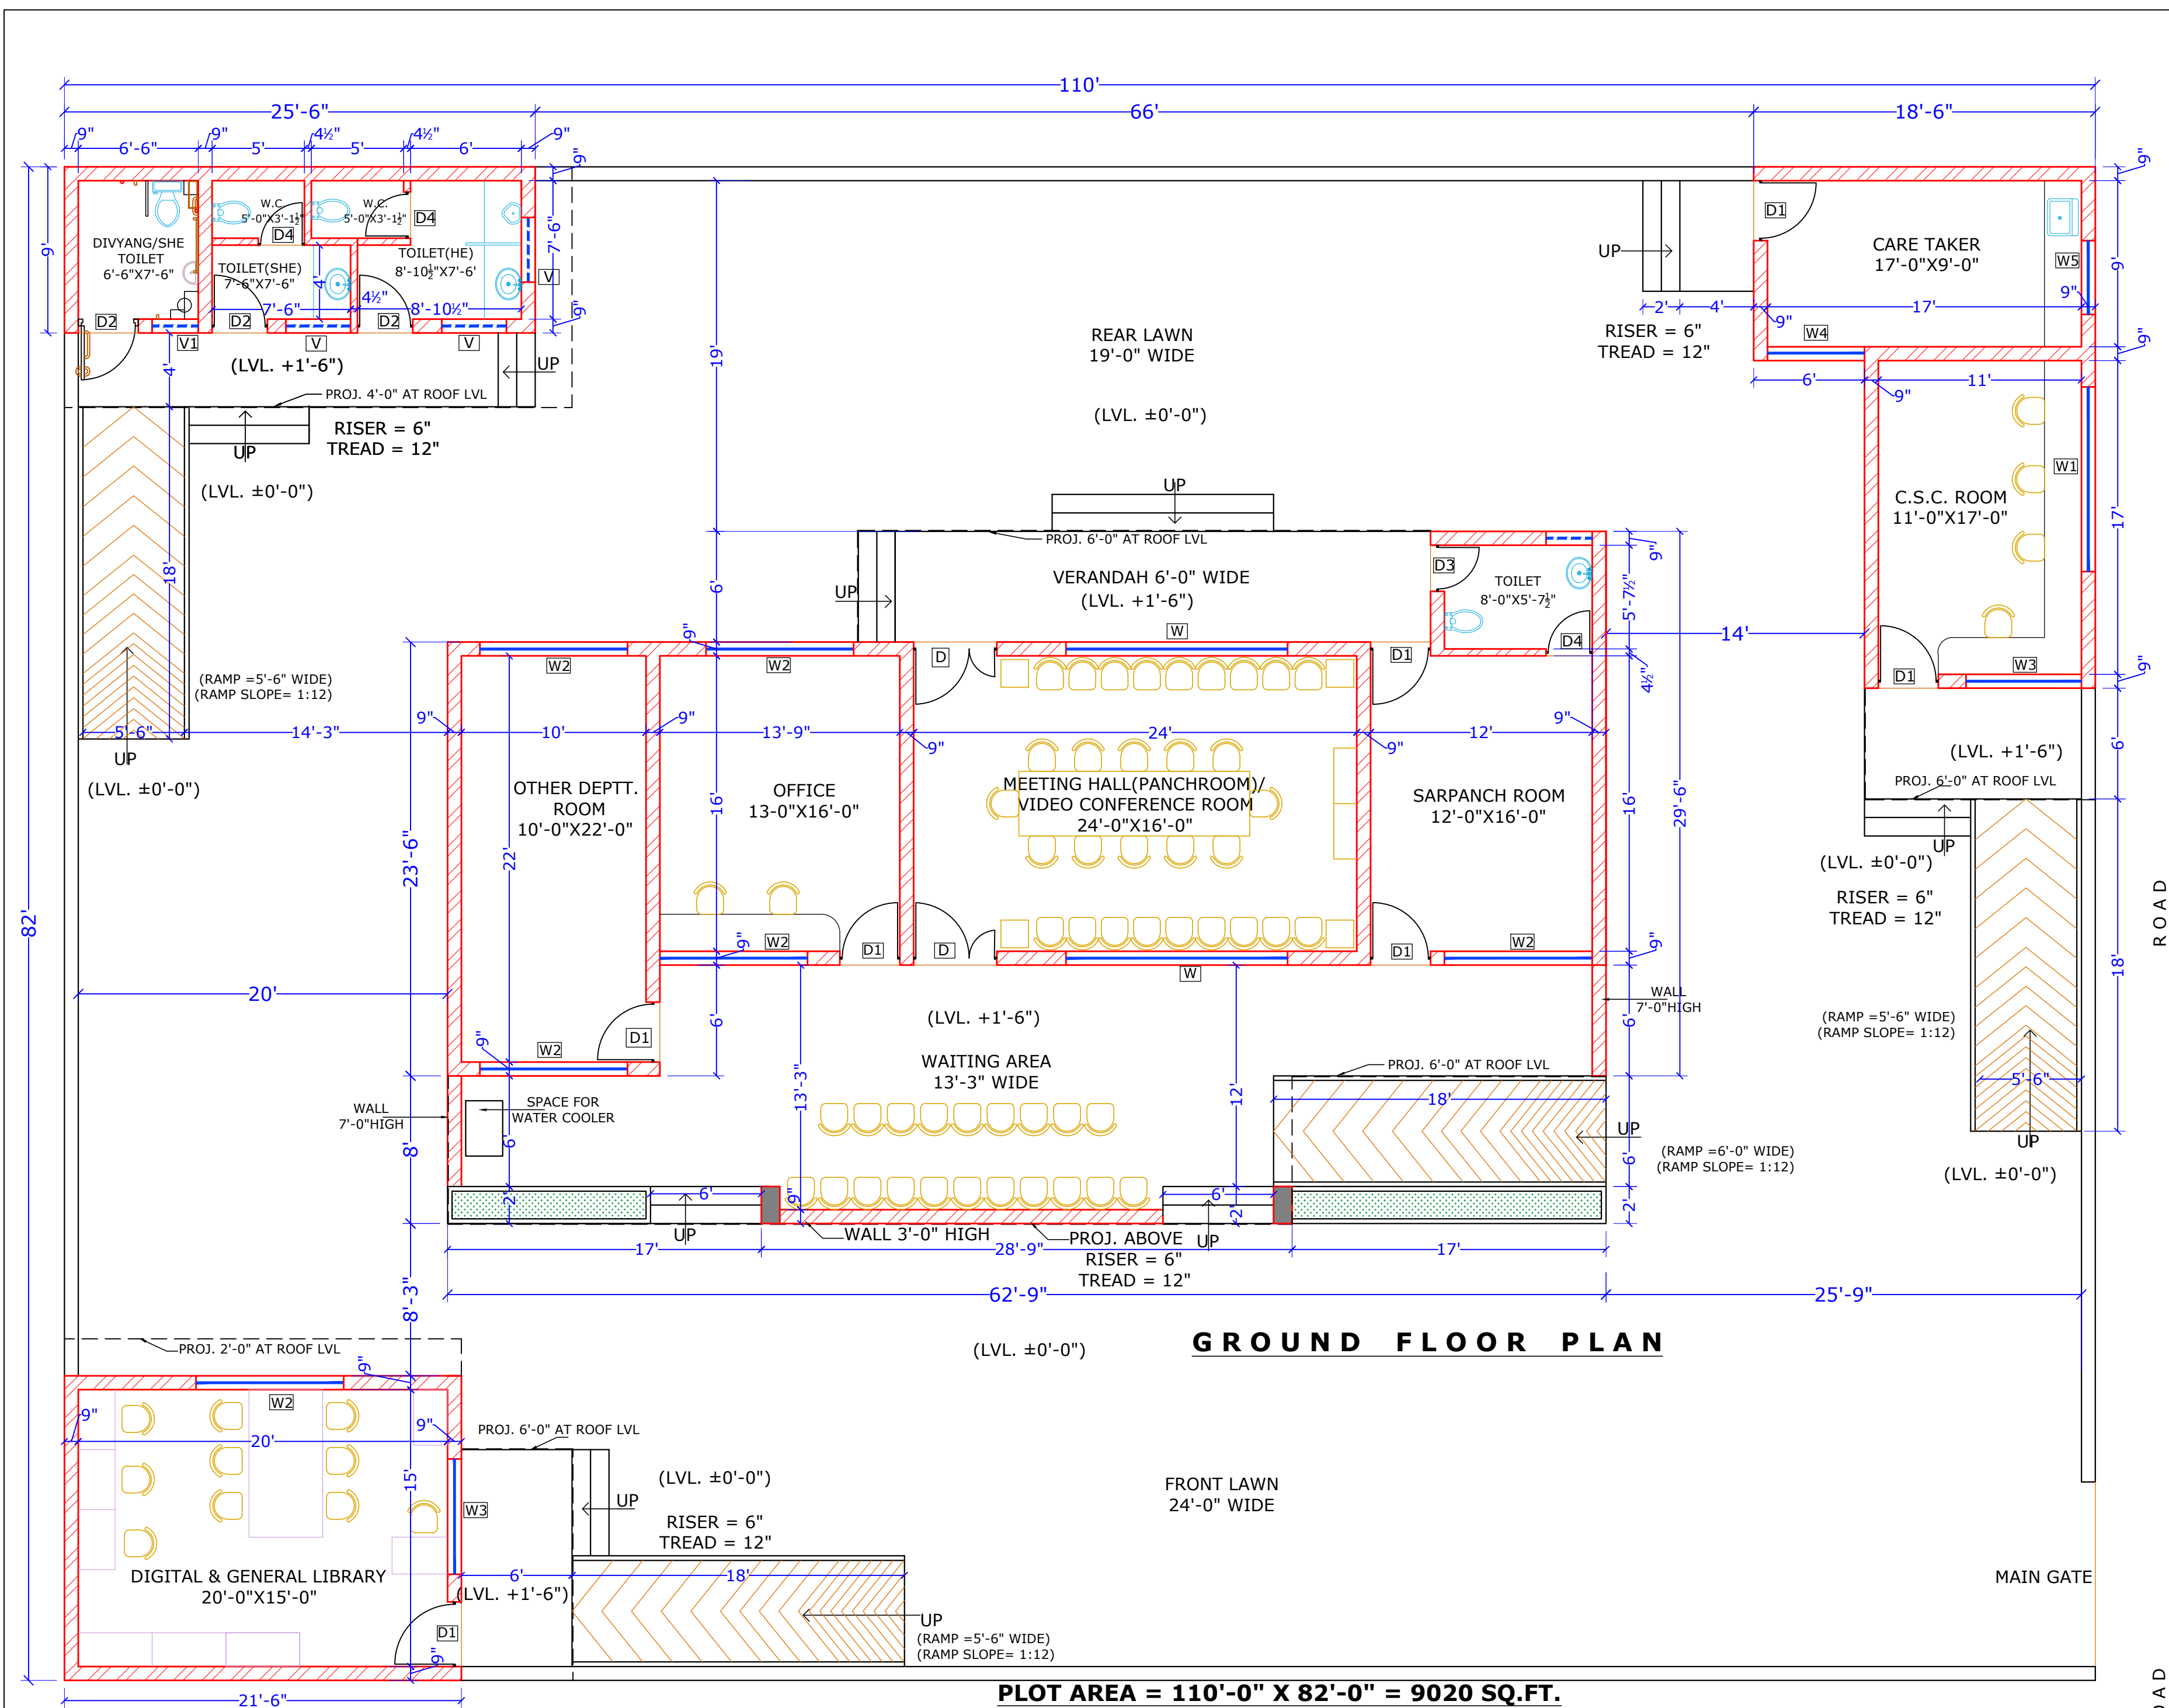

LAYOUT PLAN

PLOT AREA = 110'-0" X 82'-0" = 9020 SQ.FT.
COVERED AREA:
MAIN OFFICE BLOCK = 1896.0 SQ.FT.
CARE TAKER BLOCK = 416.0 SQ.FT.
TOILET BLOCK = 230.0 SQ.FT.
DIGITAL LIBRARY BLOCK = 355.0 SQ.FT.
TOTAL COVERD AREA = 2897.0 SQ.FT. OR 269.0 SQ.MT.

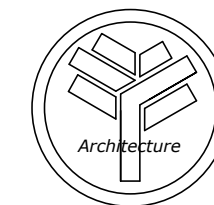

REVISION

S.N.	DATE	DESCRIPTION	BY

THIS DRG. IS THE PROPERTY OF THE DEPTT. OF ARCHITECTURE GOVT. OF HARYANA. IT MAY NOT BE ALTERED COPIED USED IN WHOLE OR IN PART WITHOUT THE PERMISSION OF THIS DEPTT.

GENERAL NOTES

THE DISCREPANCY IF ANY MUST BE BROUGHT TO BE NOTICE OF CONCERNED ARCHITECT BEFORE CONSTRUCTION

SCHEDULE OF JOINERY

TYPE	SIZE	CILL	TOP	REMARKS
D	4'-6"X8'-6"	-	8'-6"	
D1	3'-3"X8'-6"	-	8'-6"	
D2	3'-0"X8'-6"	-	8'-6"	
D3	2'-6"X8'-6"	-	8'-6"	
D4	2'-6"X7'-0"	-	7'-0"	
W	12'-0"X6'-0"	2'-6"	8'-6"	
W1	10'-0"X6'-0"	2'-6"	8'-6"	
W2	8'-0"X6'-0"	2'-6"	8'-6"	
W3	6'-0"X6'-0"	2'-6"	8'-6"	
W4	5'-3"X6'-0"	2'-6"	8'-6"	
W5	4'-0"X5'-0"	3'-6"	8'-6"	
V	3'-6"X3'-0"	5'-6"	8'-6"	
V1	2'-6"X3'-0"	5'-6"	8'-6"	

AR. B.M. SHARMA
CHIEF ARCHITECT

AR. ANIL K. WALIA
SENIOR ARCHITECT

AR. AMAN JAIN
ARCHITECT

AR. ABHILASH RAWAT
ASSTT. ARCHITECT.

OFFICE OF THE
CHIEF ARCHITECT
HARYANA CHANDIGARH

STANDARD GRAM SACHIVALYA CUM
VILLAGE KNOWLEDGE CENTRE.

ASHA (S.D.) DEALT BY:	CHECKED BY:
JOB. NO. 2809	SCALE: 1/8" = 1'-0"
DRG. NO. 1	DATE: AUGUST 2021

CONCEPTUAL PLAN